
КУХНЯ-ГОСТИНАЯ | ВАРИАНТ А | М 1:25

B01 и проемы - фактические. Мебель и техника - проектные габаритные конверты до выбора SKU.

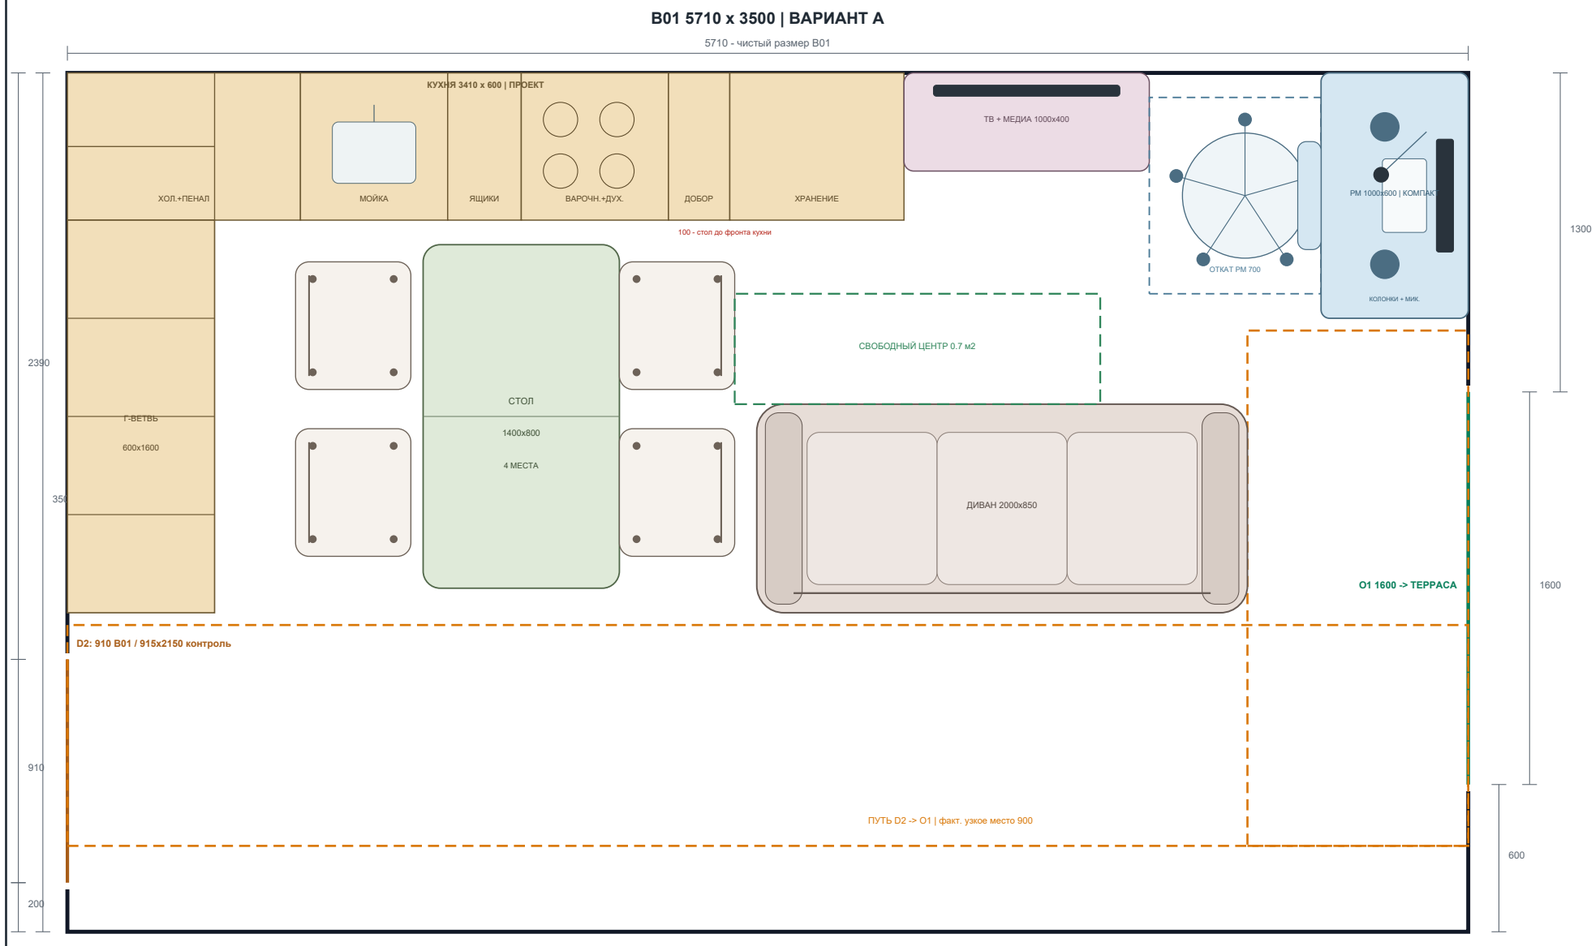

A - КЛАССИЧЕСКИЙ БАЛАНС

Г-кухня, обычный стол, диван лицом к ТВ,

компактное РМ у O1

2.3/5

ИЗМЕРИМАЯ ОЦЕНКА

Маршрут D2-O1	900	4
У кухни	100	1
За стулом	90	1
Откат РМ	700	2
Закр. хранение*	5010	5
Своб. прямоуг.*	0.7 м2	1
Ребёнок/питомцы*	2 рег.	2

ПЛЮСЫ

+ Полноценный стол на 4

+ Максимум кухонного хранения

+ Прямой обзор ТВ

КОМПРОМИССЫ

- РМ только 1000x600

- 100 мм у рабочего фронта

- 90 мм и 2 тесные зоны для ребёнка/питомцев

1000 мм = 40 мм на листе

ФАКТ: B01 5710x3500; D2 200+910 (контроль 915x2150); O1 600+1600+1300.

РЕКОМЕНДАЦИИ NKBA, не нормы РБ: проход 914; рабочий проход 1067 для одного; за стулом без транзита 813.

ПРОЕКТ*: откат РМ 900; хранение = кухня + закрытая сторона полуострова/банкетки; свободный прямоугольник считается выше маршрута.

ОЦЕНКА: проходы 5=ориентир; 4=до 50 ниже; 3=51-150; 2=151-250; 1=>250. Хранение: 5>=4000; 4>=3400; 3>=2800; 2>=2200; 1<2200.

СВОБ. ЗОНА*: 5>=4.0; 4>=3.0; 3>=2.2; 2>=1.5; 1<1.5 м2 непрерывного незанятого пола выше маршрута.


СЕМЬЯ*: 5=нет конфликтов; 4=один редкий; 3=один регулярный; 2=два; 1=три и более либо блокировка маршрута ребёнком/питомцем.

КОНТРОЛЬ: вода, E-01, радиаторы и конкретные модели мебели/техники требуют привязки до рабочей документации.

КУХНЯ-ГОСТИНАЯ | ВАРИАНТ B | М 1:25

B01 и проемы - фактические. Мебель и техника - проектные габаритные конверты до выбора SKU.

B01 5710 x 3500 | ВАРИАНТ B

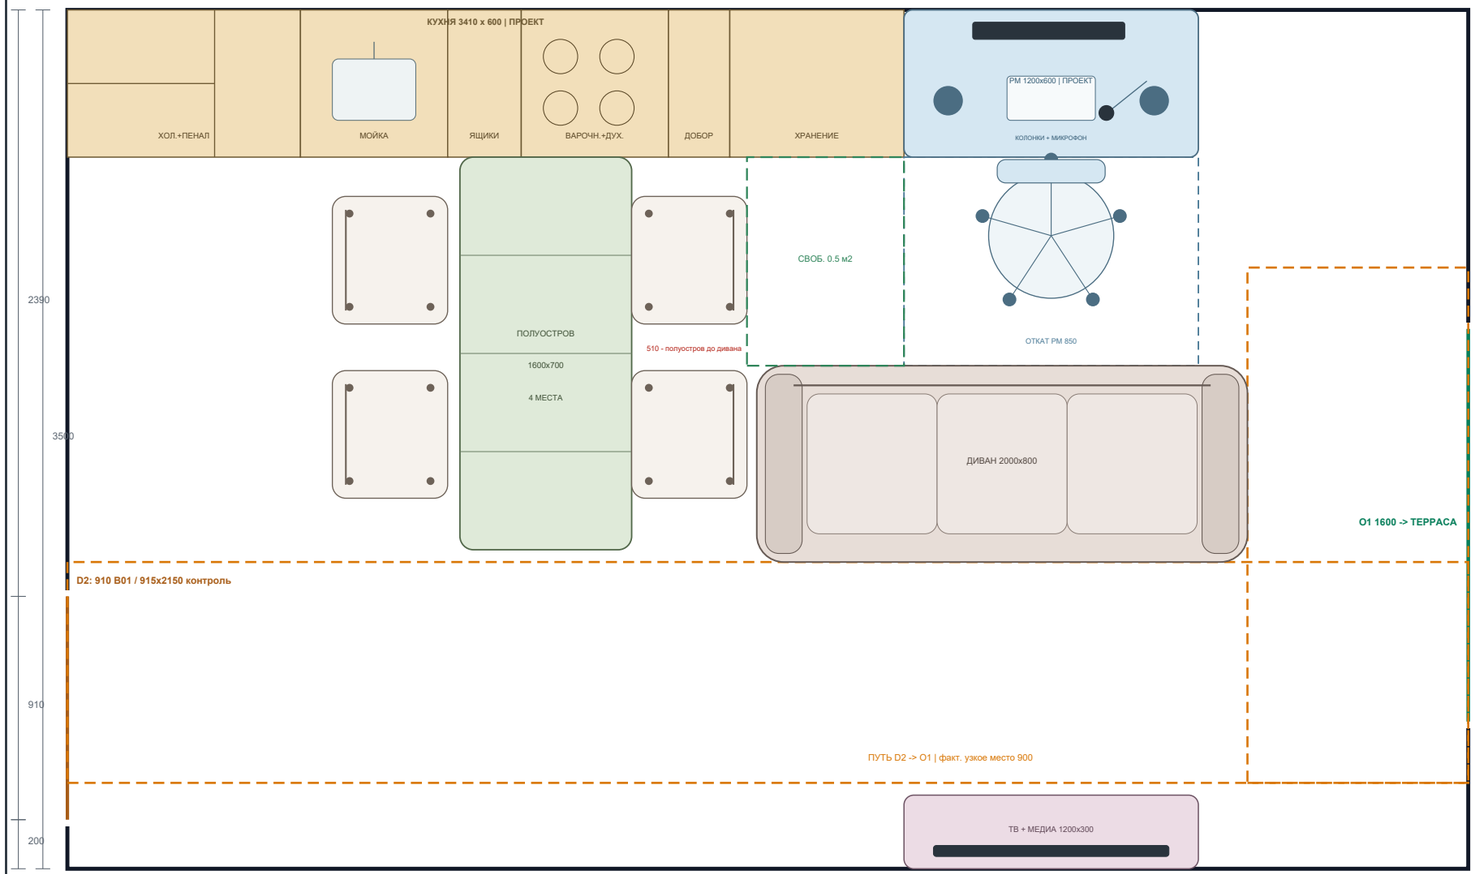

1000 мм = 40 мм на листе

B - КУХНЯ С ПОЛУОСТРОВОМ

Прямая кухня, РМ в верхней линии, полуостров для еды и хранения

2.6/5

ИЗМЕРИМАЯ ОЦЕНКА

Маршрут D2-O1	900	4
У полуострова	510	1
За стулом	40	1
Откат РМ	850	4
Закр. хранение*	5010	5
Своб. прямоуг.*	0.5 м2	1
Ребёнок/питомцы*	2 рег.	2

ПЛЮСЫ

+ Больше столешницы
+ Четыре посадочных места
+ РМ шириной 1200

КОМПРОМИССЫ

- 40 мм за правыми стульями
- Стулья конфликтуют с путём ребёнка/питомцев
- Узкий боковой проход 510

ФАКТ: B01 5710x3500; D2 200+910 (контроль 915x2150); O1 600+1600+1300.

РЕКОМЕНДАЦИИ NKBA, не нормы РБ: проход 914; рабочий проход 1067 для одного; за стулом без транзита 813.

ПРОЕКТ*: откат РМ 900; хранение = кухня + закрытая сторона полуострова/банкетки; свободный прямоугольник считается выше маршрута.

ОЦЕНКА: проходы 5=ориентир; 4=до 50 ниже; 3=51-150; 2=151-250; 1=>250. Хранение: 5>=4000; 4>=3400; 3>=2800; 2>=2200; 1<2200.


СВОБ. ЗОНА*: 5>=4.0; 4>=3.0; 3>=2.2; 2>=1.5; 1<1.5 м2 непрерывного незанятого пола выше маршрута.

СЕМЬЯ*: 5=нет конфликтов; 4=один редкий; 3=один регулярный; 2=два; 1=три и более либо блокировка маршрута ребёнком/питомцем.

КОНТРОЛЬ: вода, E-01, радиаторы и конкретные модели мебели/техники требуют привязки до рабочей документации.

КУХНЯ-ГОСТИНАЯ | ВАРИАНТ C | М 1:25

B01 и проемы - фактические. Мебель и техника - проектные габаритные конверты до выбора SKU.

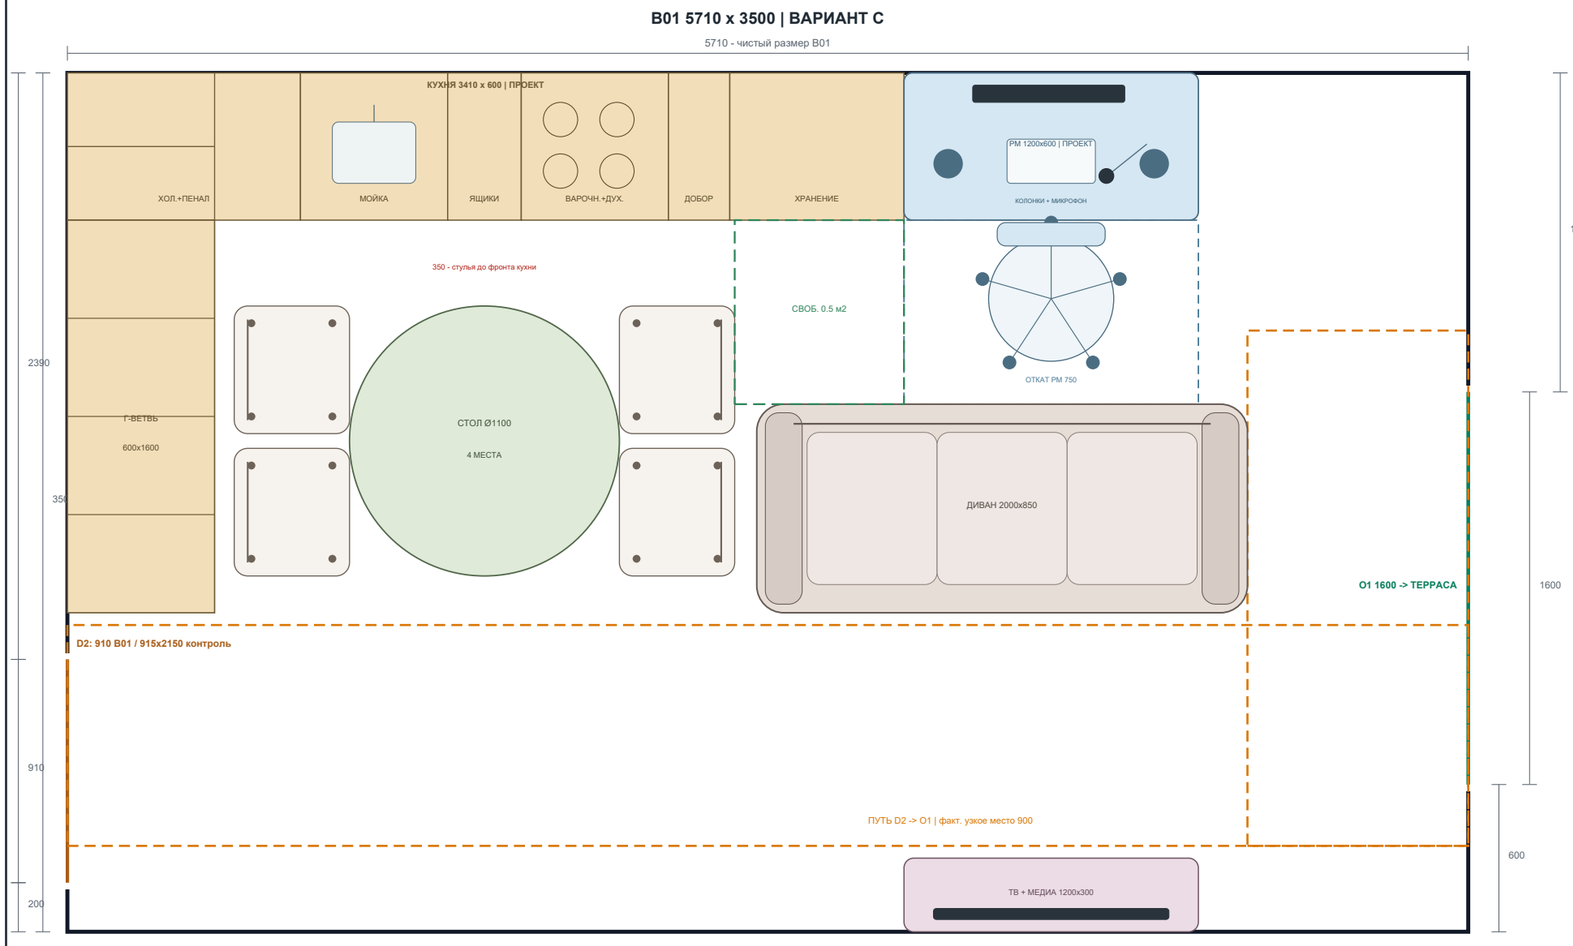

C - КРУГЛЫЙ СТОЛ + ВСТРОЕННОЕ РМ

Г-кухня, круглый стол, РМ в общей верхней линии, диван-зонирование

2.3/5

ИЗМЕРИМАЯ ОЦЕНКА

Маршрут D2-O1	900	4
У кухни	350	1
За стулом	90	1
Откат РМ	750	3
Закр. хранение*	5010	5
Своб. прямоуг.*	0.5 м2	1
Ребёнок/питомцы*	3 рег.	1

ПЛЮСЫ

+ Мягкая круглая геометрия

+ РМ 1200x600

+ Удобное общение за столом

КОМПРОМИССЫ

- 350 мм у рабочего фронта

- 90 мм у дивана; 3 тесные зоны для ребёнка/питомцев

- Откат кресла только 750

1000 мм = 40 мм на листе

ФАКТ: B01 5710x3500; D2 200+910 (контроль 915x2150); O1 600+1600+1300.

РЕКОМЕНДАЦИИ NKBA, не нормы РБ: проход 914; рабочий проход 1067 для одного; за стулом без транзита 813.

ПРОЕКТ*: откат РМ 900; хранение = кухня + закрытая сторона полуострова/банкетки; свободный прямоугольник считается выше маршрута.

ОЦЕНКА: проходы 5=ориентир; 4=до 50 ниже; 3=51-150; 2=151-250; 1=>250. Хранение: 5>=4000; 4>=3400; 3>=2800; 2>=2200; 1<2200.


СВОБ. ЗОНА*: 5>=4.0; 4>=3.0; 3>=2.2; 2>=1.5; 1<1.5 м2 непрерывного незанятого пола выше маршрута.

СЕМЬЯ*: 5=нет конфликтов; 4=один редкий; 3=один регулярный; 2=два; 1=три и более либо блокировка маршрута ребёнком/питомцем.

КОНТРОЛЬ: вода, E-01, радиаторы и конкретные модели мебели/техники требуют привязки до рабочей документации.

КУХНЯ-ГОСТИНАЯ | ВАРИАНТ D | М 1:25

B01 и проемы - фактические. Мебель и техника - проектные габаритные конверты до выбора SKU.

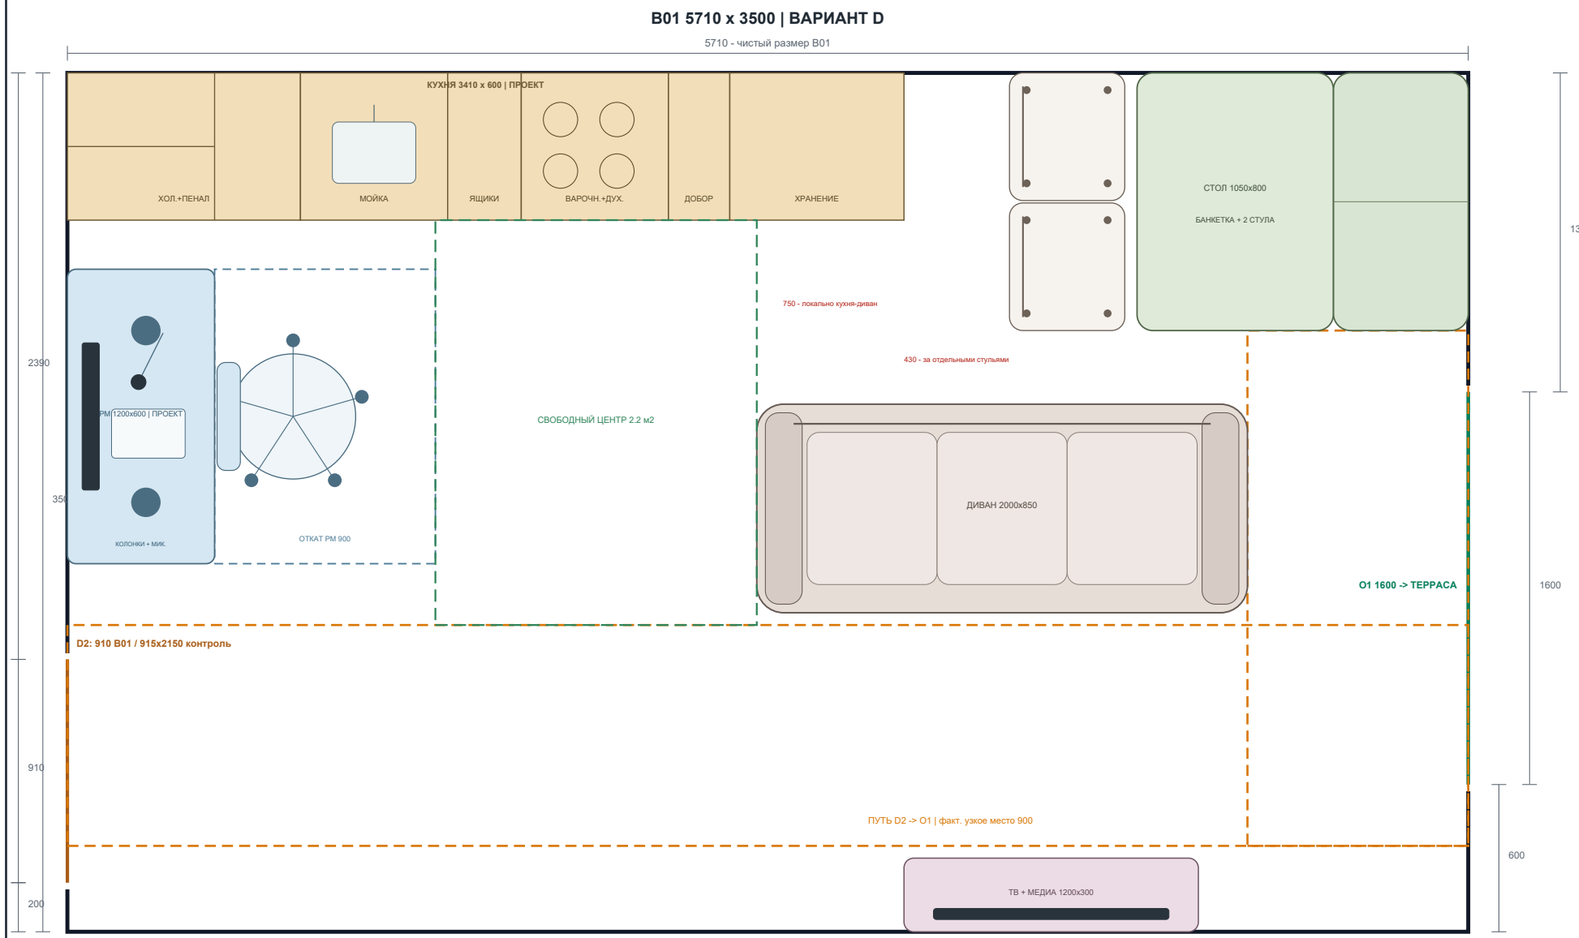

1000 мм = 40 мм на листе

D - СЕМЕЙНАЯ БАНКЕТКА

Прямая кухня, РМ слева, банкетка у верхнего простенка O1, свободный центр

3.3/5
РЕКОМЕНДУЮ

ИЗМЕРИМАЯ ОЦЕНКА

Маршрут D2-O1	900	4
Кухня-диван	750	1
За стулом	430	1
Откат РМ	900	5
Закр. хранение*	4460	5
Своб. прямоуг.*	2.2 м2	3
Ребёнок/питомцы*	1 редк.	4

ПЛЮСЫ

+ Свободный центр для ребёнка/питомцев

+ РМ 1200x600 вне маршрута

+ Детям удобно на банкетке

КОМПРОМИССЫ

- Локально кухня-диван 750

- 430 мм за отдельными стульями

- Банкетка только на заказ

ФАКТ: B01 5710x3500; D2 200+910 (контроль 915x2150); O1 600+1600+1300.

РЕКОМЕНДАЦИИ NKBA, не нормы РБ: проход 914; рабочий проход 1067 для одного; за стулом без транзита 813.

ПРОЕКТ*: откат РМ 900; хранение = кухня + закрытая сторона полуострова/банкетки; свободный прямоугольник считается выше маршрута.

ОЦЕНКА: проходы 5=ориентир; 4=до 50 ниже; 3=51-150; 2=151-250; 1=>250. Хранение: 5>=4000; 4>=3400; 3>=2800; 2>=2200; 1<2200.

СВОБ. ЗОНА*: 5>=4.0; 4>=3.0; 3>=2.2; 2>=1.5; 1<1.5 м2 непрерывного незанятого пола выше маршрута.


СЕМЬЯ*: 5=нет конфликтов; 4=один редкий; 3=один регулярный; 2=два; 1=три и более либо блокировка маршрута ребёнком/питомцем.

КОНТРОЛЬ: вода, E-01, радиаторы и конкретные модели мебели/техники требуют привязки до рабочей документации.

КУХНЯ-ГОСТИНАЯ | D+1 - ЕЖЕДНЕВНО | М 1:25

B01 и проёмы - фактические. Мебель - проектные конверты. Новых стен нет.

B01 5710 x 3500 | ВАРИАНТ D+1 - ЕЖЕДНЕВНО

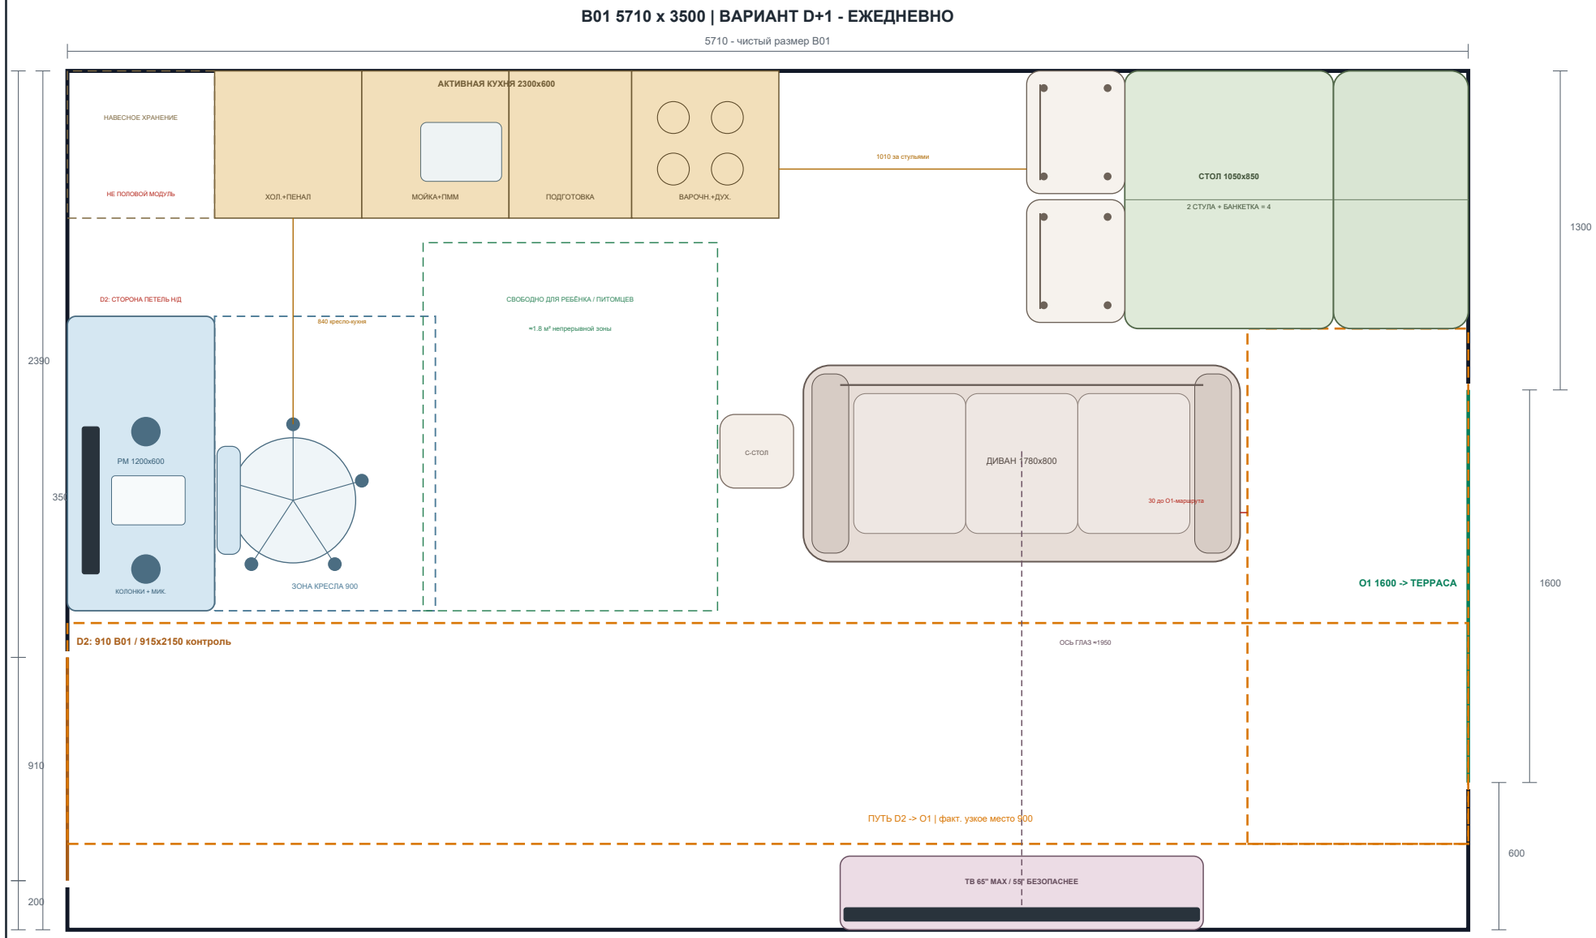

D+1 - ЕЖЕДНЕВНО

Кухня	**2300x600, компакт**
Рабочее место	**1200x600**
Диван	**1780x800, 3**
Стол	**1050x850, 4**
Путь D2-O1	**900, PASS**
ТВ	**65 max; ось ≈1950**

ЧТО УЛУЧШЕНО

+ Отдельный мягкий диван, не банкетка
+ Рабочее кресло имеет резерв 900
+ 1010 за обеденными стульями
+ Гостевой режим без переноса тяжёлой мебели

ЧЕСТНЫЕ ОГРАНИЧЕНИЯ

- Кухня 2300 - компактная
- Стол на 4; 7-9 только для общения
- Локально кресло-кухня 840
- До О1-зоны от дивана лишь 30

1000 мм = 40 мм на листе

ФАКТ: B01 5710x3500; D2 слева 200+910 (контроль 915x2150); О1 справа 600+1600+1300.

P0 PASS: защищённые полосы 900 мм D2-O1 проверены численно; мебель и кресла их не пересекают.

D+: кухня 2300; стол 1050x850 на 4; диван 1780x800; РМ 1200x600; ТВ 55-65.

ГОСТИ: 4 за столом + 3 на диване + 2 пуфа = до 9 только для общения, не для общего ужина.

ЗАЗОРЫ: 1010 за обеденными стульями; 840 кресло-кухня; 250 над путём; 30 до зоны О1.


СТАТУС: концепция мебели, не рабочий чертёж и не основание для заказа.

ГЕЙТЫ: сторона петель D2, вода, канализация, вентиляция, E-01, отопление и реальные SKU.

КУХНЯ-ГОСТИНАЯ | D+2 - СОЦИАЛЬНЫЕ ГОСТИ | М 1:25

B01 и проёмы - фактические. Мебель - проектные конверты. Новых стен нет.

B01 5710 x 3500 | ВАРИАНТ D+2 - СОЦИАЛЬНЫЕ ГОСТИ

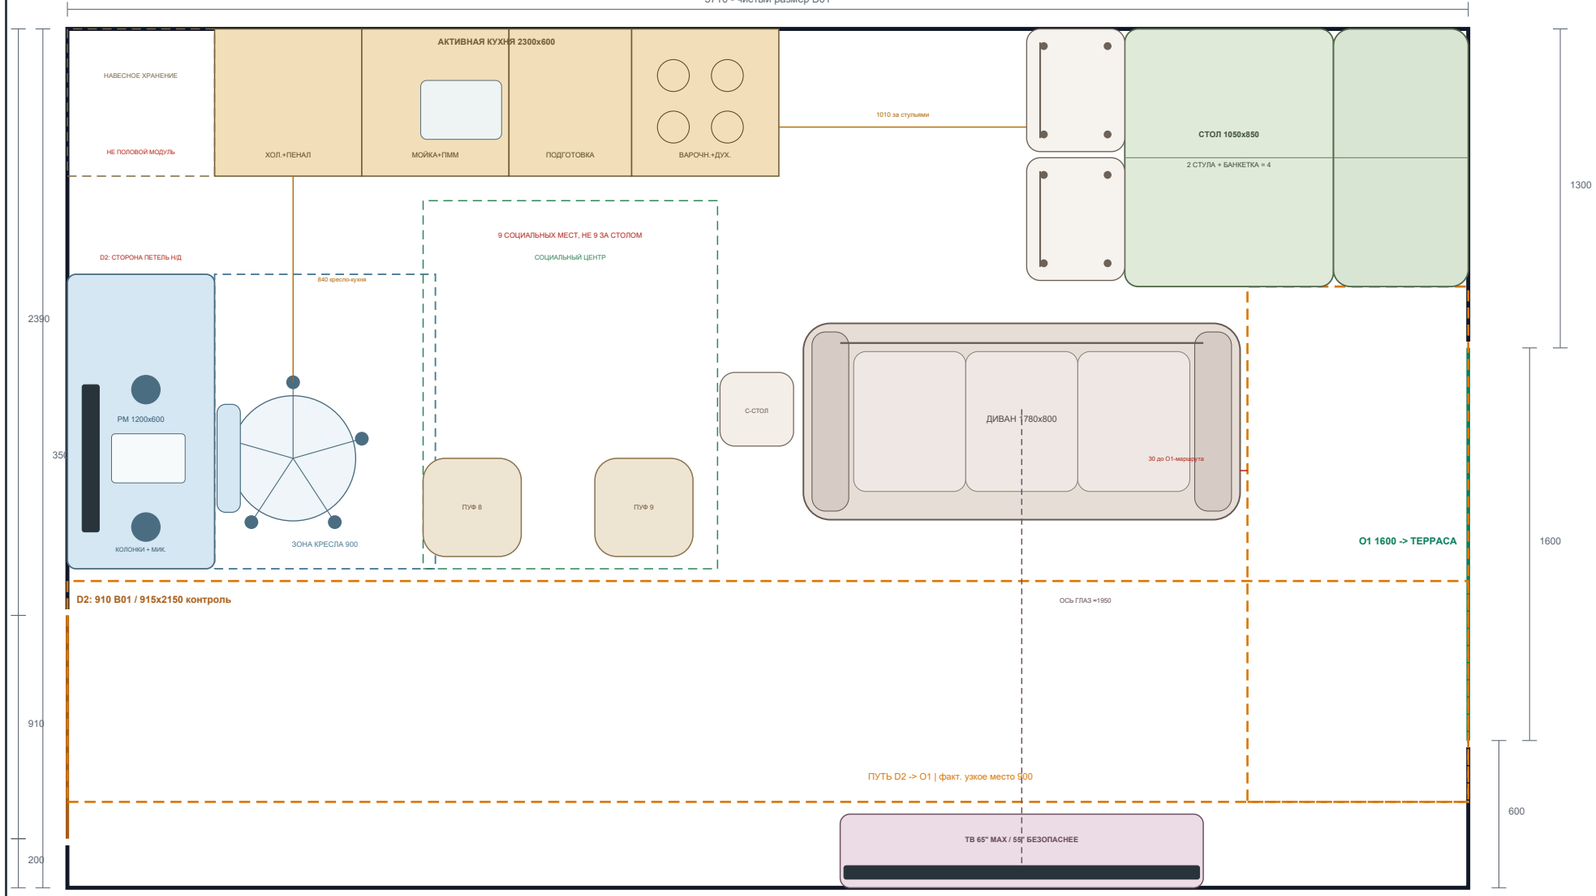

D+2 - ГОСТИ / ОБЩЕНИЕ

За столом	**4**
На диване	**3**
Мобильные пуфы	**2**
Социальная посадка	**до 9**
Ужин	**только 4**
Путь D2-O1	**900, PASS**

ЧТО УЛУЧШЕНО

+ Отдельный мягкий диван, не банкетка
+ Рабочее кресло имеет резерв 900
+ 1010 за обеденными стульями
+ Гостевой режим без переноса тяжёлой мебели

ЧЕСТНЫЕ ОГРАНИЧЕНИЯ

- Кухня 2300 - компактная
- Стол на 4; 7-9 только для общения
- Локально кресло-кухня 840
- До О1-зоны от дивана лишь 30

1000 мм = 40 мм на листе

ФАКТ: B01 5710x3500; D2 слева 200+910 (контроль 915x2150); О1 справа 600+1600+1300.

P0 PASS: защищённые полосы 900 мм D2-O1 проверены численно; мебель и кресла их не пересекают.

D+: кухня 2300; стол 1050x850 на 4; диван 1780x800; РМ 1200x600; ТВ 55-65.

ГОСТИ: 4 за столом + 3 на диване + 2 пуфа = до 9 только для общения, не для общего ужина.

ЗАЗОРЫ: 1010 за обеденными стульями; 840 кресло-кухня; 250 над путём; 30 до зоны О1.


СТАТУС: концепция мебели, не рабочий чертёж и не основание для заказа.

ГЕЙТЫ: сторона петель D2, вода, канализация, вентиляция, E-01, отопление и реальные SKU.

КУХНЯ-ГОСТИНАЯ | ВАРИАНТ E | E1 - ЕЖЕДНЕВНО | M 1:25

B01 и проёмы - фактические. Мебель - проектные габариты. Стены и проёмы не меняются.

B01 5710 x 3500 | ВАРИАНТ E1 - ЕЖЕДНЕВНО

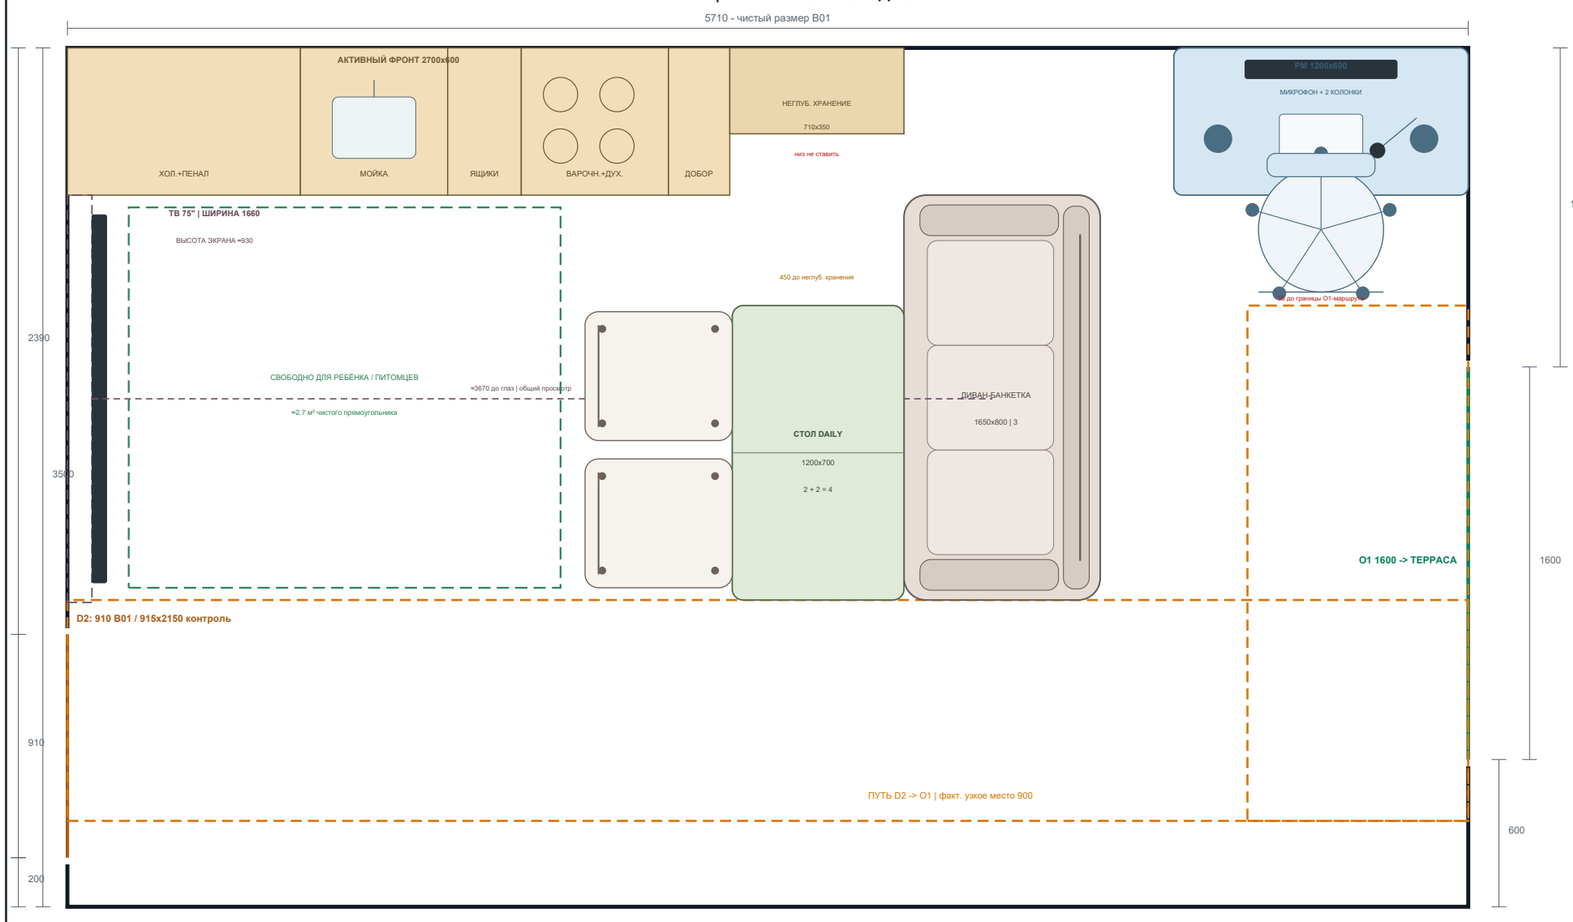

1000 мм = 40 мм на листе

ФАКТ: B01 5710x3500; D2 слева 200+910 (контроль 915x2150); О1 справа 600+1600+1300.

ПУТЬ: защищённая проектная полоса 900 мм сохранена; это не заявление о соответствии нормам РБ.

E: активная кухня 2700x600; хранение 710x350; стол 1200->1650x700; диван 1650x800; РМ 1200x600.

ГОСТИ: 6 посадок = 3 на прямом диване + 3 на стульях; 550 мм на человека - допустимо лишь эпизодически.

ТВ: панель 75" приблизительно 1660x930; дистанция до глаз около 3670; проектор требует отдельного расчёта.

ГЕЙТЫ: сторона D2, наличники, вода, вентиляция, E-01, отопление и реальные SKU должны быть промерены до заказа.

РМ: кресло в рабочем положении не входит в О1-маршрут (запас 55); при откате назад пересечение временно возможно.

E1 - ЕЖЕДНЕВНЫЙ РЕЖИМ

Стол	**1200x700, 4 места**
Диван	**1650x800, прямой**
ТВ	**75", ось ≈3670**
Рабочее место	**1200x600**
Путь D2-О1	**900, свободен**
Свободный центр	**≈2.7 м²**

ПОЧЕМУ ЭТО СИЛЬНЕЕ D

+ ТВ развёрнут по длинной оси комнаты

+ Один стол обслуживает 4 и 6 человек

+ Диван работает и как мягкая банкетка

+ Не перекрываются D2, О1 и путь 900

ЧЕСТНЫЕ КОМПРОМИССЫ

- Нужен прямой диван с посадкой 430-470

- 6 мест - редкий компактный режим


- Выдвижение кресла РМ временно касается пути

- Крепление ТВ - только после проверки D2

КУХНЯ-ГОСТИНАЯ | ВАРИАНТ E | E2 - ГОСТИ | M 1:25

B01 и проёмы - фактические. Мебель - проектные габариты. Стены и проёмы не меняются.

B01 5710 x 3500 | ВАРИАНТ E2 - ГОСТИ

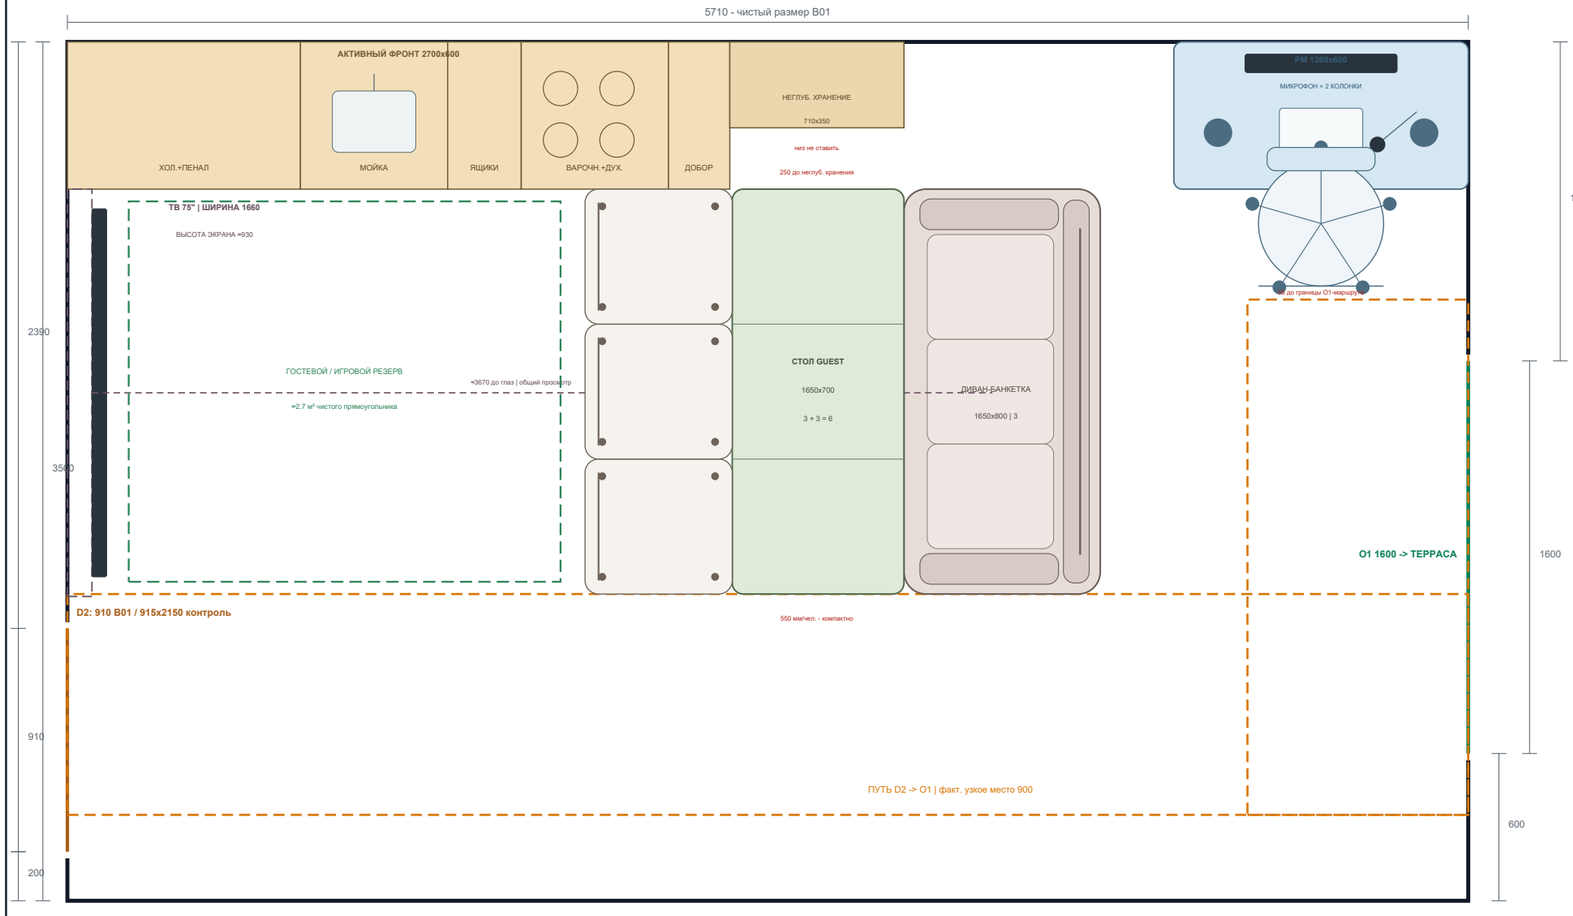

E2 - ГОСТЕВОЙ РЕЖИМ

Стол	**1650x700**
Посадка	**3 диван + 3 стула**
Ширина на гостя	**550 - компактно**
Путь D2-O1	**900, свободен**
Рабочее место	**остаётся на месте**
Кухня	**активные 2700 доступны**

ПОЧЕМУ ЭТО СИЛЬНЕЕ D

+ ТВ развёрнут по длинной оси комнаты

+ Один стол обслуживает 4 и 6 человек

+ Диван работает и как мягкая банкетка

+ Не перекрываются D2, O1 и путь 900

ЧЕСТНЫЕ КОМПРОМИССЫ

- Нужен прямой диван с посадкой 430-470

- 6 мест - редкий компактный режим

- Выдвижение кресла РМ временно касается пути

- Крепление ТВ - только после проверки D2

1000 мм = 40 мм на листе

ФАКТ: B01 5710x3500; D2 слева 200+910 (контроль 915x2150); O1 справа 600+1600+1300.

ПУТЬ: защищённая проектная полоса 900 мм сохранена; это не заявление о соответствии нормам РБ.

E: активная кухня 2700x600; хранение 710x350; стол 1200->1650x700; диван 1650x800; РМ 1200x600.

ГОСТИ: 6 посадок = 3 на прямом диване + 3 на стульях; 550 мм на человека - допустимо лишь эпизодически.

ТВ: панель 75" приблизительно 1660x930; дистанция до глаз около 3670; проектор требует отдельного расчёта.


ГЕЙТЫ: сторона D2, наличники, вода, вентиляция, E-01, отопление и реальные SKU должны быть померены до заказа.

РМ: кресло в рабочем положении не входит в O1-маршрут (запас 55); при откате назад пересечение временно возможно.

КУХНЯ-ГОСТИНАЯ | E+1 - ЕЖЕДНЕВНО | M 1:25

B01 и проёмы - фактические. Мебель - проектные конверты. Новых стен нет.

B01 5710 x 3500 | ВАРИАНТ E+1 - ЕЖЕДНЕВНО

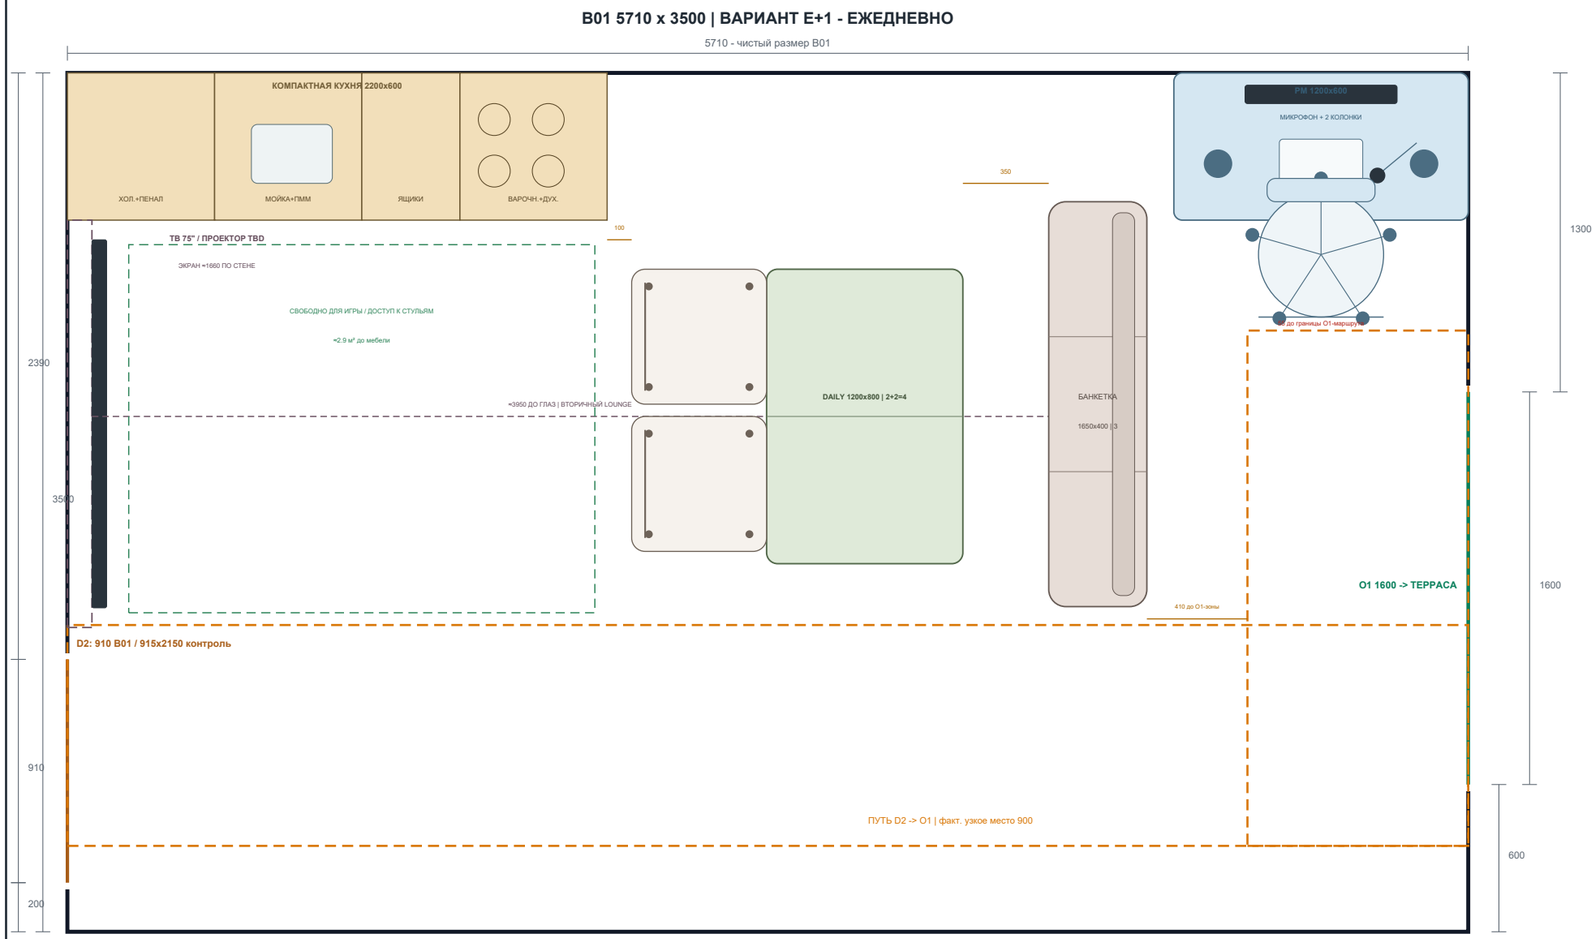

1000 мм = 40 мм на листе

ФАКТ: B01 5710x3500; D2 слева 200+910 (контроль 915x2150); O1 справа 600+1600+1300.

P0 PASS: защищённые полосы 900 мм D2-O1 проверены численно; мебель и кресла их не пересекают.

E+: кухня 2200; стол 1200->1650x800; банкетка 1650x400; РМ 1200x600.

УЖИН 6: 3 на банкетке + 3 на стульях; 550 мм/чел. - компактный, эпизодический режим.

ЗАЗОРЫ: 100 кухня-стулья по x; 350 стол-банкетка; 410 до O1-зоны; кресло РМ 55 над ней.

СТАТУС: концепция мебели, не рабочий чертёж и не основание для заказа.

ГЕЙТЫ: сторона петель D2, вода, канализация, вентиляция, E-01, отопление и реальные SKU.

E+1 - ЕЖЕДНЕВНО

Кухня	**2200x600, минимум**
Рабочее место	**1200x600**
Стол	**1200x800, 4**
Банкетка	**1650x400**
Путь D2-O1	**900, PASS**
Свободная зона	**≈2.9 м²**

ЧТО УЛУЧШЕНО

+ Шесть человек за одним столом
+ Стол глубиной 800, а не 700
+ Активная кухня не перекрыта стульями
+ 410 до защищённой зоны O1


ЧЕСТНЫЕ ОГРАНИЧЕНИЯ

- Кухня 2200 - минимальная
- Банкетка 400 - не глубокий диван
- 550 мм/чел. - компактный ужин
- Кресло РМ имеет лишь 55 до O1-зоны

КУХНЯ-ГОСТИНАЯ | E+2 - УЖИН 6 | М 1:25

B01 и проёмы - фактические. Мебель - проектные конверты. Новых стен нет.

B01 5710 x 3500 | ВАРИАНТ E+2 - УЖИН 6

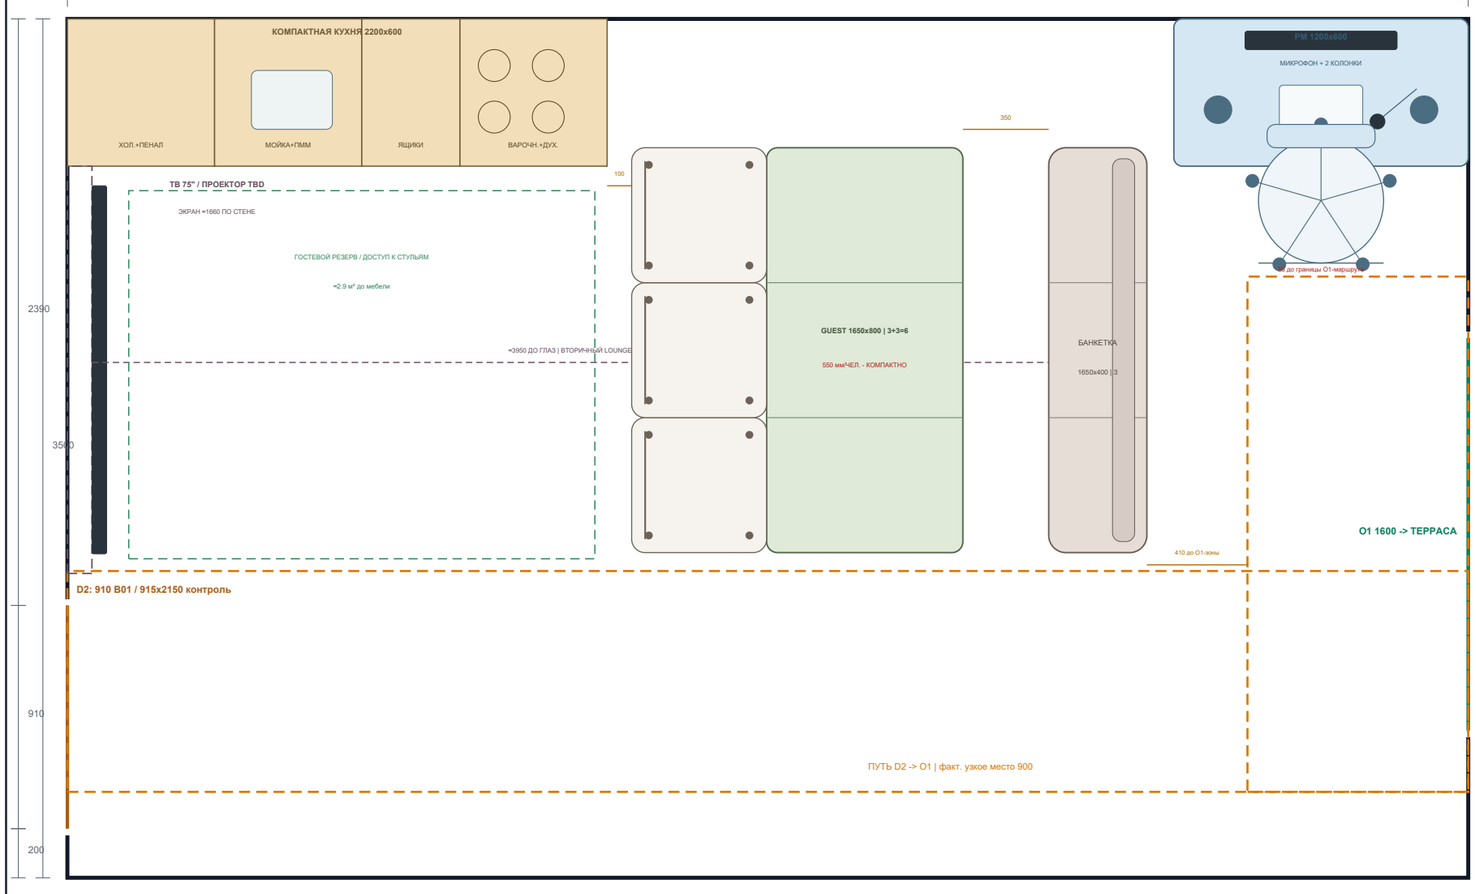

E+2 - УЖИН 6

Стол	**1650x800**
Посадка	**3+3 = 6**
Ширина места	**550, компакт**
Путь D2-O1	**900, PASS**
Рабочее место	**остаётся**
Перевод режима	**<5 минут**

ЧТО УЛУЧШЕНО

+ Шесть человек за одним столом
+ Стол глубиной 800, а не 700
+ Активная кухня не перекрыта стульями
+ 410 до защищённой зоны O1

ЧЕСТНЫЕ ОГРАНИЧЕНИЯ

- Кухня 2200 - минимальная
- Банкетка 400 - не глубокий диван
- 550 мм/чел. - компактный ужин
- Кресло PM имеет лишь 55 до O1-зоны

1000 мм = 40 мм на листе

ФАКТ: B01 5710x3500; D2 слева 200+910 (контроль 915x2150); O1 справа 600+1600+1300.

P0 PASS: защищённые полосы 900 мм D2-O1 проверены численно; мебель и кресла их не пересекают.

E+: кухня 2200; стол 1200->1650x800; банкетка 1650x400; PM 1200x600.

УЖИН 6: 3 на банкетке + 3 на стульях; 550 мм/чел. - компактный, эпизодический режим.

ЗАЗОРЫ: 100 кухня-стулья по x; 350 стол-банкетка; 410 до O1-зоны; кресло PM 55 над ней.


СТАТУС: концепция мебели, не рабочий чертёж и не основание для заказа.

ГЕЙТЫ: сторона петель D2, вода, канализация, вентиляция, E-01, отопление и реальные SKU.

КУХНЯ-ГОСТИНАЯ | STORAGE-FIRST | ЕЖЕДНЕВНО

М 1:25. В01 и проемы - фактические; мебель, техника и полезные объемы - проектные конверты.

B01 5710 x 3500 | ВАРИАНТ SF-D

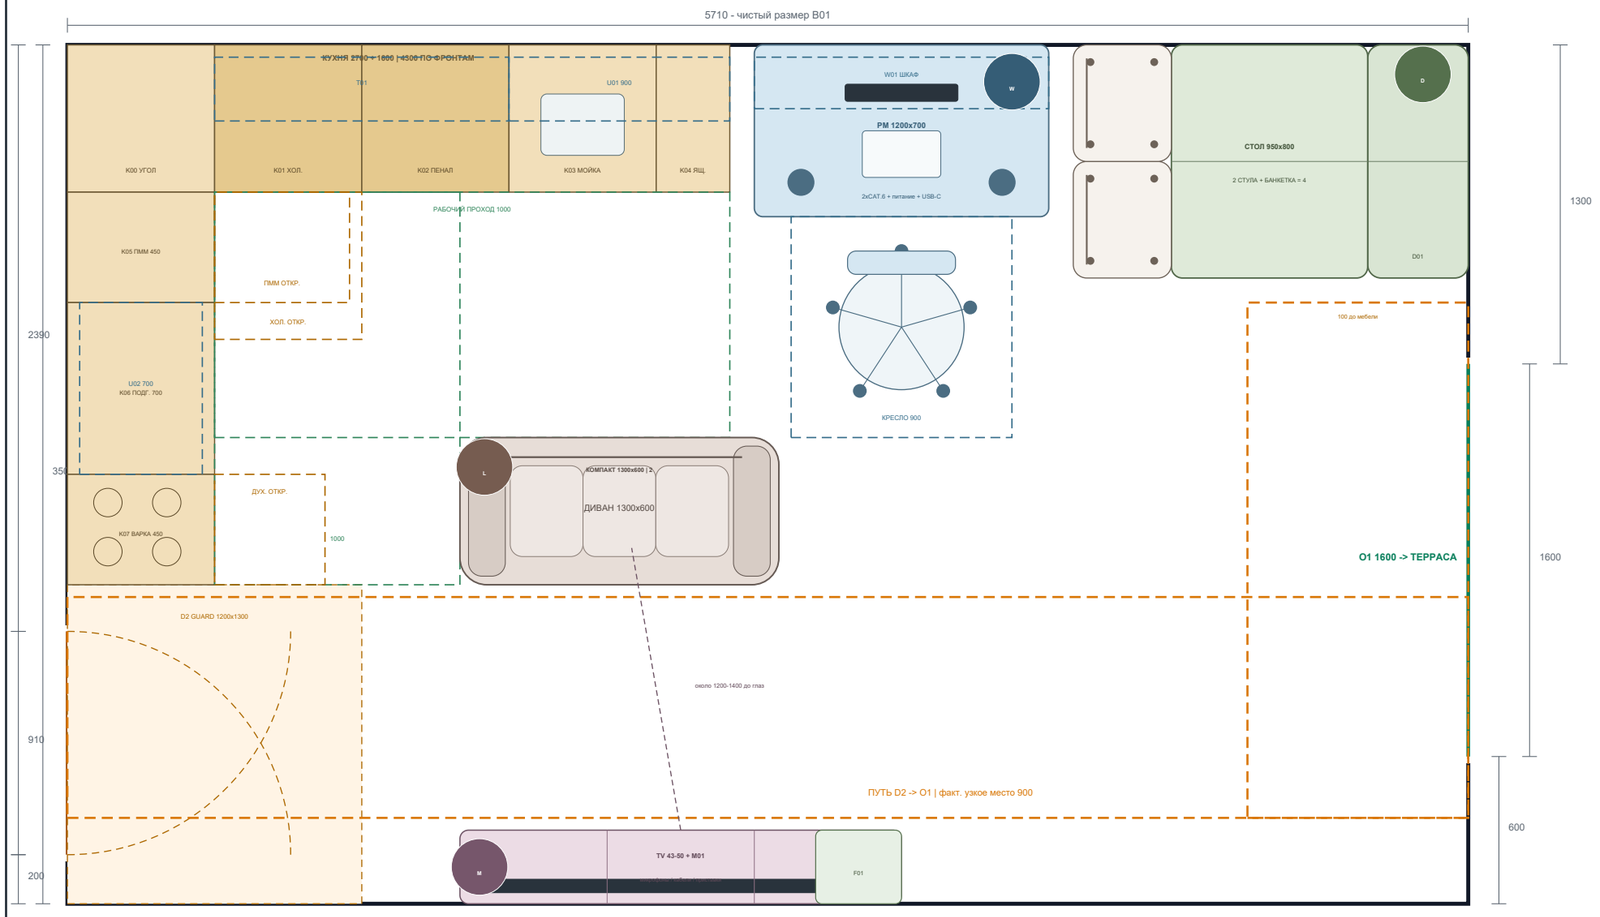

SF-1 - ЕЖЕДНЕВНО

Кухня по фронтам	**4300**
Подготовка	**700**
Рабочие проходы	**1000**
РМ	**1200x700**
Стол	**950x800 / 4**
Соц. посадка	**до 8**
Хранение	**около 1.59 м3**
Путь D2-O1	**900 PASS**

КАК ИСПОЛЬЗОВАТЬ

Готовка	K03 -> K06 -> K07; ПММ у угла
Работа	кресло 900 не входит в кухню
Хранение	ежедневное здесь, сезонное в 8
Ребенок	замки низких ящиков и anti-tip
Питомцы	F01 вне прохода; миски убирать

ЧЕСТНЫЕ ОГРАНИЧЕНИЯ

- Варочная 450 и ПММ 450 - осознанный компромисс ради хранения и проходов.
- Диван 1300x600 компактный; 65-75 дюймов и проектор эта схема не поддерживает.
- Вода, вентиляция, E-01, петли D2/O1 и высота шкафов пока не замкнуты.

1000 мм = 40 мм на листе

ФАКТ: B01 5710x3500; D2 200+910 (контроль 915x2150); O1 600+1600+1300.

PASS: фиксированная мебель и показанные динамические конверты не входят в D2 guard и путь D2-O1.

PASS: рабочая полоса кухни 1000 по двум фронтам; кресло РМ имеет конверт 900.


КОНЦЕПТ: перед заказом закрыть G1-G6 на листе 6. Ужин на 6 в эту расстановку не заявлен.

ХРАНЕНИЕ: около 1.59 м3 полезного объема без холодильника, допуск ±20 процентов до выбора SKU.

КУХНЯ-ГОСТИНАЯ | STORAGE-FIRST | ГОСТИ

М 1:25. В01 и проемы - фактические; мебель, техника и полезные объемы - проектные конверты.

B01 5710 x 3500 | ВАРИАНТ SF-G

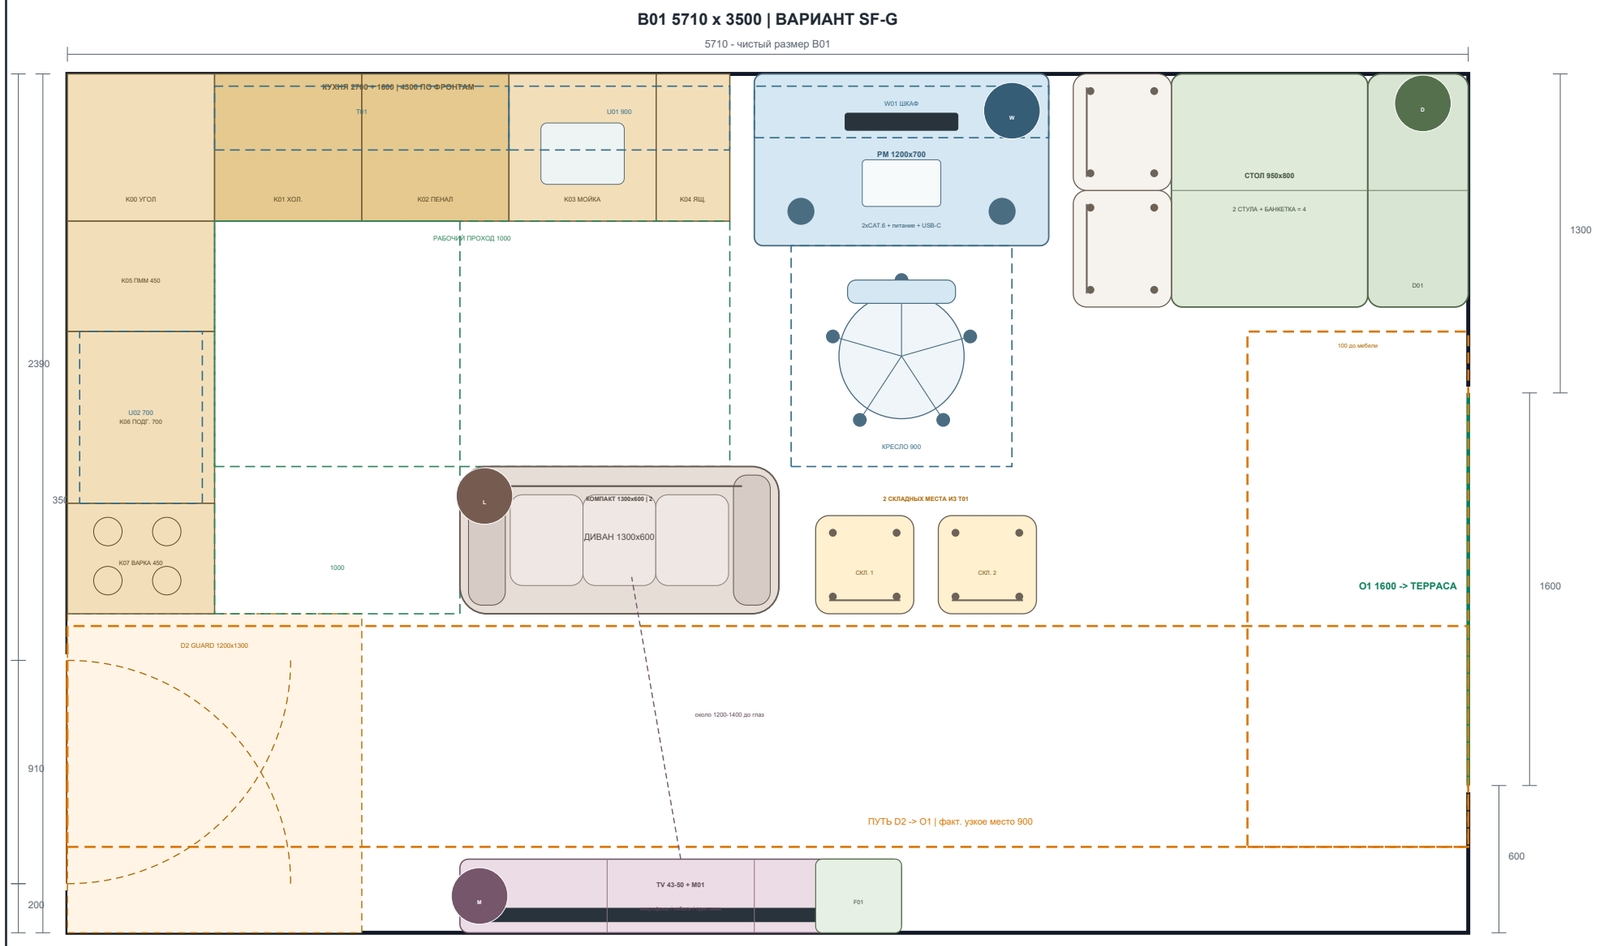

1000 мм = 40 мм на листе

ФАКТ: B01 5710x3500; D2 200+910 (контроль 915x2150); O1 600+1600+1300.

PASS: фиксированная мебель и показанные динамические конверты не входят в D2 guard и путь D2-O1.

PASS: рабочая полоса кухни 1000 по двум фронтам; кресло PM имеет конверт 900.

КОНЦЕПТ: перед заказом закрыть G1-G6 на листе 6. Ужин на 6 в эту расстановку не заявлен.

ХРАНЕНИЕ: около 1.59 м3 полезного объема без холодильника, допуск ±20 процентов до выбора SKU.

SF-2 - ГОСТИ / ОБЩЕНИЕ

За столом	**4**
Компакт-диван	**2**
Складные стулья	**2**
Всего социально	**до 8**
Ужин	**только 4**
Путь D2-O1	**900 PASS**
O1 до мебели	**100**
Перевод режима	**до 3 мин**

КАК ИСПОЛЬЗОВАТЬ

Прием	4 стол + 2 диван + 2 складных
Сервировка	K04 и столешница 300
Музыка	колонки на PM, микрофоны W01
Важно	это не ужин на 6
После гостей	ступья в T01, путь свободен


ЧЕСТНЫЕ ОГРАНИЧЕНИЯ

- Варочная 450 и ПММ 450 - осознанный компромисс ради хранения и проходов.
- Диван 1300x600 компактный; 65-75 дюймов и проектор эта схема не поддерживает.
- Вода, вентиляция, E-01, петли D2/O1 и высота шкафов пока не замкнуты.


KLV-002 | КУХНЯ - МОДУЛИ И ВЫСОТЫ

Фасады - проектная схема. Ширины модулей фиксированы в концепте; высоты и инженерные оси не для заказа.

ФАСАД А - ВЕРХНИЙ ФРОНТ 2700 | М 1:20

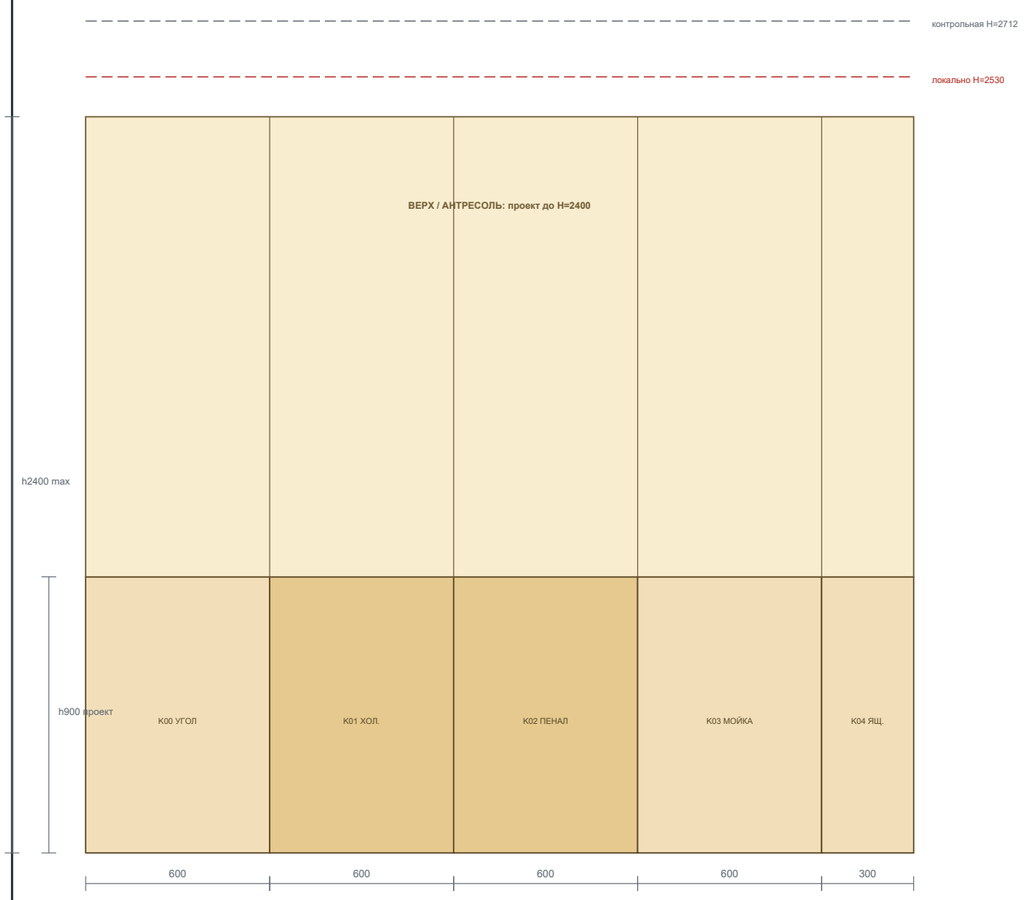

ФАСАД В - ВОЗВРАТ 1600 | М 1:20

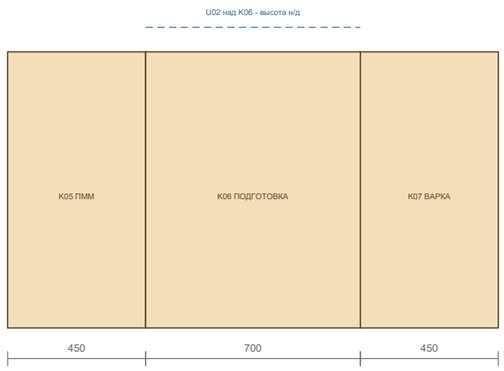

Непрерывная подготовка 700; варочная 450; ПММ 450.

МОДУЛЬНАЯ ВЕДОМОСТЬ

ID	Ширина	Функция	Статус
K00	600	угол, крупная посуда	проект
K01	600	холодильник	SKU н/д
K02	600	пенал, духовка, СВЧ	SKU н/д
K03	600	мойка + сортировка	вода н/д
K04	300	приборы / посадочная	проект
K05	450	посудомоечная	SKU н/д
K06	700	ящики + подготовка	проект
K07	450	3-зонная варка	вент. н/д
U01	900	верх над мойкой	H н/д
U02	700	верх подготовки	H н/д
T01	1200	верх над пеналами	H н/д

ПОЧЕМУ НЕ D+/E+

- 2200-2300 мм не вмещают отдельные мойку, ПММ, подготовку, варку и продуктовый пенал.
- Блок 'мойка+ПММ 600' из прошлых листов не является реальным модулем и исключен.
- Здесь 4300 мм фронтов, отдельные модули и 700 мм непрерывной подготовки.

KLV-002 | ВЕДОМОСТЬ ХРАНЕНИЯ

Полезный объем - расчетная внутренняя емкость с коэффициентом наполнения; холодильник и ПММ не считаются.

РАСЧЕТНАЯ ПОЛЕЗНАЯ ЕМКОСТЬ: 1593 Л = 1.59 М3 | ДОПУСК ±20 ПРОЦЕНТОВ

Если верхние шкафы U01/U02/T01 не проходят по вентиляции или высоте, емкость падает на 461 л до 1.13 м3.

ID	Элемент	Чистый конверт	k	Литры	Назначение	Доступ	Статус
K00	Угловая база	600x560x700	0.50	118	Кастрюли / формы	Неделя	Проект
K02	Пенал с духовкой	600x560x2100	0.40	282	Сухие продукты / техника	День+редко	Проект
K03	База мойки	600x520x700	0.25	55	Сортировка / расходники	День	Оси н/д
K04	Ящики 300	300x500x600	0.75	68	Приборы / доски	День	Проект
K06	Ящики подготовки	700x500x600	0.75	158	Посуда / контейнеры	День	Проект
K07	База под варкой	450x500x600	0.45	61	Сковороды / масла	День	Вент. н/д
U01	Верх над мойкой	900x300x900	0.75	182	Посуда / чай / кофе	День	Высота н/д
U02	Верх над подготовкой	700x300x900	0.75	142	Бакалея / специи	День	Высота н/д
T01	Антресоль над пеналами	1200x500x350	0.65	137	Редкая техника	Редко	Высота н/д
W01	Шкаф над РМ	1200x260x600	0.75	140	Документы / микрофоны	День	E-01 н/д
W02	Тумба РМ	400x500x600	0.70	84	Гарнитура / зарядки	День	Проект
M01	Медиа-тумба	1800x260x250	0.75	88	Кабели / приставки	День	Вентиляция
D01	Банкетка	850x350x300	0.70	62	Игры / текстиль	Неделя	Проект
F01	Pet-секция	350x250x250	0.75	16	Корм / салфетки	День	Защелка

ИТОГО БЕЗ ХОЛОДИЛЬНИКА И ПММ **1593 Л**

ЕЖЕДНЕВНО 400-1600

K03/K04/K06/K07/U01/W02/M01/F01: посуда, продукты, зарядки, корм.

РЕДКО / ВЫСОКО

K02/T01/U02: редкая техника и запасы. Нужна стремянка; ничего тяжелого над рабочим местом.


НЕ ХРАНИТЬ ЗДЕСЬ

Сезонное, крупная уборочная техника и архив детских вещей - гардеробная 8. Химия и лекарства - запираемый верх.

KLV-002 | СЦЕНАРИИ ОДНОВРЕМЕННОГО ИСПОЛЬЗОВАНИЯ


Мини-схемы повторяют те же координаты B01. Цветом выделены активные зоны; маршрут всегда остается пустым.

A. ГОТОВКА + РАБОТА

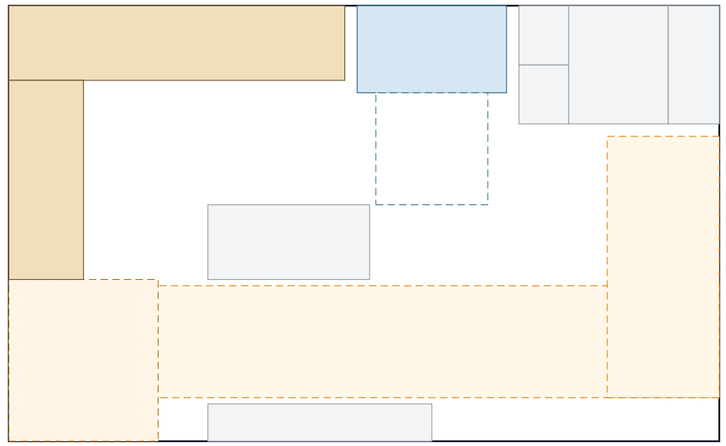


PASS: два кухонных прохода 1000; кресло 900 отдельно.

B. СЕМЕЙНЫЙ УЖИН 4

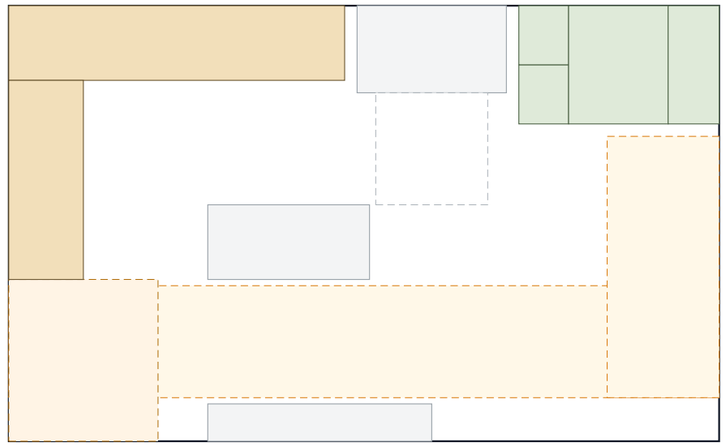


PASS: кухня и стол не пересекаются; O1 имеет резерв 100.

C. ГОСТИ / ОБЩЕНИЕ ДО 8

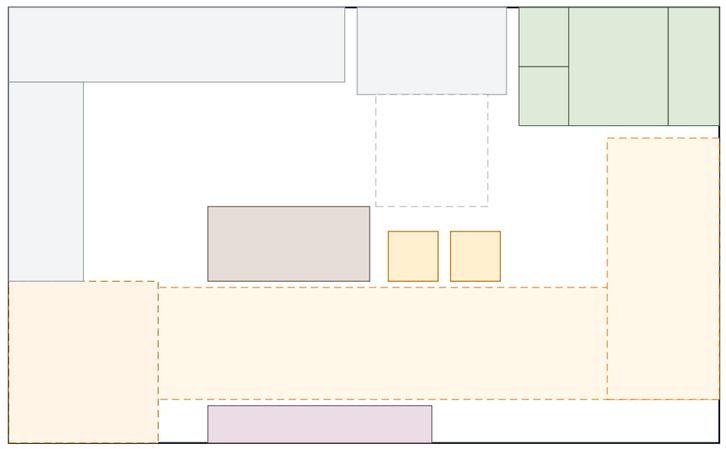

PASS: 4 стол + 2 диван + 2 складных; это не ужин 6.

D. УБОРКА + ПИТОМЦЫ

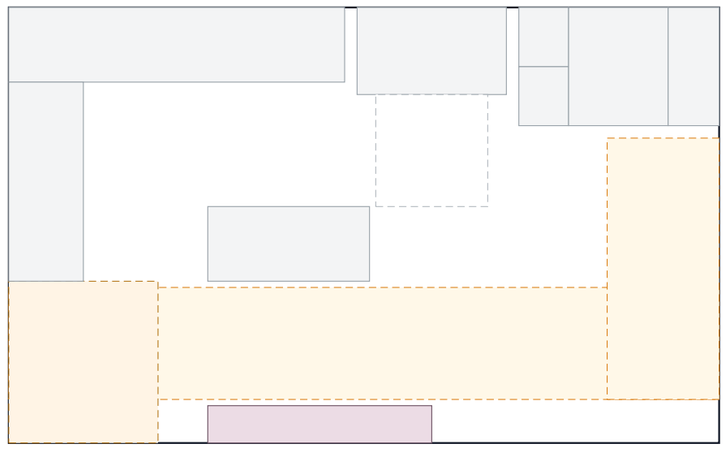

PASS: F01 у медиа; робот и пылесос остаются в гардеробной 8.

KLV-002 | ПРИЕМКА, РИСКИ И СЛЕДУЮЩИЕ ШАГИ

Этот лист отделяет проверенное от проектного и не дает использовать концепт как чертеж заказа.

ПРОВЕРЯЕМАЯ МАТРИЦА

B01 / D2 / O1	5710x3500; 915 контроль; O1 1600	**PASS**
Путь D2-O1	900 во всех показанных режимах	**PASS**
D2 guard	1200x1300; обе возможные дуги внутри	**PASS***
Кухонные проходы	1000 по верхнему и левому фронту	**PASS**
PM	1200x700; конверт кресла 900	**PASS**
ПММ / духовка / холодильник	динамика показана, мебель не пересекает	**PASS***
Семейный стол	950x800; 4 места компактно	**PASS**
Прием гостей	до 8 социальных мест	**PASS**
Ужин 6	без блокировки пути / кухни не помещается	**НЕ ЗАЯВЛЕН**
Хранение	1593 л ±20 процентов; без холодильника	**ПРОЕКТ**
TV	43-50; около 1200-1400 до глаз	**ПОДБОР SKU**
65-75 / проектор	требует другой медиа-компоновки	**FAIL ЗДЕСЬ**

ОТКРЫТЫЕ ВОРОТА ДО ЗАКАЗА

G1 - Вода / канализация

две оси, диаметры, h центра

G2 - Вентиляция / вытяжка

ось, сечение, маршрут воздуховода

G3 - E-01

две привязки и высота розеток

G4 - D2 и O1

петли, профиль, фактическая дуга

G5 - Потолок

граница локального H=2530 и все 5

точек

G6 - SKU

реальные габариты и открывание

техники/мебели

РЕШЕНИЕ: утвердить геометрию SF как базу только после G1-G5; затем подобрать SKU и повторить динамическую проверку G6.