
КУХНЯ-ГОСТИНАЯ | ВАРИАНТ А | М 1:25

B01 и проемы - фактические. Мебель и техника - проектные габаритные конверты до выбора SKU.

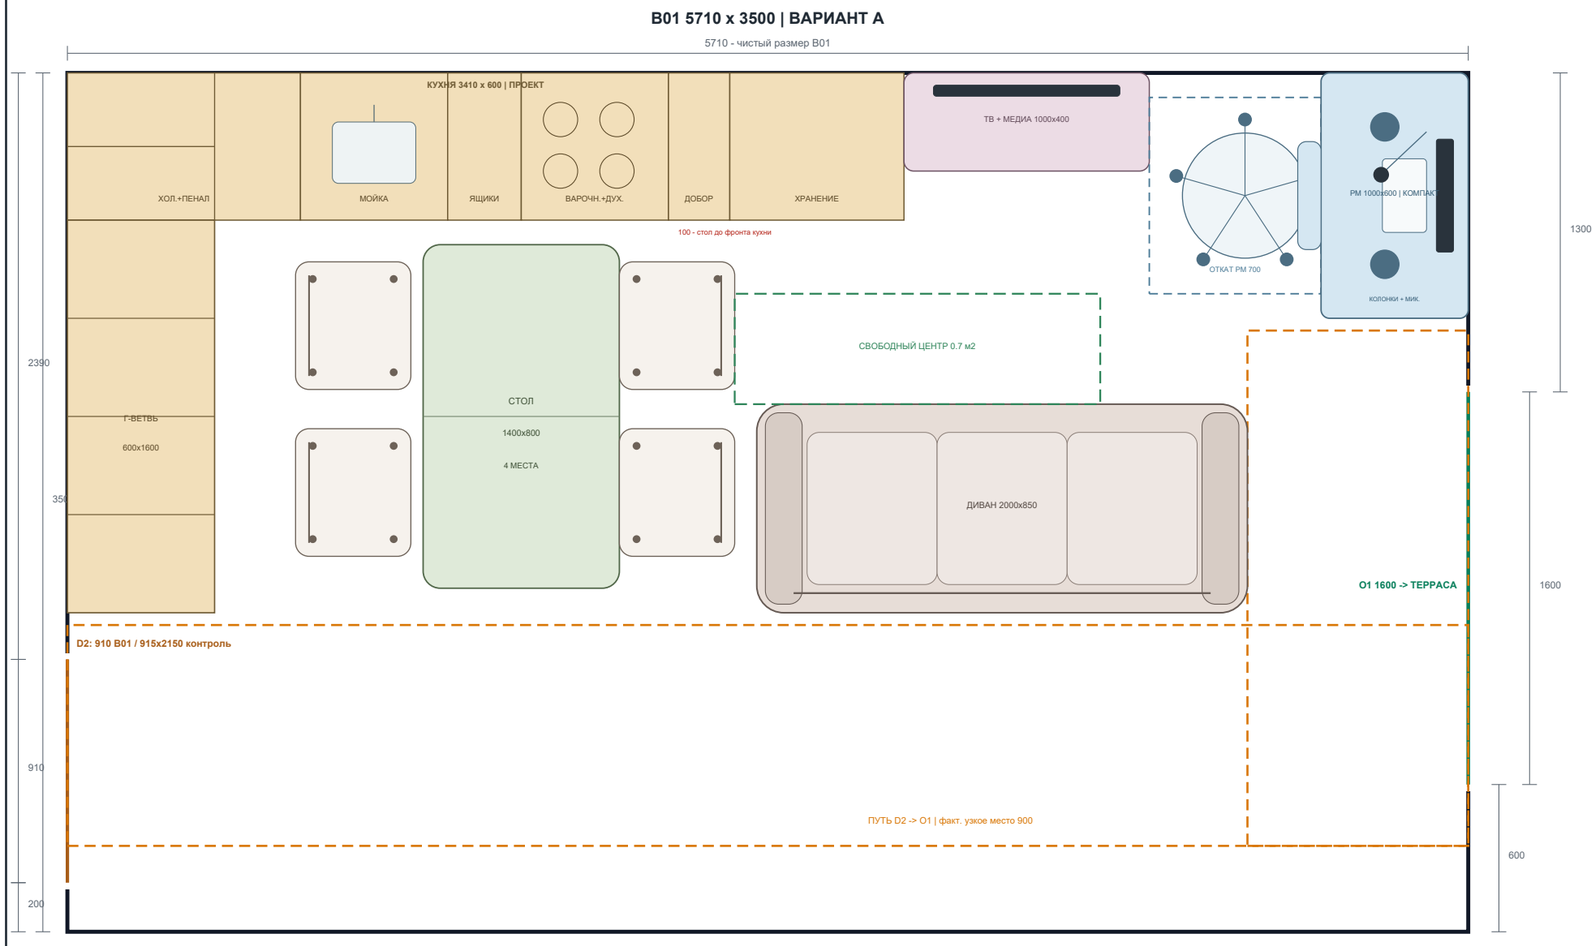

A - КЛАССИЧЕСКИЙ БАЛАНС

Г-кухня, обычный стол, диван лицом к ТВ,

компактное РМ у O1

2.3/5

ИЗМЕРИМАЯ ОЦЕНКА

Маршрут D2-O1	900	4
У кухни	100	1
За стулом	90	1
Откат РМ	700	2
Закр. хранение*	5010	5
Своб. прямоуг.*	0.7 м2	1
Ребёнок/питомцы*	2 рег.	2

ПЛЮСЫ

+ Полноценный стол на 4

+ Максимум кухонного хранения

+ Прямой обзор ТВ

КОМПРОМИССЫ

- РМ только 1000x600

- 100 мм у рабочего фронта

- 90 мм и 2 тесные зоны для ребёнка/питомцев

1000 мм = 40 мм на листе

ФАКТ: B01 5710x3500; D2 200+910 (контроль 915x2150); O1 600+1600+1300.

РЕКОМЕНДАЦИИ NKBA, не нормы РБ: проход 914; рабочий проход 1067 для одного; за стулом без транзита 813.

ПРОЕКТ*: откат РМ 900; хранение = кухня + закрытая сторона полуострова/банкетки; свободный прямоугольник считается выше маршрута.

ОЦЕНКА: проходы 5=ориентир; 4=до 50 ниже; 3=51-150; 2=151-250; 1=>250. Хранение: 5>=4000; 4>=3400; 3>=2800; 2>=2200; 1<2200.

СВОБ. ЗОНА*: 5>=4.0; 4>=3.0; 3>=2.2; 2>=1.5; 1<1.5 м2 непрерывного незанятого пола выше маршрута.


СЕМЬЯ*: 5=нет конфликтов; 4=один редкий; 3=один регулярный; 2=два; 1=три и более либо блокировка маршрута ребёнком/питомцем.

КОНТРОЛЬ: вода, E-01, радиаторы и конкретные модели мебели/техники требуют привязки до рабочей документации.

КУХНЯ-ГОСТИНАЯ | ВАРИАНТ B | М 1:25

B01 и проемы - фактические. Мебель и техника - проектные габаритные конверты до выбора SKU.

B01 5710 x 3500 | ВАРИАНТ B

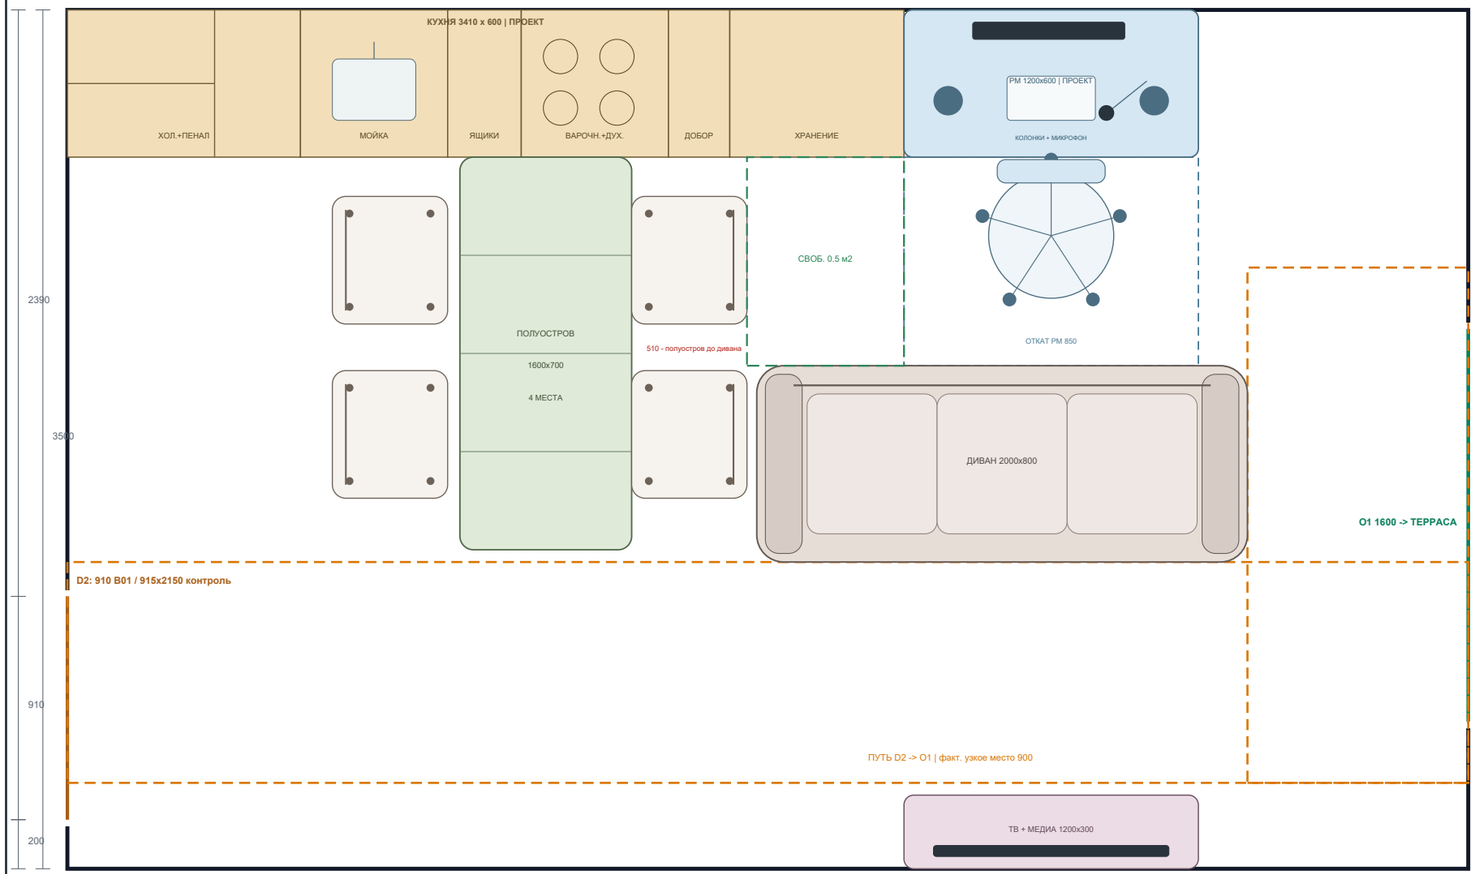

1000 мм = 40 мм на листе

B - КУХНЯ С ПОЛУОСТРОВОМ

Прямая кухня, РМ в верхней линии, полуостров для еды и хранения

2.6/5

ИЗМЕРИМАЯ ОЦЕНКА

Маршрут D2-O1	900	4
У полуострова	510	1
За стулом	40	1
Откат РМ	850	4
Закр. хранение*	5010	5
Своб. прямоуг.*	0.5 м2	1
Ребёнок/питомцы*	2 рег.	2

ПЛЮСЫ

+ Больше столешницы
+ Четыре посадочных места
+ РМ шириной 1200

КОМПРОМИССЫ

- 40 мм за правыми стульями
- Стулья конфликтуют с путём ребёнка/питомцев
- Узкий боковой проход 510

ФАКТ: B01 5710x3500; D2 200+910 (контроль 915x2150); O1 600+1600+1300.

РЕКОМЕНДАЦИИ NKBA, не нормы РБ: проход 914; рабочий проход 1067 для одного; за стулом без транзита 813.

ПРОЕКТ*: откат РМ 900; хранение = кухня + закрытая сторона полуострова/банкетки; свободный прямоугольник считается выше маршрута.

ОЦЕНКА: проходы 5=ориентир; 4=до 50 ниже; 3=51-150; 2=151-250; 1=>250. Хранение: 5>=4000; 4>=3400; 3>=2800; 2>=2200; 1<2200.


СВОБ. ЗОНА*: 5>=4.0; 4>=3.0; 3>=2.2; 2>=1.5; 1<1.5 м2 непрерывного незанятого пола выше маршрута.

СЕМЬЯ*: 5=нет конфликтов; 4=один редкий; 3=один регулярный; 2=два; 1=три и более либо блокировка маршрута ребёнком/питомцем.

КОНТРОЛЬ: вода, E-01, радиаторы и конкретные модели мебели/техники требуют привязки до рабочей документации.

КУХНЯ-ГОСТИНАЯ | ВАРИАНТ C | М 1:25

B01 и проемы - фактические. Мебель и техника - проектные габаритные конверты до выбора SKU.

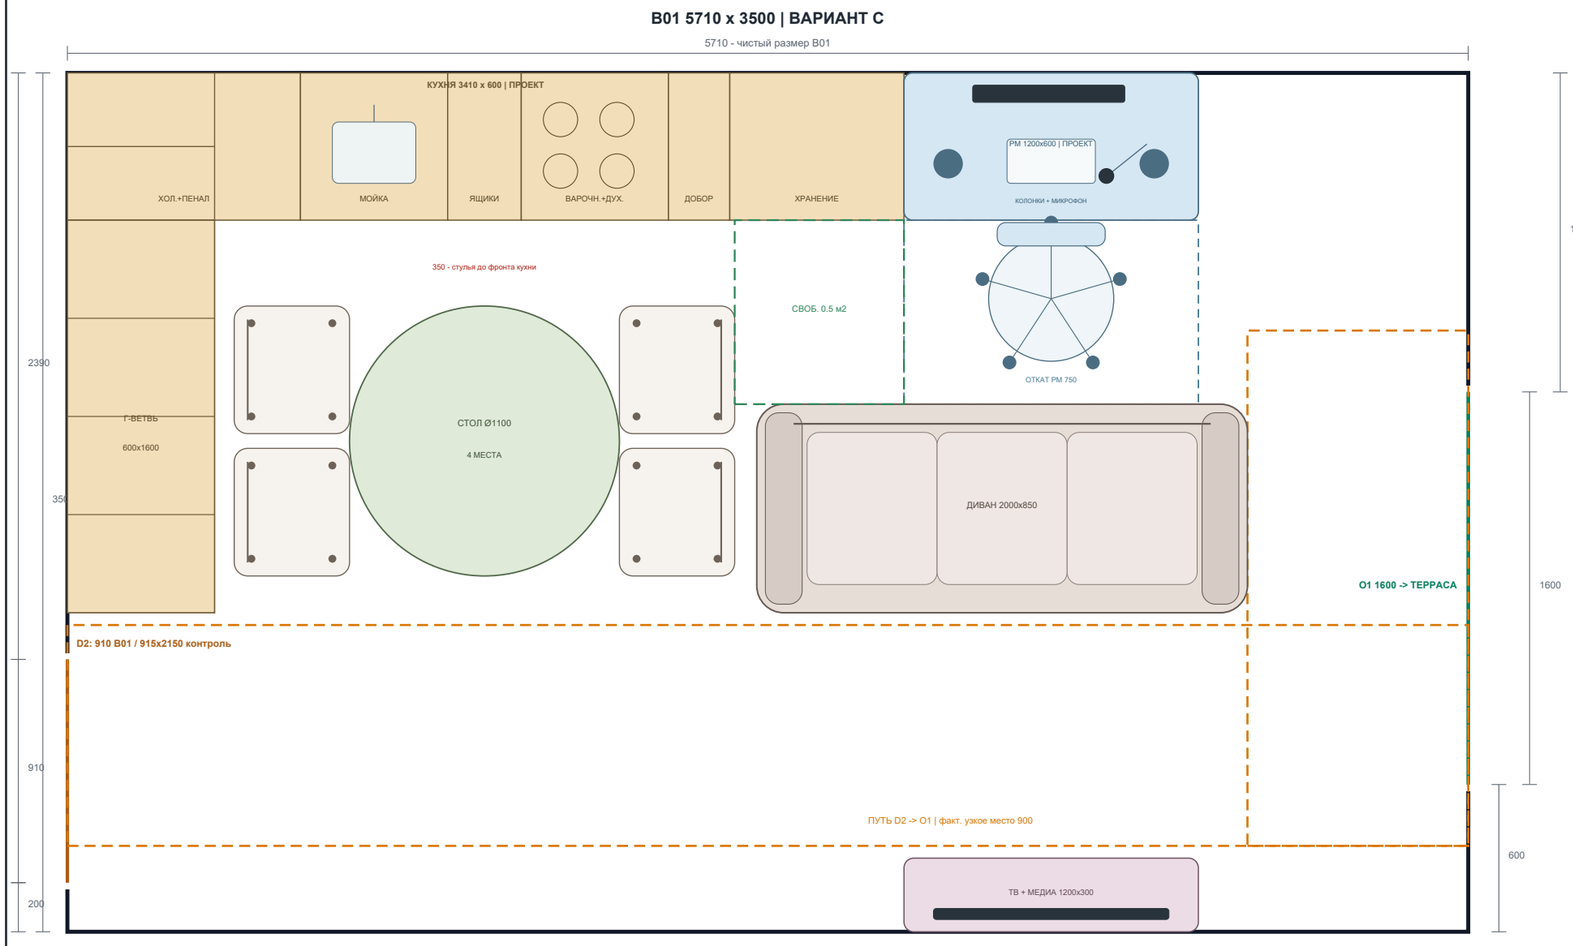

C - КРУГЛЫЙ СТОЛ + ВСТРОЕННОЕ РМ

Г-кухня, круглый стол, РМ в общей верхней линии, диван-зонирование

2.3/5

ИЗМЕРИМАЯ ОЦЕНКА

Маршрут D2-O1	900	4
У кухни	350	1
За стулом	90	1
Откат РМ	750	3
Закр. хранение*	5010	5
Своб. прямоуг.*	0.5 м2	1
Ребёнок/питомцы*	3 рег.	1

ПЛЮСЫ

+ Мягкая круглая геометрия

+ РМ 1200x600

+ Удобное общение за столом

КОМПРОМИССЫ

- 350 мм у рабочего фронта

- 90 мм у дивана; 3 тесные зоны для ребёнка/питомцев

- Откат кресла только 750

1000 мм = 40 мм на листе

ФАКТ: B01 5710x3500; D2 200+910 (контроль 915x2150); O1 600+1600+1300.

РЕКОМЕНДАЦИИ NKBA, не нормы РБ: проход 914; рабочий проход 1067 для одного; за стулом без транзита 813.

ПРОЕКТ*: откат РМ 900; хранение = кухня + закрытая сторона полуострова/банкетки; свободный прямоугольник считается выше маршрута.

ОЦЕНКА: проходы 5=ориентир; 4=до 50 ниже; 3=51-150; 2=151-250; 1=>250. Хранение: 5>=4000; 4>=3400; 3>=2800; 2>=2200; 1<2200.


СВОБ. ЗОНА*: 5>=4.0; 4>=3.0; 3>=2.2; 2>=1.5; 1<1.5 м2 непрерывного незанятого пола выше маршрута.

СЕМЬЯ*: 5=нет конфликтов; 4=один редкий; 3=один регулярный; 2=два; 1=три и более либо блокировка маршрута ребёнком/питомцем.

КОНТРОЛЬ: вода, E-01, радиаторы и конкретные модели мебели/техники требуют привязки до рабочей документации.

КУХНЯ-ГОСТИНАЯ | ВАРИАНТ D | М 1:25

B01 и проемы - фактические. Мебель и техника - проектные габаритные конверты до выбора SKU.

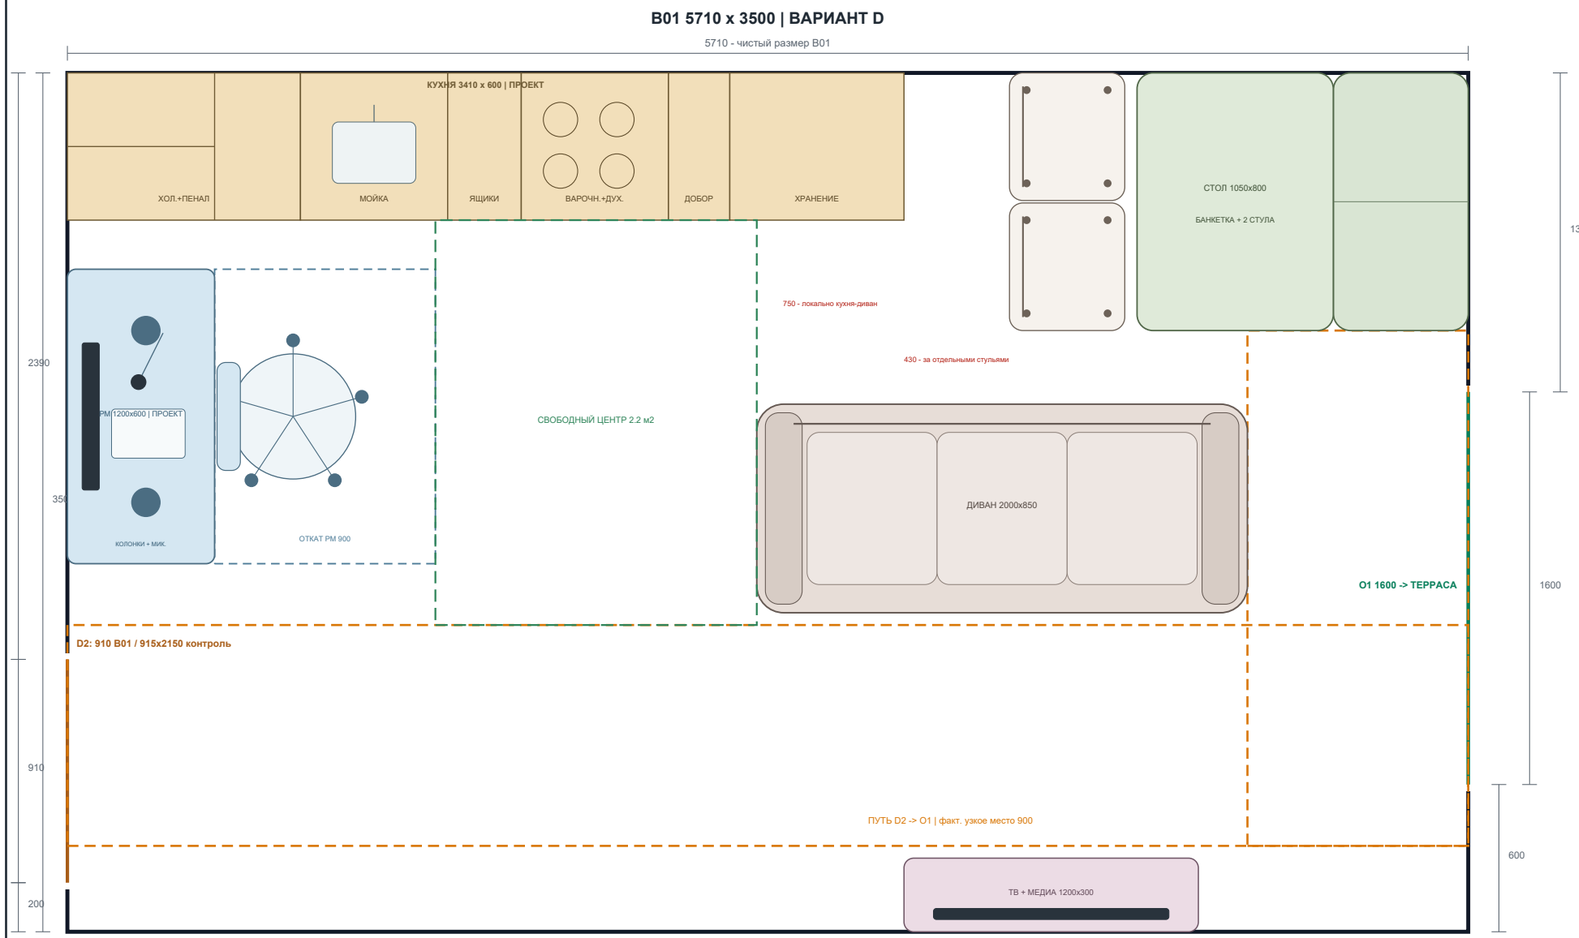

1000 мм = 40 мм на листе

D - СЕМЕЙНАЯ БАНКЕТКА

Прямая кухня, РМ слева, банкетка у верхнего простенка O1, свободный центр

3.3/5
РЕКОМЕНДУЮ

ИЗМЕРИМАЯ ОЦЕНКА

Маршрут D2-O1	900	4
Кухня-диван	750	1
За стулом	430	1
Откат РМ	900	5
Закр. хранение*	4460	5
Своб. прямоуг.*	2.2 м2	3
Ребёнок/питомцы*	1 редк.	4

ПЛЮСЫ

+ Свободный центр для ребёнка/питомцев

+ РМ 1200x600 вне маршрута

+ Детям удобно на банкетке

КОМПРОМИССЫ

- Локально кухня-диван 750

- 430 мм за отдельными стульями

- Банкетка только на заказ

ФАКТ: B01 5710x3500; D2 200+910 (контроль 915x2150); O1 600+1600+1300.

РЕКОМЕНДАЦИИ NKBA, не нормы РБ: проход 914; рабочий проход 1067 для одного; за стулом без транзита 813.

ПРОЕКТ*: откат РМ 900; хранение = кухня + закрытая сторона полуострова/банкетки; свободный прямоугольник считается выше маршрута.

ОЦЕНКА: проходы 5=ориентир; 4=до 50 ниже; 3=51-150; 2=151-250; 1=>250. Хранение: 5>=4000; 4>=3400; 3>=2800; 2>=2200; 1<2200.

СВОБ. ЗОНА*: 5>=4.0; 4>=3.0; 3>=2.2; 2>=1.5; 1<1.5 м2 непрерывного незанятого пола выше маршрута.


СЕМЬЯ*: 5=нет конфликтов; 4=один редкий; 3=один регулярный; 2=два; 1=три и более либо блокировка маршрута ребёнком/питомцем.

КОНТРОЛЬ: вода, E-01, радиаторы и конкретные модели мебели/техники требуют привязки до рабочей документации.

КУХНЯ-ГОСТИНАЯ | ВАРИАНТ E | E1 - ЕЖЕДНЕВНО | M 1:25

B01 и проёмы - фактические. Мебель - проектные габариты. Стены и проёмы не меняются.

B01 5710 x 3500 | ВАРИАНТ E1 - ЕЖЕДНЕВНО

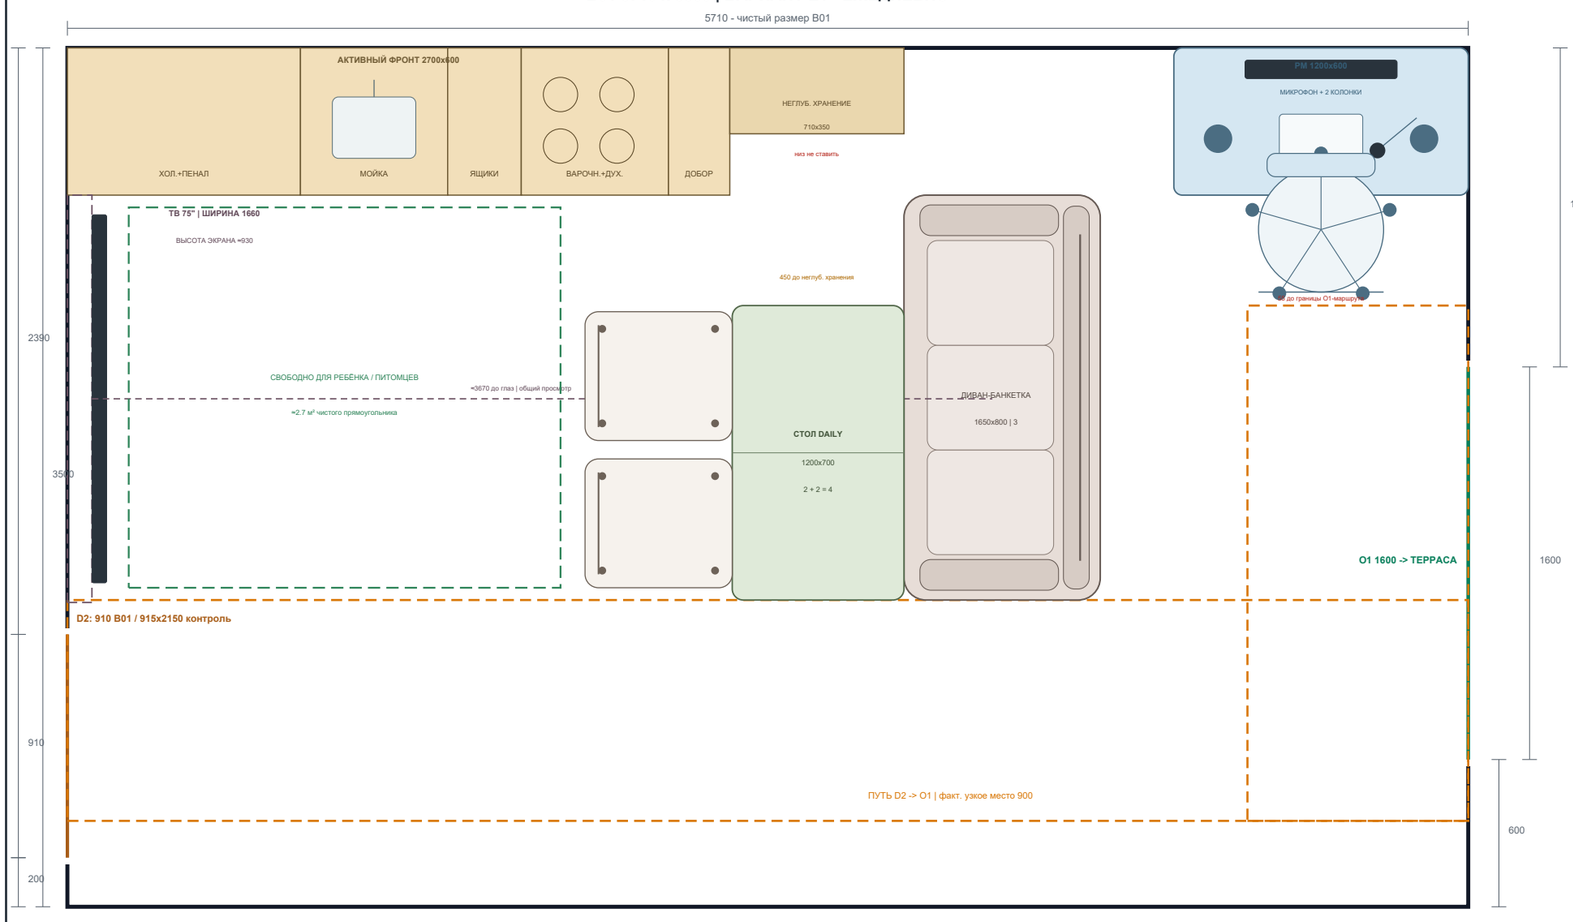

1000 мм = 40 мм на листе

ФАКТ: B01 5710x3500; D2 слева 200+910 (контроль 915x2150); О1 справа 600+1600+1300.

ПУТЬ: защищённая проектная полоса 900 мм сохранена; это не заявление о соответствии нормам РБ.

E: активная кухня 2700x600; хранение 710x350; стол 1200->1650x700; диван 1650x800; РМ 1200x600.

ГОСТИ: 6 посадок = 3 на прямом диване + 3 на стульях; 550 мм на человека - допустимо лишь эпизодически.

ТВ: панель 75" приблизительно 1660x930; дистанция до глаз около 3670; проектор требует отдельного расчёта.

ГЕЙТЫ: сторона D2, наличники, вода, вентиляция, E-01, отопление и реальные SKU должны быть промерены до заказа.

РМ: кресло в рабочем положении не входит в О1-маршрут (запас 55); при откате назад пересечение временно возможно.

E1 - ЕЖЕДНЕВНЫЙ РЕЖИМ

Стол	**1200x700, 4 места**
Диван	**1650x800, прямой**
ТВ	**75", ось ≈3670**
Рабочее место	**1200x600**
Путь D2-О1	**900, свободен**
Свободный центр	**≈2.7 м²**

ПОЧЕМУ ЭТО СИЛЬНЕЕ D

+ ТВ развёрнут по длинной оси комнаты

+ Один стол обслуживает 4 и 6 человек

+ Диван работает и как мягкая банкетка

+ Не перекрываются D2, О1 и путь 900

ЧЕСТНЫЕ КОМПРОМИССЫ

- Нужен прямой диван с посадкой 430-470

- 6 мест - редкий компактный режим


- Выдвижение кресла РМ временно касается пути

- Крепление ТВ - только после проверки D2

КУХНЯ-ГОСТИНАЯ | ВАРИАНТ E | E2 - ГОСТИ | M 1:25

B01 и проёмы - фактические. Мебель - проектные габариты. Стены и проёмы не меняются.

B01 5710 x 3500 | ВАРИАНТ E2 - ГОСТИ

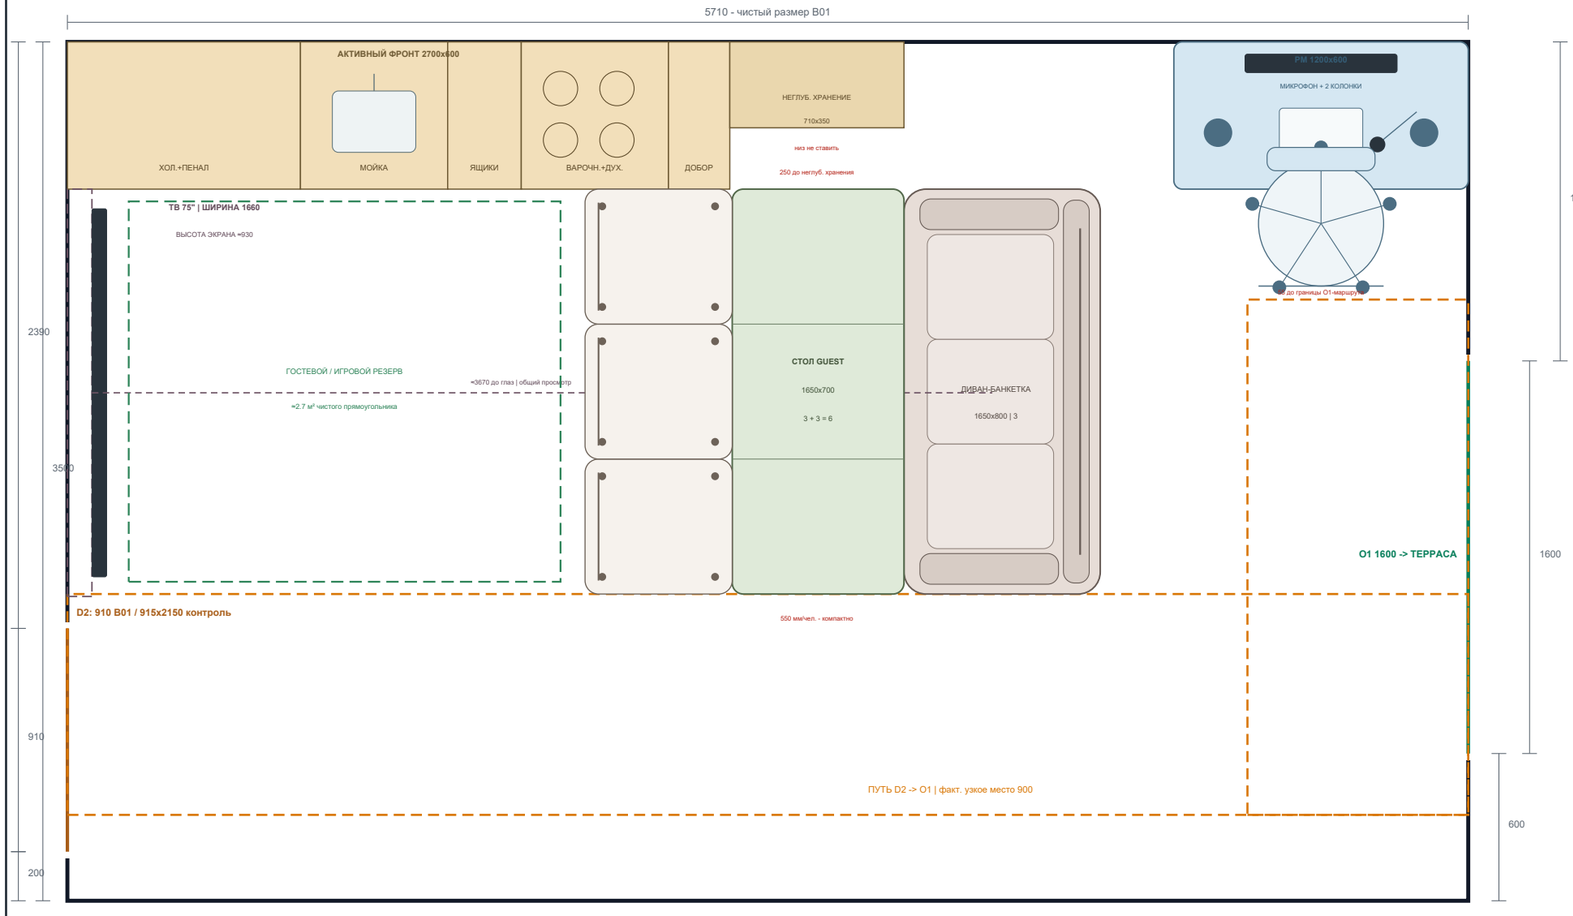

E2 - ГОСТЕВОЙ РЕЖИМ

Стол	**1650x700**
Посадка	**3 диван + 3 стула**
Ширина на гостя	**550 - компактно**
Путь D2-O1	**900, свободен**
Рабочее место	**остаётся на месте**
Кухня	**активные 2700 доступны**

ПОЧЕМУ ЭТО СИЛЬНЕЕ D

+ ТВ развёрнут по длинной оси комнаты

+ Один стол обслуживает 4 и 6 человек

+ Диван работает и как мягкая банкетка

+ Не перекрываются D2, O1 и путь 900

ЧЕСТНЫЕ КОМПРОМИССЫ

- Нужен прямой диван с посадкой 430-470

- 6 мест - редкий компактный режим

- Выдвижение кресла РМ временно касается пути

- Крепление ТВ - только после проверки D2

1000 мм = 40 мм на листе

ФАКТ: B01 5710x3500; D2 слева 200+910 (контроль 915x2150); O1 справа 600+1600+1300.

ПУТЬ: защищённая проектная полоса 900 мм сохранена; это не заявление о соответствии нормам РБ.

E: активная кухня 2700x600; хранение 710x350; стол 1200->1650x700; диван 1650x800; РМ 1200x600.

ГОСТИ: 6 посадок = 3 на прямом диване + 3 на стульях; 550 мм на человека - допустимо лишь эпизодически.

ТВ: панель 75" приблизительно 1660x930; дистанция до глаз около 3670; проектор требует отдельного расчёта.

ГЕЙТЫ: сторона D2, наличники, вода, вентиляция, E-01, отопление и реальные SKU должны быть померены до заказа.

РМ: кресло в рабочем положении не входит в O1-маршрут (запас 55); при откате назад пересечение временно возможно.