
ПЛАН РАССТАНОВКИ - ПРАЧЕЧНАЯ

B01 1730 × 1740 мм | постоянная мебель только слева от входа | М 1:20

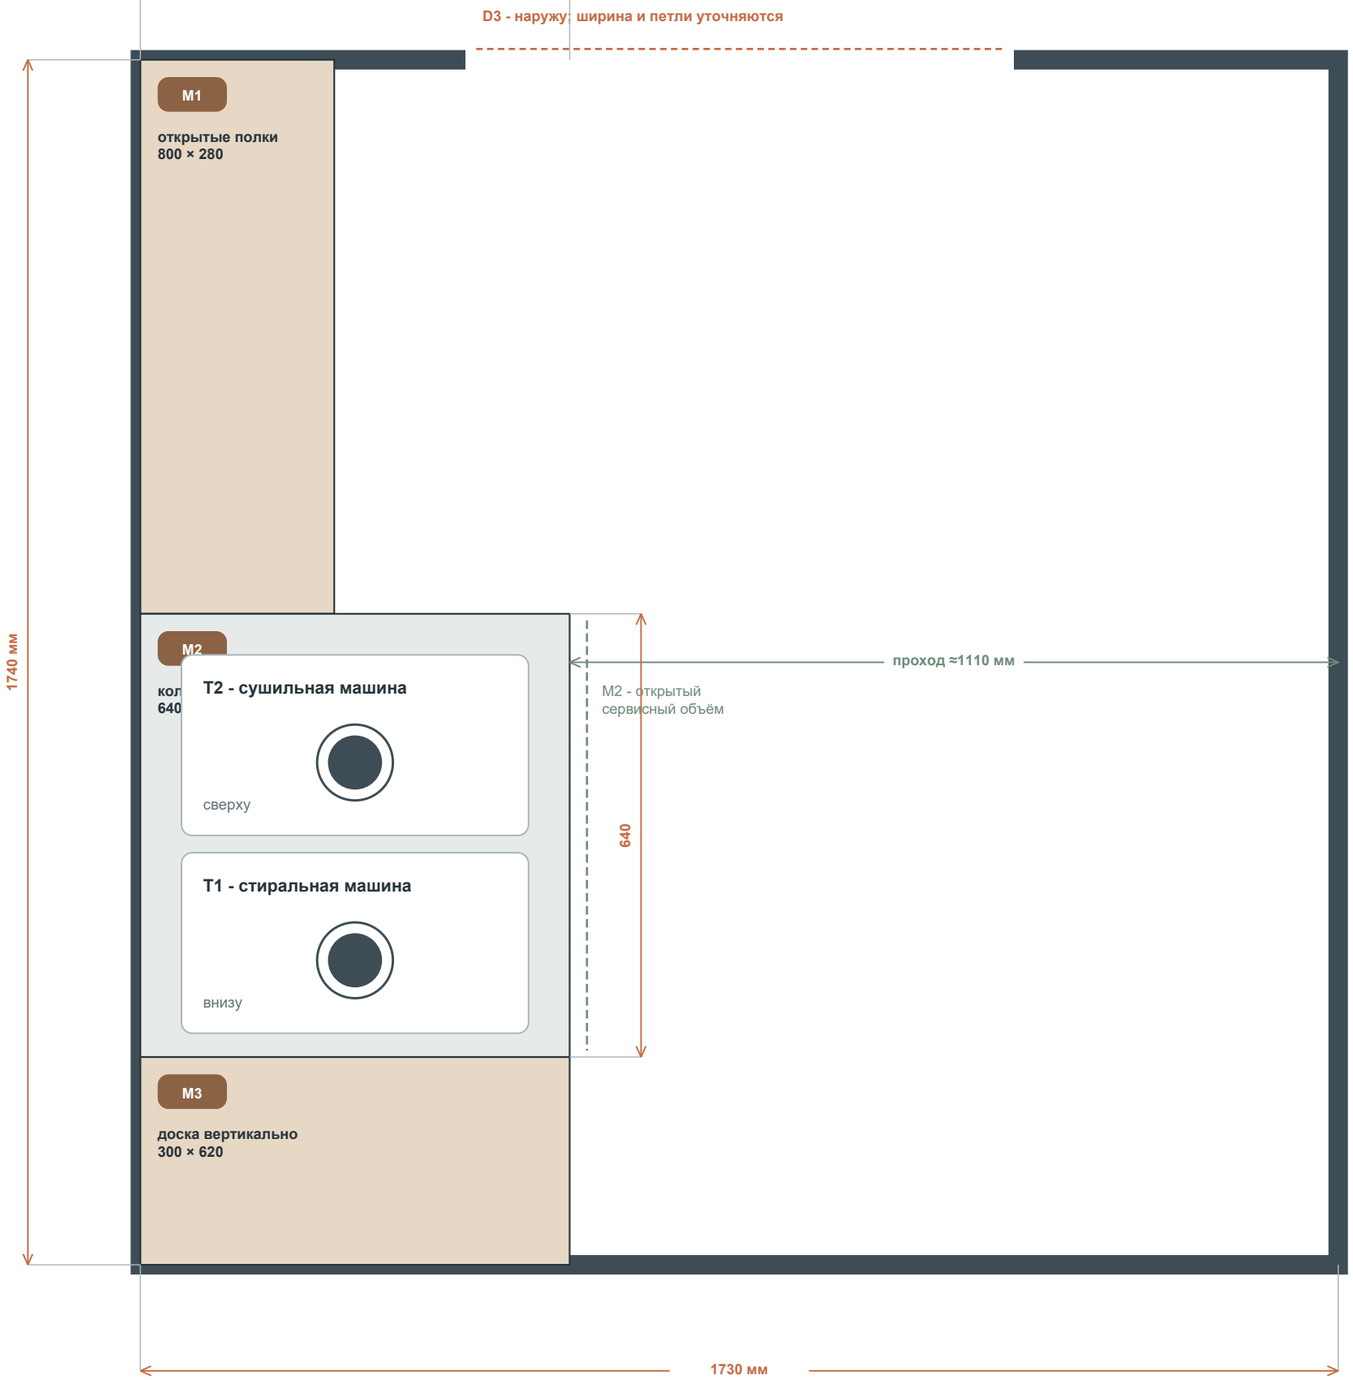

ЛОГИКА ПЛАНА

01 M1 + M2 + M3 = 1740 мм. Линия полностью занимает левую стену.

02 Справа нет постоянных модулей: это свободный проход и зона работы с доской.


03 Инженерные точки прачечной не подтверждены. Не назначать по ним приборы без отдельного обмера.

УСЛОВИЕ D3

Дверь открывается наружу. Сторона петель и чистый проём не выдумываются - фиксируются на натуре до заказа мебели.

РАЗВЁРТКА ЛЕВОЙ СТЕНЫ

Мебельная последовательность от входа к дальней стене | вертикальные высоты - только после обмера потолка

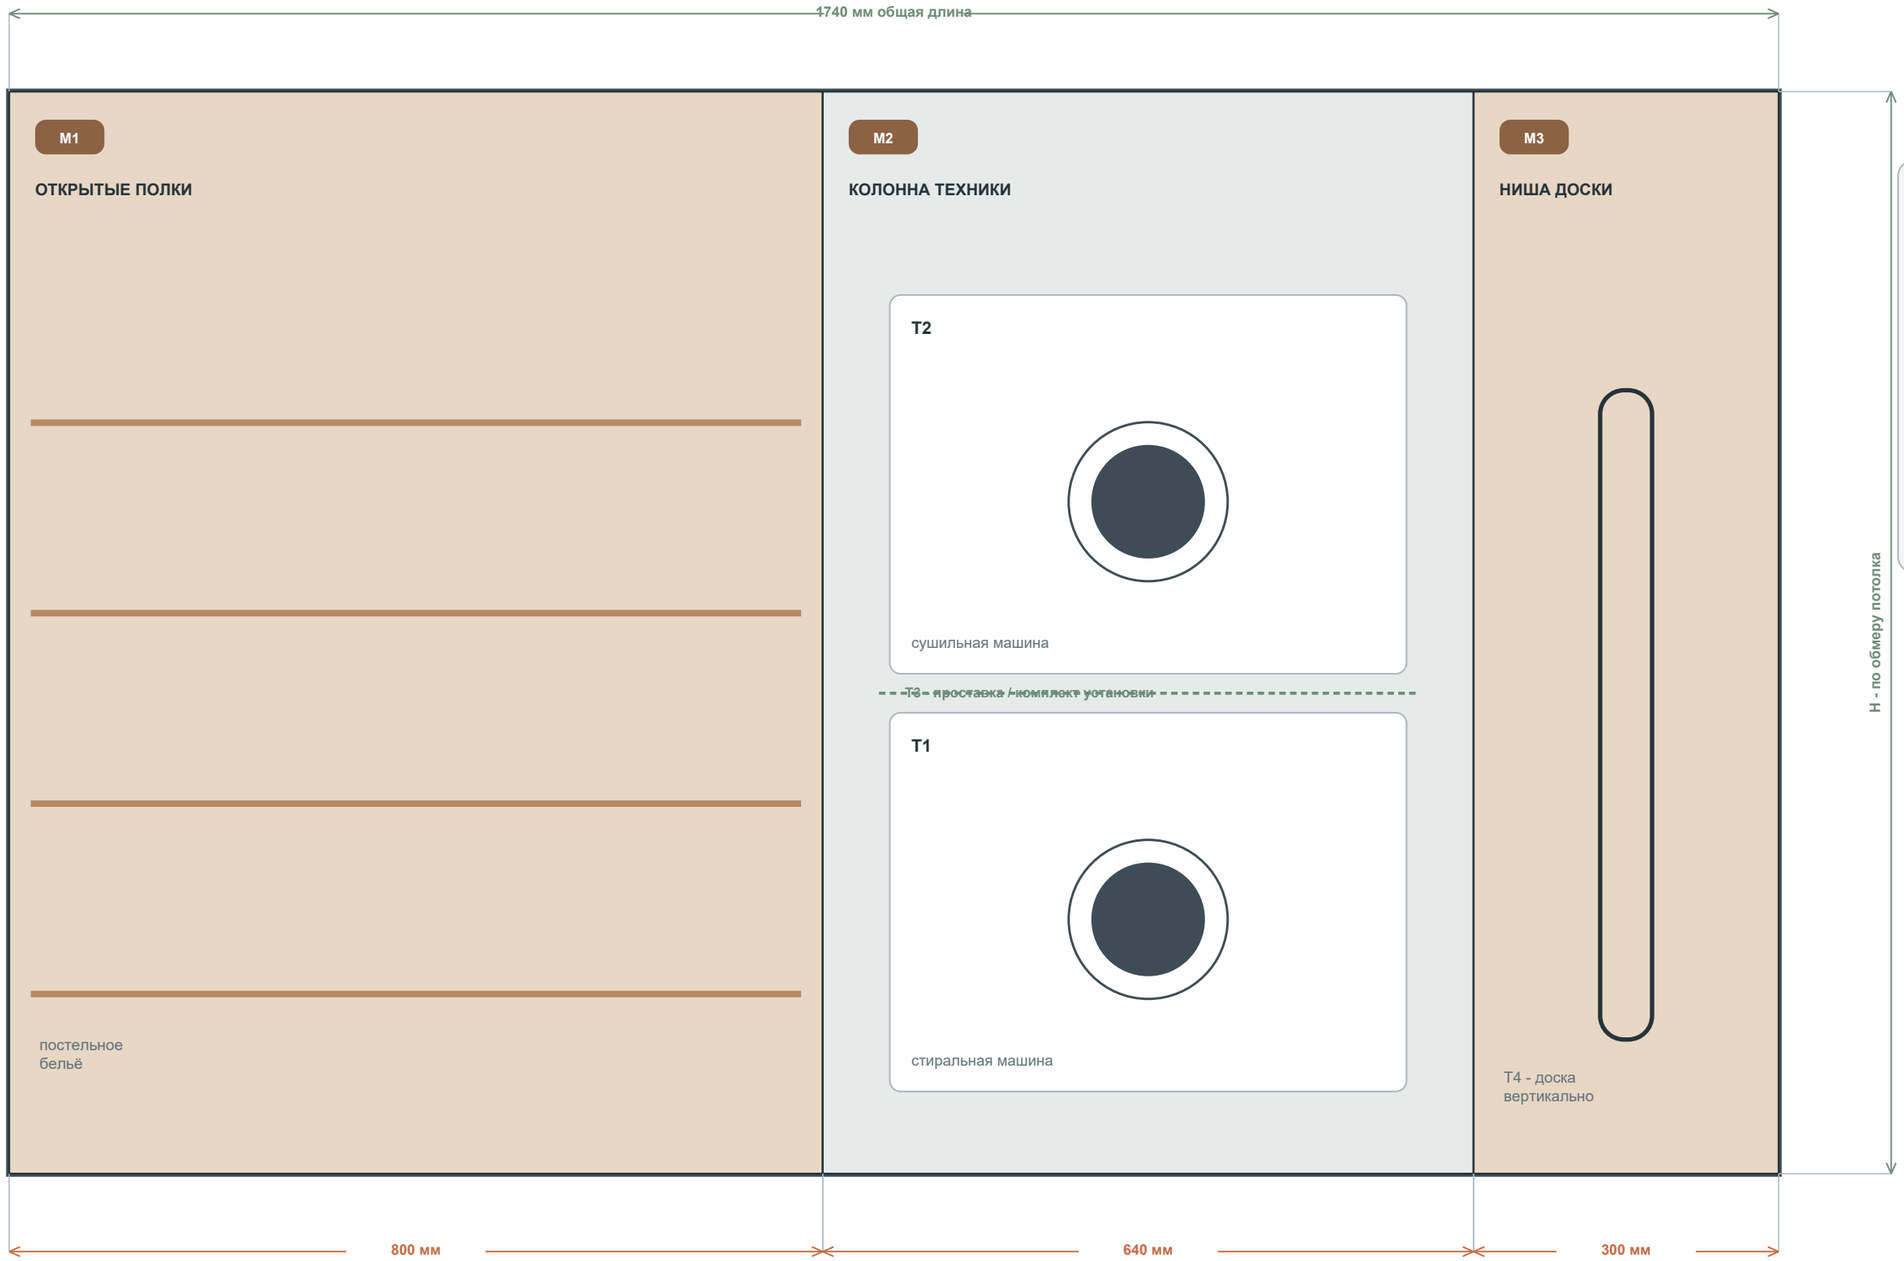

НЕ ВЫДУМЫВАТЬ

- высоту потолка;
- стороны петель D3;
- оси воды / слива;
- крепление к пустой стене.

В M2 не делать глухую заднюю стенку. Доступ к шлангам, розеткам и фильтрам сохраняется.


ТРИ РЕЖИМА И БЕЗОПАСНЫЙ ПРОХОД

Открытая мебель позволяет переключать сценарии без перестановки техники

01

СТИРКА


T1/T2 работают в открытой M2. Перед фасадами остаётся свободное место для загрузки и обслуживания.

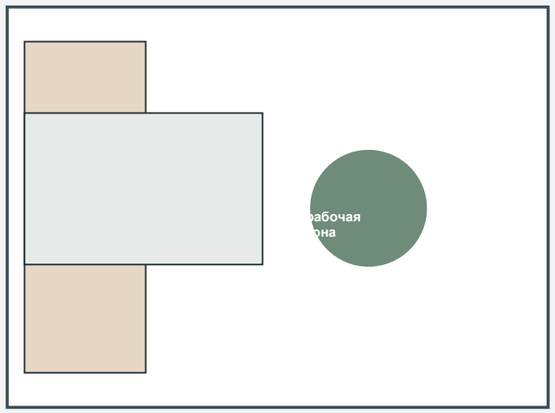

02

СКЛАДЫВАНИЕ


F1 - опциональная откидная поверхность 700 × 500 мм у M1. Она не заменяет гладильную доску.

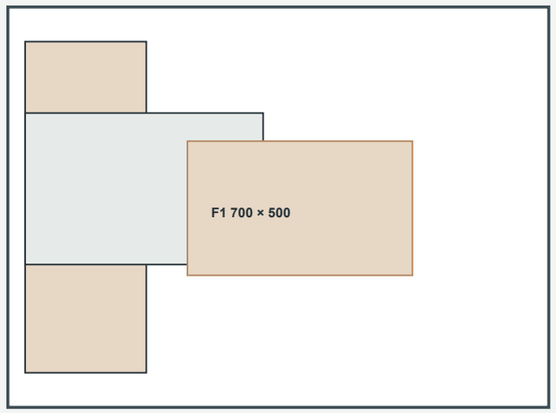

03

ГЛАЖКА

Доска выходит из M3 и раскрывается вдоль свободной части комнаты. Правую стену не занимать.

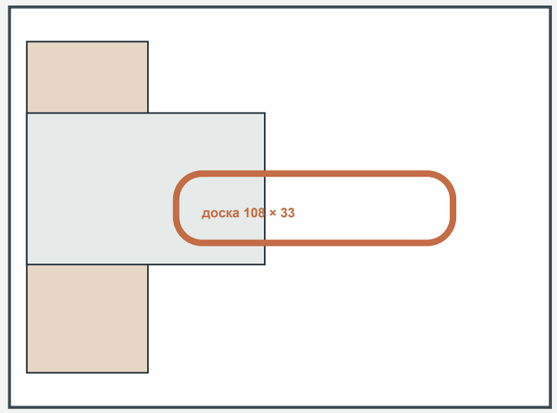

КОНТРОЛЬ: макет F1 и разложенной доски делается малярной лентой на полу до заказа мебели. D3 в этот момент проверяется в наружном открывании.

ХРАНЕНИЕ И ВЫДВИЖНАЯ РАБОЧАЯ ПОВЕРХНОСТЬ

Главная задача комнаты - стирать, сушить, складывать и хранить бельё без захламления прохода

M1

A1 · часто используемые полотенца и расходники

B1 · 2 кассеты для мелочей / химии

C1 · 3 мягких сортировочных мешка

D1 · постельное бельё в 4 коробках 360 × 260 × 250

E1 · запасные комплекты и сезонное

F1 - ОТКИДНАЯ ПОВЕРХНОСТЬ

Рекомендуемый стартовый размер 700 × 500 мм, высота 880-900 мм. Сначала проверить макетом, затем заказать фурнитуру.



не использовать как гладильную поверхность

СТОП Если макет F1 или доски съедает проход - уменьшить F1 до 600 × 400 мм, а не добавлять мебель справа.

ТЕХНИКА И МОНТАЖНЫЙ ОБЪЁМ М2

Выбор сделан под покупку в Китае; до оплаты сверить шильдик, точную модификацию, глубину с коммуникациями и гарантию

М2 · 640 × 620 мм

T2 - Haier HD80-D357U1-S



сушильная машина

T3 - HASTKU10 / подтверждённый комплект установки

T1 - Haier HW100-BD14979U1



стиральная машина

T1 — **Haier HW100-BD14979U1**

снизу; фронтальная загрузка; паспорт продавца обязателен

T2 — **Haier HD80-D357U1-S**

сверху; только с подходящим комплектом установки

T3 — **HASTKU10**

между приборами; проверить совместимость именно с обеими моделями


T4 — **RUTER 404.716.11**

доска; хранение в М3 вертикально; рабочая поверхность 108 × 33

ПРАВИЛО М2 остаётся открытой технической нишей: не зашивать заднюю стенку, не прятать розетки и не фиксировать зазоры без паспортов реальных приборов.

СВЕТ, ВЕНТИЛЯЦИЯ И ЭЛЕКТРИКА

Показана проектная логика; точные оси назначаются по натуре профильными специалистами

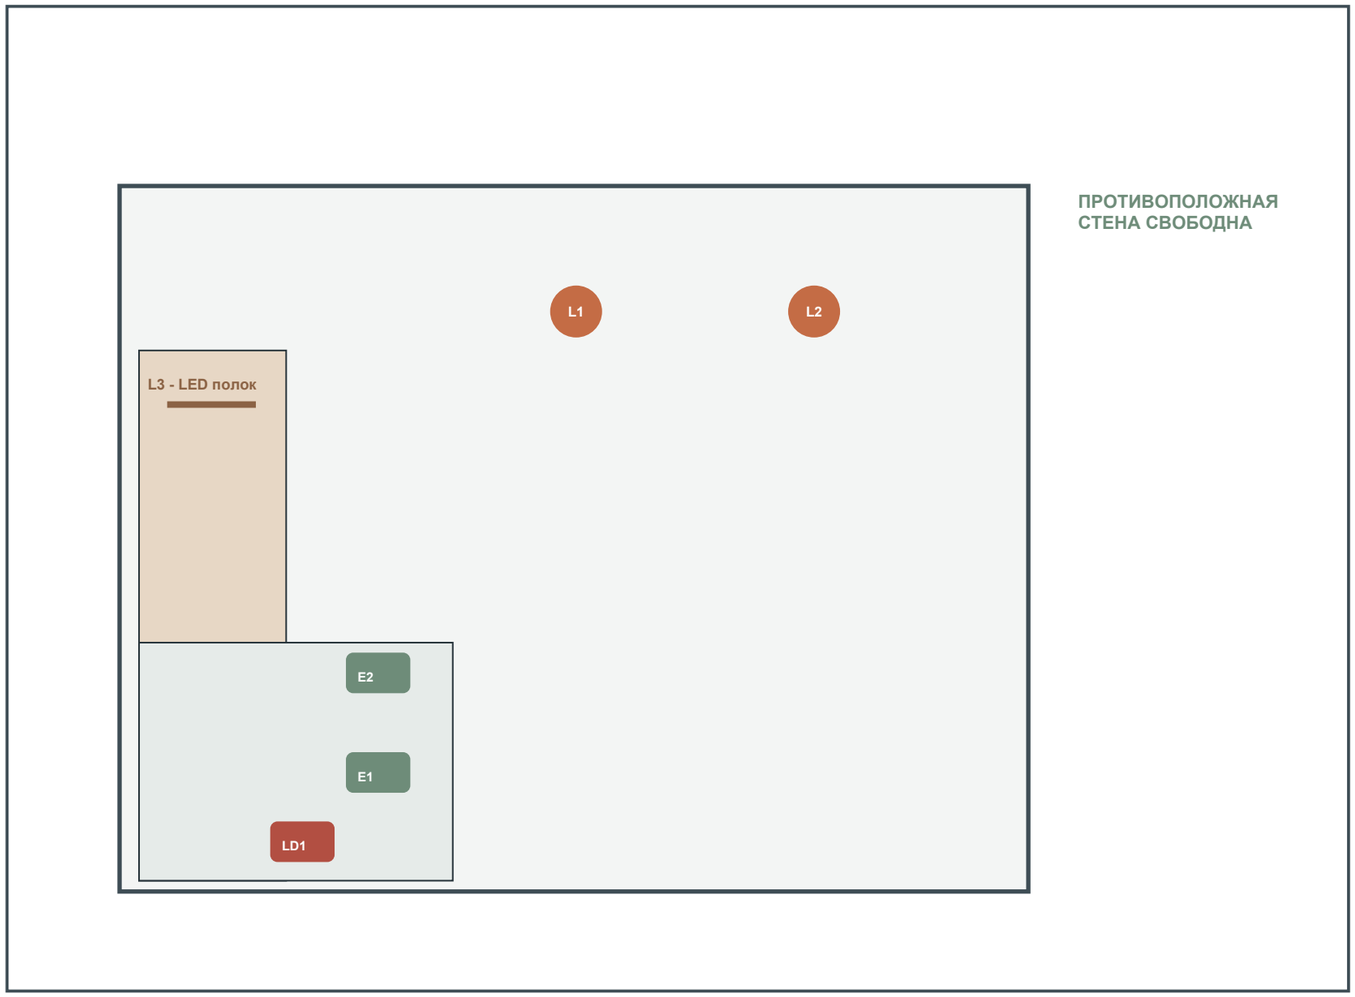

L1/L2 два потолочных контура; нейтральный тёплый свет

L3 отдельная LED-подсветка открытых полок

V1 проверить фактическую вытяжку и переток воздуха через дверь

E1/E2 доступные заземлённые розетки без удлинителей и тройников

LD1 датчик протечки под стиральной машиной; тест перед сдачей

ОГРАНИЧЕНИЕ ИСХОДНЫХ ДАННЫХ: никаких осей воды, слива или отопительных приборов в прачечной сейчас не принимать как факт. Сначала отдельный обмер этой комнаты.

КОНСТРУКТИВ МЕБЕЛИ И СЕРВИСНЫЙ ДОСТУП

Эта мебель хранит вещи; она не должна нести вес техники или перекрывать обслуживание

M1

Открытые полки

Корпус 18 мм: влагостойкая ЛДСП P3 или берёзовая фанера с HPL. Все торцы герметизировать.




открытая конструкция
без дверей

M2

Техническая колонна

Жёсткий ровный пол под техникой. Задняя стенка отсутствует; трассы, розетки и фильтры доступны.

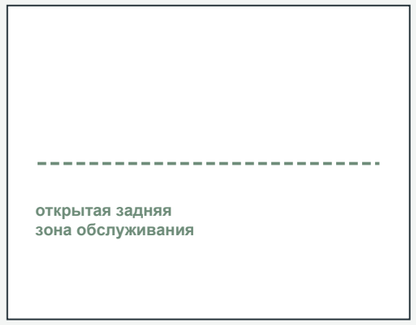

M3

Ниша доски

Чистая высота - не менее 1450 мм. Упор/ремень фиксирует доску вертикально, без падения.



вертикальная фиксация
и свободный захват

ПРИЁМКА

Нагрузка от T1/T2 передаётся на пол. Мебель не зажимает корпуса, не перекрывает сервис и не требует перестановки техники для доступа к коммуникациям.

ОТДЕЛКА И ВИЗУАЛЬНЫЙ ХАРАКТЕР

Спокойная функциональная палитра: тёплый серо-бежевый пол, светлый дуб, белая техника, сатинированная бронза только в деталях

K1 стены - тёплый светло-серый, матовый


K2 пол - керамогранит 600 × 600, матовый, R10

K3 мебель - светлый дуб, матовый HPL/шпон

K4 техника - мягкий белый

K5 акценты - приглушённая сатинированная бронза

Пол: две полные плитки 600 мм + симметричные подрезки ориентировочно 265/270 мм. Проверить по контрольному размеру 1745 мм, не усреднять.

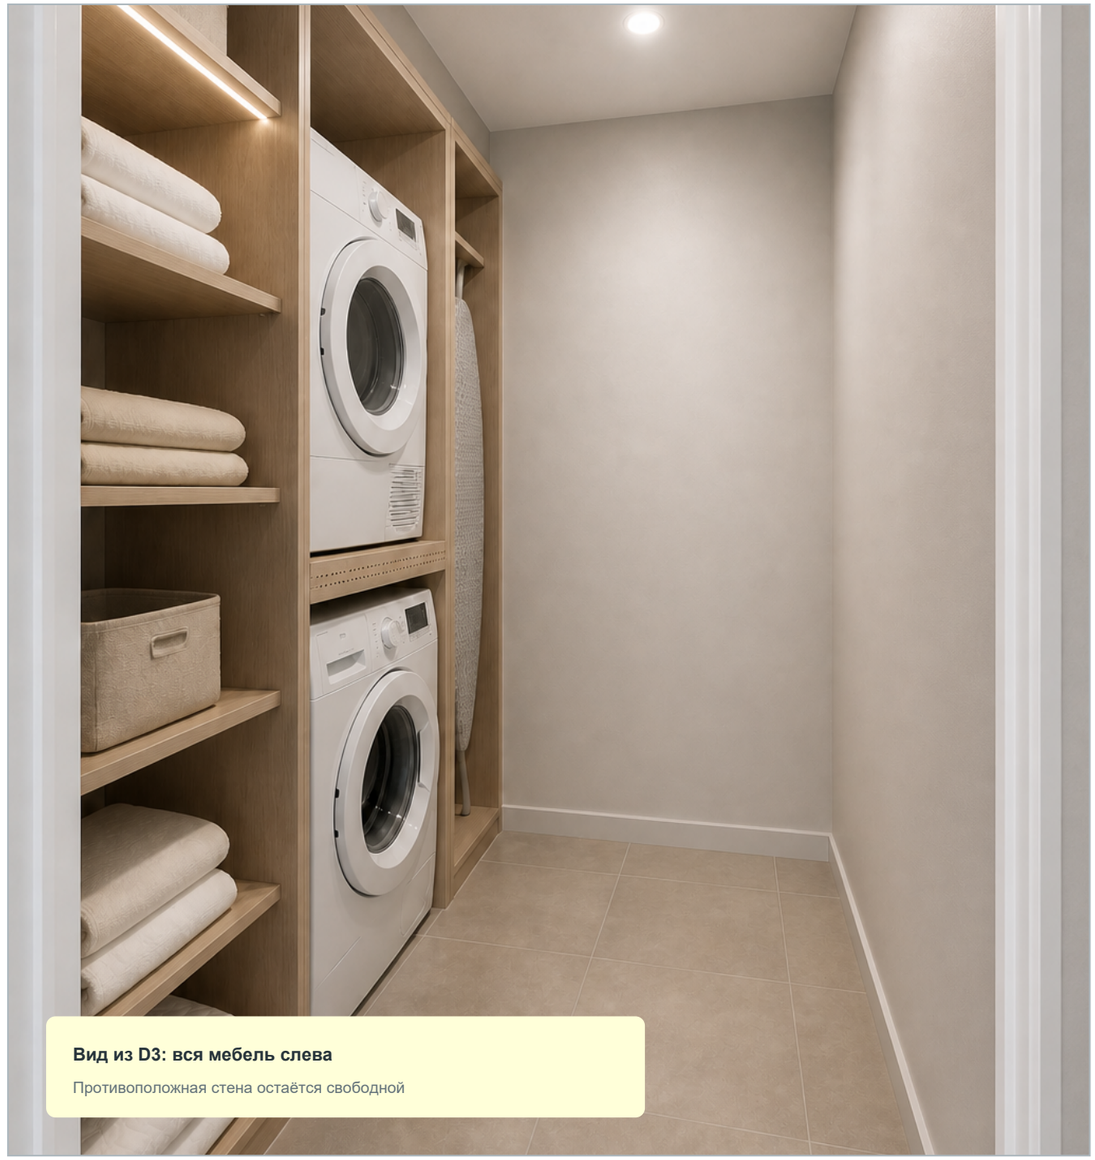

Вид из D3: вся мебель слева

Противоположная стена остаётся свободной

КОД	ПОЗИЦИЯ	ПАРАМЕТР	СТАТУС
M1	**Открытые полки**	800 × 280 мм; без дверей	в проекте
M2	**Техническая ниша**	640 × 620 мм; открытая сзади	в проекте
M3	**Ниша гладильной доски**	300 × 620 мм; чистая H ≥1450	в проекте
T1	**Haier HW100-BD14979U1**	проверить шильдик/глубину/подключение у продавца	к покупке после проверки
T2	**Haier HD80-D357U1-S**	проверить модификацию и совместимость комплекта	к покупке после проверки
T3	**HASTKU10**	монтажный комплект между T1 и T2	к покупке после проверки
T4	**RUTER 404.716.11**	доска; рабочая плоскость 108 × 33 см	к покупке

ПОКУПКА Ни один продавец не заменяет паспорт: фотография шильдика, точная глубина с шлангами, схема установки, напряжение/вилка и условия гарантии - обязательны для T1-T3.

НАТУРНЫЙ ОБМЕР И ВЫПУСК В РАБОТУ

Это финальная мебельная схема; инженерные решения выпускаются отдельным актом после обмера именно прачечной

01

D3

чистая ширина проёма, сторона петель, наличник и наружное открывание

02

ПОТОЛОК

высота, световые точки, положение вентиляции и возможность верхних полок

03

M2

реальная глубина T1/T2 с шлангами, розетками и открытыми дверцами

04

F1/M3

макет F1 и разложенной доски; ничто не пересекает D3 и проход

05

ИНЖЕНЕРИЯ

отдельное фото прачечной с рулеткой от двух углов и заключение сантехника

06

ПРИЁМКА

M1 + M2 + M3 = 1740; проход у M2 ≈1110; задняя стенка M2 открыта

СТОП ДО ЗАКАЗА

Не заказывать приборы или зашивать стены по фото из другого помещения. Пока не будет отдельного обмера прачечной, правая и задняя стены остаются свободным резервом.

Основание для финальной мебели: B01 1730 × 1740, M1 800 × 280, M2 640 × 620, M3 300 × 620, D3 наружу. Контрольный размер 1745 × 1740 не усредняется.