
МАСШТАБНЫЙ ОБМЕРНЫЙ ПЛАН КВАРТИРЫ

Лист А3 · М 1:50 при печати 100% · единицы на размерных линиях — мм · редакция 7 · 10.08.2026

Основание: контрольные обмеры S01–S14. Сплошной контур = размер подтверждён; пунктир = связь помещений без полной координатной цепочки.

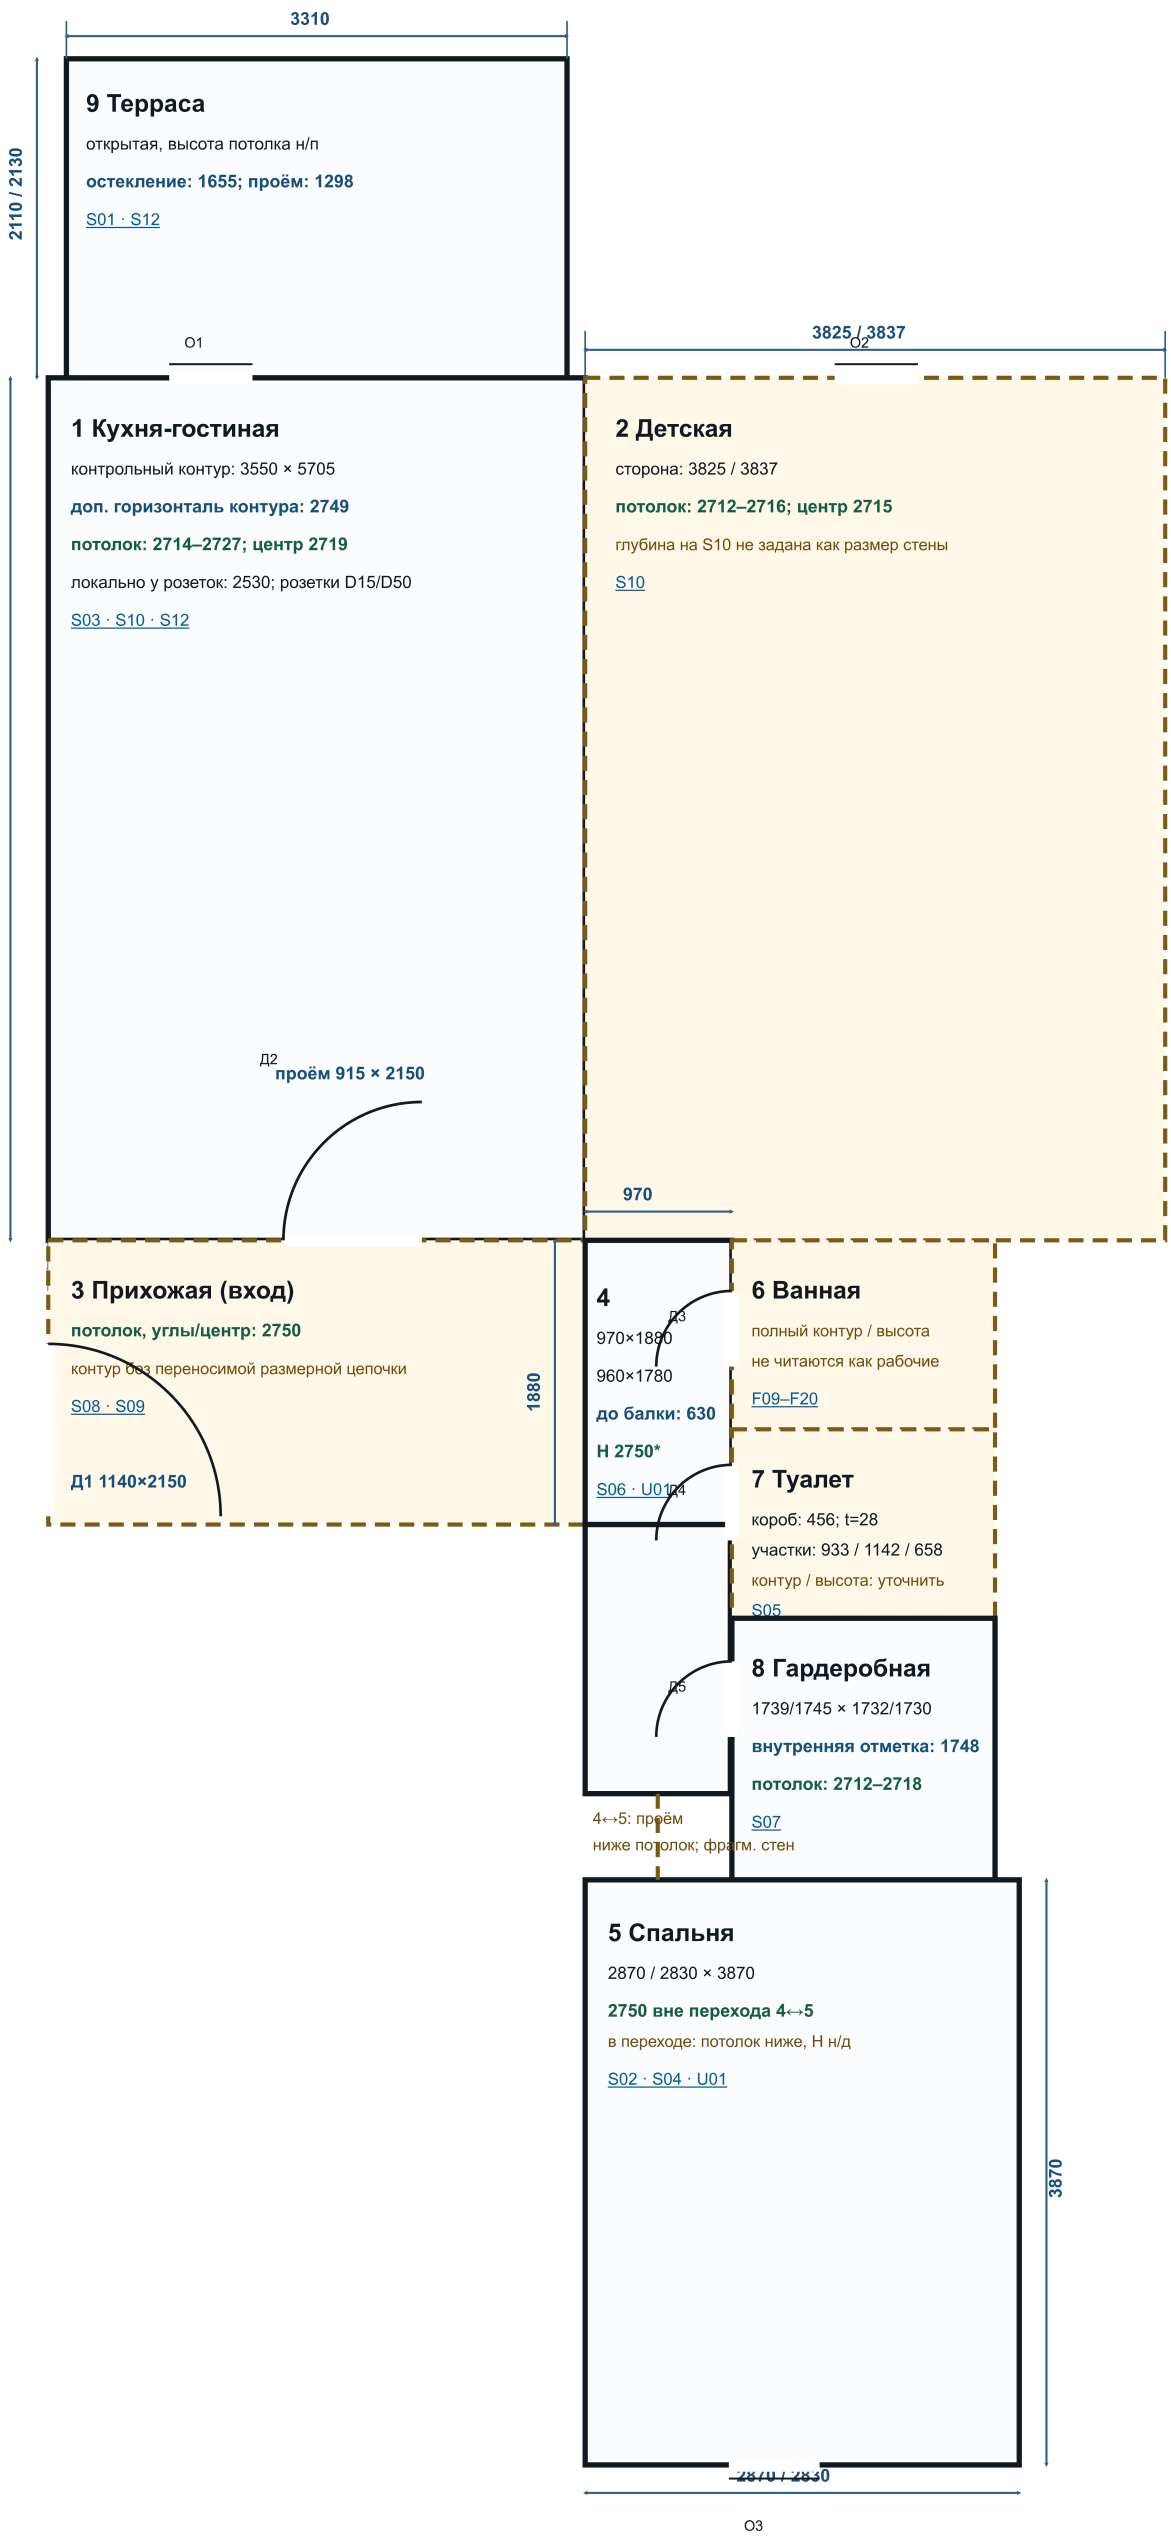

Статус масштаба

1 drawing mm = 50 real mm.

Проверка печати: масштабная линейка ниже.

0 1000 2000 мм

Условные обозначения

подтверждённый масштабный контур

схемное положение; размерной цепочки нет

контрольный размер, мм

Размеры и высоты

Плановые размеры — синим; значения потолка — зелёным. Разные значения не усреднялись.

Неподтверждённые зоны

Детская: отсутствует второй плановый размер. Прихожая: нет замкнутой цепочки. Ванная и туалет: рабочий полный контур и высоты не считываются в доступных JPG.

Ключевые источники

S14 — взаимное расположение 1–9

S12 — кухня-гостиная, потолок

S10 — детская и проём

S09 — прихожая

S06 — коридор

S02 — спальня

S07 — гардеробная

Проёмы по S14

Перед применением

О1 — кухня, О2 — детская, О3 — спальня.
Д1 — вход 1140×2150; Д2 — кухня/прихожая 915×2150.
Д3–Д5 — санузлы и гардеробная.
Для О1–О3, Д3–Д5 на S14 нет линейных привязок: показано положение, не ширина.

Перед применением

Не использовать пунктирные контуры для заказа мебели, плитки или переноса стен. Для этого нужны недостающие размеры и повторная проверка на объекте.