
АРТ-001 | ПОДРОБНЫЙ ПЛАН КОНТРОЛЬНЫХ ОБМЕРОВ

B01 БТИ + C01-C07/C09/C10/C12 + U01 + T01/V01; модель 1:1 мм; лист A2; печать M 1:50


Чужой референс: только оформление, данные запрещены

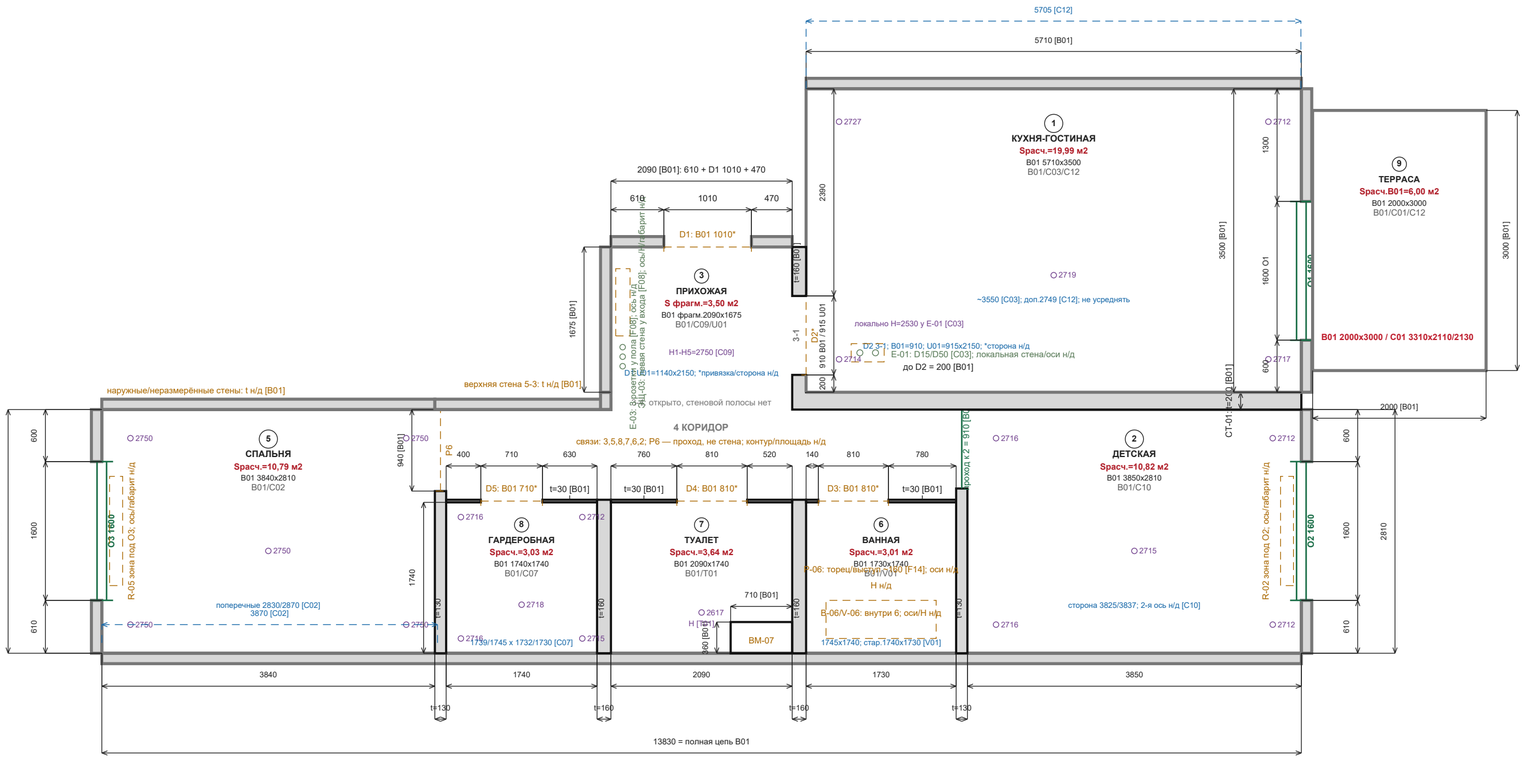

ЛОКАЛЬНЫЕ УЗЛЫ / НЕЗАМКНУТЫЕ ДАННЫЕ

не использовать как глобальные координаты без указанной привязки


4 КОРИДОР — локальные фрагменты [C06]

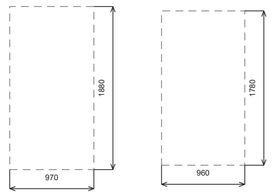

H отмеченных точек = 2750
проход до балки = 630
P6=940: H ниже, отметка н/д
полный контур коридора н/д

7 ТУАЛЕТ — локальный узел [B01/T01]

контур B01 2090x1740; ориентация T01 к плану н/д

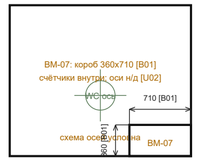

H потолка 2617
D4: предвар.705x2027
открывание наружу; петли н/д
WC: 550 от задней; 1621 от правой
проход от оси 824 до передней
вода: 620 от левой; h=200
BM-07: короб 360x710 [B01]; оси внутри н/д [U02]
канализация WC: 460-470; h=80
раковина: канализация h=240
кабель: h=1850; 1030/250
вентрешётка 260x260; 40/80
Л-07 щиток/лючок S05: 456; t28; 933/1142/658

9 ТЕРРАСА — конфликт контуров



B01: 2000x3000
C01: 3310x2110/2130
остекление 1655
проём 1298 [C12]
не совмещать без замера

НЕОПРЕДЕЛЁННОСТИ / НЕПРИВЯЗАННЫЕ ЭЛЕМЕНТЫ

1. наружная t стен
2. полный верхний контур/площадь коридора
3. привязки D1/D2 к углам
4. D3/D5 W/H н/д; D4 перепроверить 705x2027
5. H пониженного потолка P6
6. H подоконников и габариты радиаторов
7. H ванной и глобальные оси инженерии
8. ЭЩ-03: габарит/H/ось на стене н/д
9. BM-07: оси, H и габарит люка н/д
10. Л-07: тип и связь с BM-07 н/д

E-01 кухня: D15/D50; оси/H н/д [C03]
ЭЩ-03 прихожая: габарит/H/ось н/д [F08]
E-03: 3 розетки у пола в прихожей [F08]; ось н/д
R-02/R-05 под O2/O3; габарит/H н/д
WC: подтверждён; точные локальные оси — узел выше

M 1:50: 1000 мм = 20 мм

0 — 500 — 1000 мм

УСЛОВНЫЕ ОБОЗНАЧЕНИЯ И ПРАВИЛА

- внутренние стены B01 с t=30/130/160/200
- наружные/неразмерённые стены; t числом н/д
- размеры/цепочки B01
- контрольные обмеры Cxx/U01
- проёмы и окна
- существующее оборудование/зона
- точечные отметки потолка
- конфликт источников
- неизвестно / нужна привязка

Приоритет: контроль для заказа; B01 для топологии.
Не усреднять разные стороны и источники.
Sрасч. — геометрический расчёт, не официальная площадь.
* Дуги D1-D5 не показаны; D4 наружу, петли н/д; сегмент B01 не равен чистой W.
R01 (чужой пример) — только графический стиль.
Полная матрица: docs/11_Паспорт_подробного_обмерного_плана.md

ЭКСПЛИКАЦИЯ ПОМЕЩЕНИЙ / ПОСЛЕ ОБМЕРОВ

№	Помещение	B01, мм	Sрасч.	H, мм	Статус
1	Кухня-гостиная	5710x3500	19,99	2714/2717/2727/2712; ц.2719	B01 + контроль
2	Детская	3850x2810	10,82	2712/2716; ц.2715	B01; 1 ось контроля
3	Прихожая	фрагм.2090x1675	3,50*	2750 (5 точек)	не полная площадь
4	Коридор	контур н/д	н/д	2750; P6 ниже н/д	топология + вставки
5	Спальня	3840x2810	10,79	2750 (5 точек)	B01 + контроль
6	Ванная	1730x1740	3,01	н/д	конфликт контроля
7	Туалет	2090x1740	3,64	2617 [T01]	инженерия локально
8	Гардеробная	1740x1740	3,03	2712-2718	4 контрольные стороны
9	Терраса	2000x3000	6,00 B01	не применяется	сильный конфликт

АРТ-001

ПОДРОБНЫЙ ОБМЕРНЫЙ ПЛАН

БТИ S15 + контрольные обмеры + фото

Лист	**04**	Масштаб	**1:50**
Формат	A2, альбом	Ед.	мм
Дата	11.08.2026	Рев.	13

Красные/оранжевые позиции не применять без проверки

Исходные фото не изменялись; публикация не выполнялась