
КУХНЯ-ГОСТИНАЯ | ВАРИАНТ А | М 1:25

B01 и проемы - фактические. Мебель и техника - проектные габаритные конверты до выбора SKU.

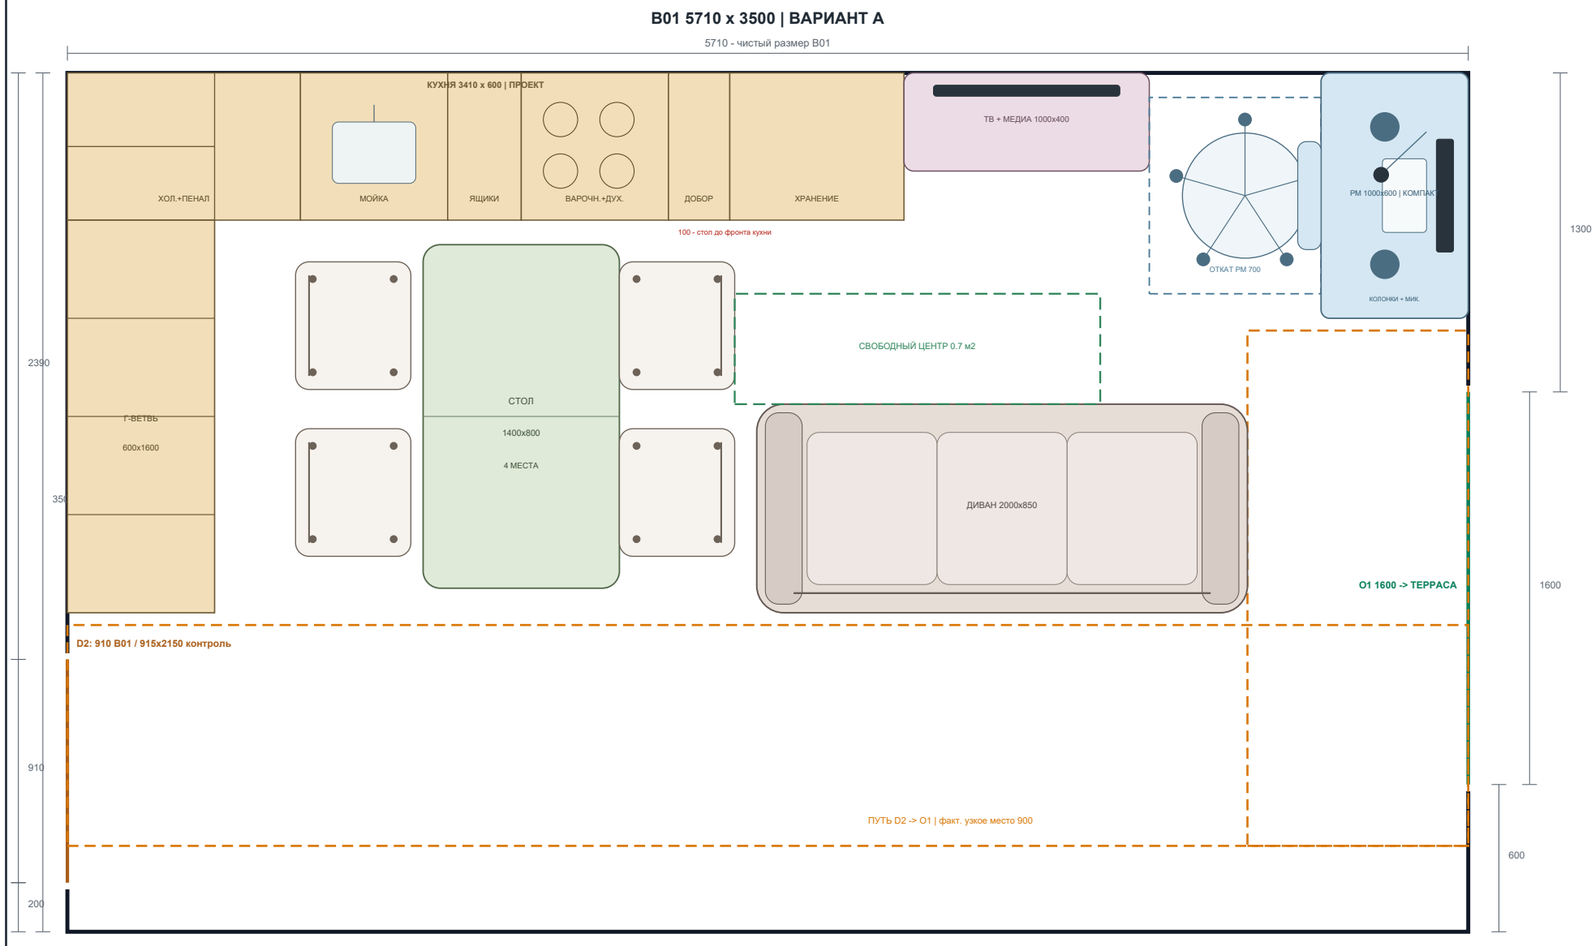

A - КЛАССИЧЕСКИЙ БАЛАНС

Г-кухня, обычный стол, диван лицом к ТВ,

компактное РМ у O1

2.3/5

ИЗМЕРИМАЯ ОЦЕНКА

Маршрут D2-O1	900	4
У кухни	100	1
За стулом	90	1
Откат РМ	700	2
Закр. хранение*	5010	5
Своб. прямоуг.*	0.7 м2	1
Ребёнок/питомцы*	2 рег.	2

ПЛЮСЫ

+ Полноценный стол на 4

+ Максимум кухонного хранения

+ Прямой обзор ТВ

КОМПРОМИССЫ

- РМ только 1000x600

- 100 мм у рабочего фронта

- 90 мм и 2 тесные зоны для ребёнка/питомцев

1000 мм = 40 мм на листе

ФАКТ: B01 5710x3500; D2 200+910 (контроль 915x2150); O1 600+1600+1300.

РЕКОМЕНДАЦИИ NKBA, не нормы РБ: проход 914; рабочий проход 1067 для одного; за стулом без транзита 813.

ПРОЕКТ*: откат РМ 900; хранение = кухня + закрытая сторона полуострова/банкетки; свободный прямоугольник считается выше маршрута.

ОЦЕНКА: проходы 5=ориентир; 4=до 50 ниже; 3=51-150; 2=151-250; 1=>250. Хранение: 5>=4000; 4>=3400; 3>=2800; 2>=2200; 1<2200.

СВОБ. ЗОНА*: 5>=4.0; 4>=3.0; 3>=2.2; 2>=1.5; 1<1.5 м2 непрерывного незанятого пола выше маршрута.


СЕМЬЯ*: 5=нет конфликтов; 4=один редкий; 3=один регулярный; 2=два; 1=три и более либо блокировка маршрута ребёнком/питомцем.

КОНТРОЛЬ: вода, E-01, радиаторы и конкретные модели мебели/техники требуют привязки до рабочей документации.

КУХНЯ-ГОСТИНАЯ | ВАРИАНТ B | М 1:25

B01 и проемы - фактические. Мебель и техника - проектные габаритные конверты до выбора SKU.

B01 5710 x 3500 | ВАРИАНТ B

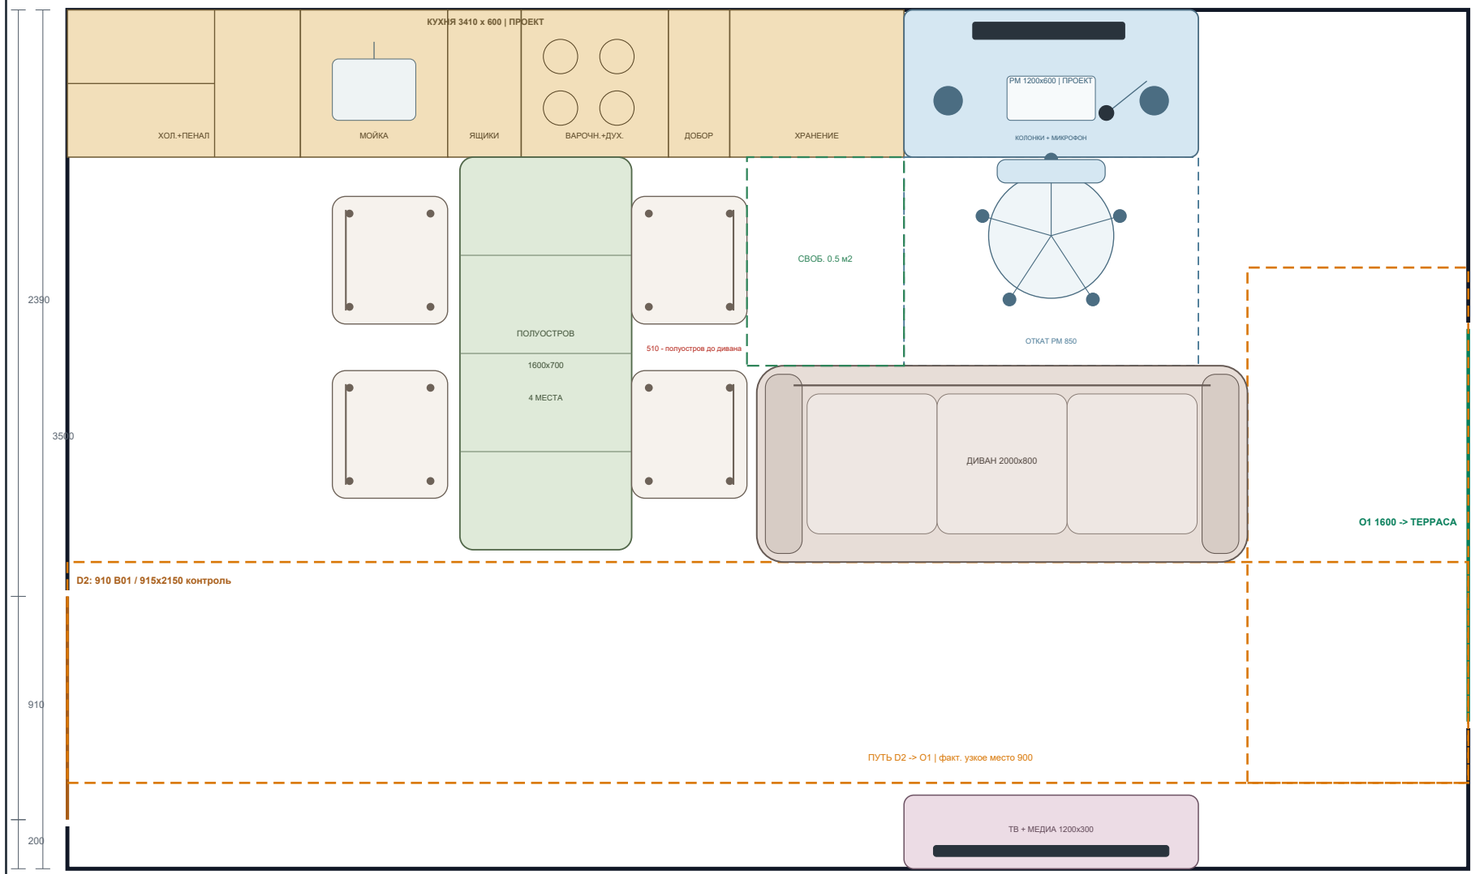

1000 мм = 40 мм на листе

B - КУХНЯ С ПОЛУОСТРОВОМ

Прямая кухня, РМ в верхней линии, полуостров для еды и хранения

2.6/5

ИЗМЕРИМАЯ ОЦЕНКА

Маршрут D2-O1	900	4
У полуострова	510	1
За стулом	40	1
Откат РМ	850	4
Закр. хранение*	5010	5
Своб. прямоуг.*	0.5 м2	1
Ребёнок/питомцы*	2 рег.	2

ПЛЮСЫ

+ Больше столешницы
+ Четыре посадочных места
+ РМ шириной 1200

КОМПРОМИССЫ

- 40 мм за правыми стульями
- Стулья конфликтуют с путём ребёнка/питомцев
- Узкий боковой проход 510

ФАКТ: B01 5710x3500; D2 200+910 (контроль 915x2150); O1 600+1600+1300.

РЕКОМЕНДАЦИИ NKBA, не нормы РБ: проход 914; рабочий проход 1067 для одного; за стулом без транзита 813.

ПРОЕКТ*: откат РМ 900; хранение = кухня + закрытая сторона полуострова/банкетки; свободный прямоугольник считается выше маршрута.

ОЦЕНКА: проходы 5=ориентир; 4=до 50 ниже; 3=51-150; 2=151-250; 1=>250. Хранение: 5>=4000; 4>=3400; 3>=2800; 2>=2200; 1<2200.


СВОБ. ЗОНА*: 5>=4.0; 4>=3.0; 3>=2.2; 2>=1.5; 1<1.5 м2 непрерывного незанятого пола выше маршрута.

СЕМЬЯ*: 5=нет конфликтов; 4=один редкий; 3=один регулярный; 2=два; 1=три и более либо блокировка маршрута ребёнком/питомцем.

КОНТРОЛЬ: вода, E-01, радиаторы и конкретные модели мебели/техники требуют привязки до рабочей документации.

КУХНЯ-ГОСТИНАЯ | ВАРИАНТ C | М 1:25

B01 и проемы - фактические. Мебель и техника - проектные габаритные конверты до выбора SKU.

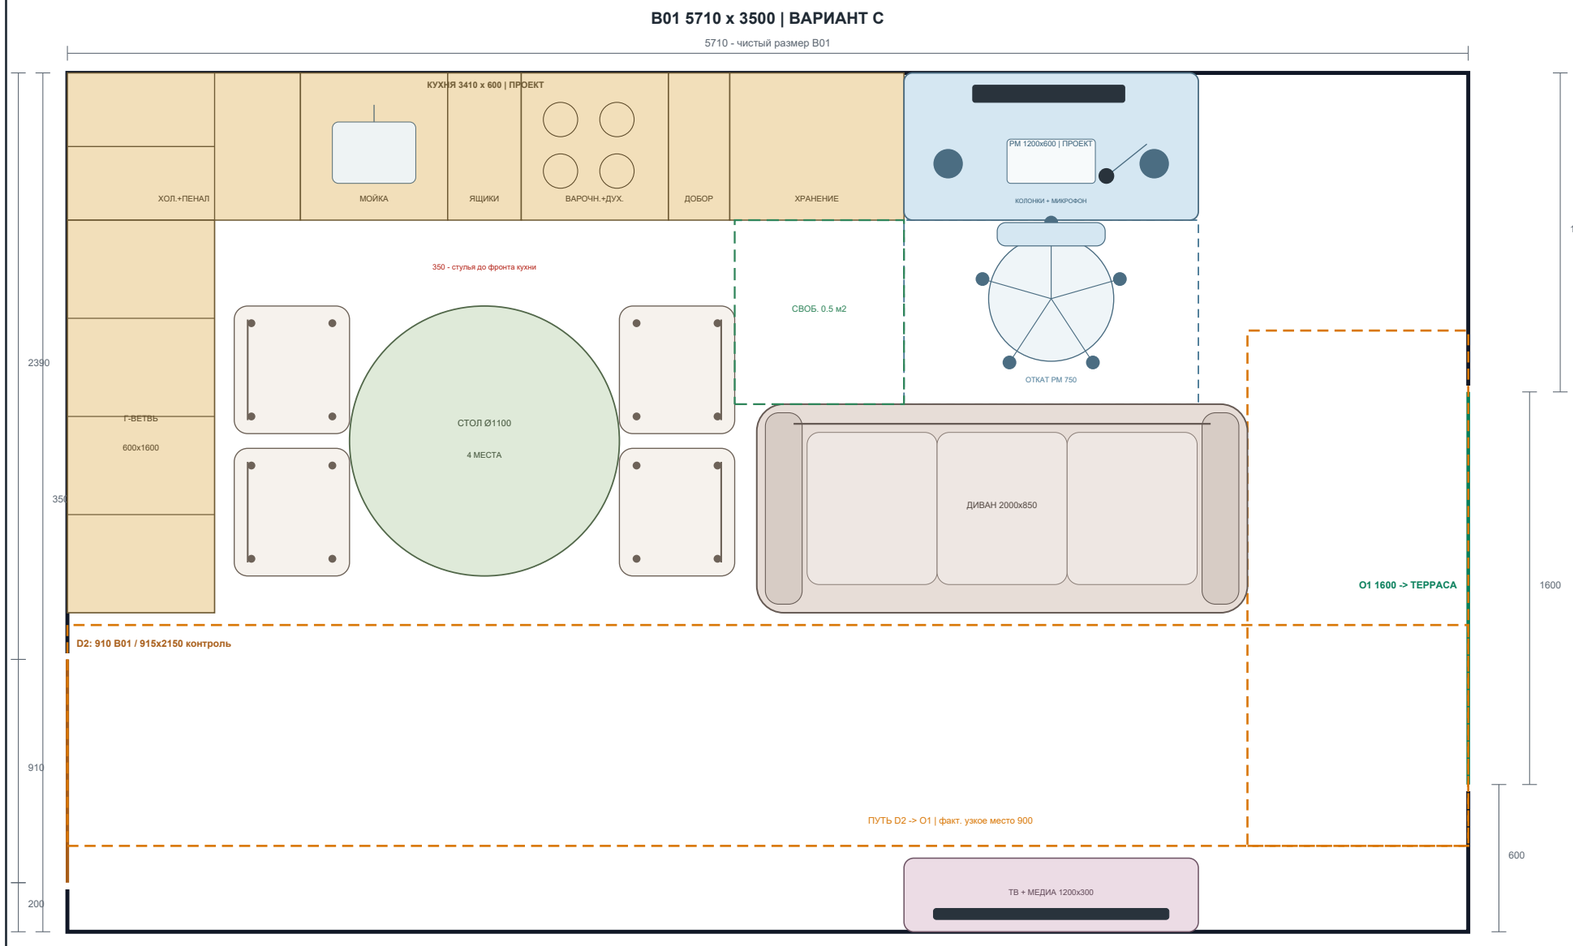

C - КРУГЛЫЙ СТОЛ + ВСТРОЕННОЕ РМ

Г-кухня, круглый стол, РМ в общей верхней линии, диван-зонирование

2.3/5

ИЗМЕРИМАЯ ОЦЕНКА

Маршрут D2-O1	900	4
У кухни	350	1
За стулом	90	1
Откат РМ	750	3
Закр. хранение*	5010	5
Своб. прямоуг.*	0.5 м2	1
Ребёнок/питомцы*	3 рег.	1

ПЛЮСЫ

+ Мягкая круглая геометрия

+ РМ 1200x600

+ Удобное общение за столом

КОМПРОМИССЫ

- 350 мм у рабочего фронта

- 90 мм у дивана; 3 тесные зоны для ребёнка/питомцев

- Откат кресла только 750

1000 мм = 40 мм на листе

ФАКТ: B01 5710x3500; D2 200+910 (контроль 915x2150); O1 600+1600+1300.

РЕКОМЕНДАЦИИ NKBA, не нормы РБ: проход 914; рабочий проход 1067 для одного; за стулом без транзита 813.

ПРОЕКТ*: откат РМ 900; хранение = кухня + закрытая сторона полуострова/банкетки; свободный прямоугольник считается выше маршрута.

ОЦЕНКА: проходы 5=ориентир; 4=до 50 ниже; 3=51-150; 2=151-250; 1=>250. Хранение: 5>=4000; 4>=3400; 3>=2800; 2>=2200; 1<2200.


СВОБ. ЗОНА*: 5>=4.0; 4>=3.0; 3>=2.2; 2>=1.5; 1<1.5 м2 непрерывного незанятого пола выше маршрута.

СЕМЬЯ*: 5=нет конфликтов; 4=один редкий; 3=один регулярный; 2=два; 1=три и более либо блокировка маршрута ребёнком/питомцем.

КОНТРОЛЬ: вода, E-01, радиаторы и конкретные модели мебели/техники требуют привязки до рабочей документации.

КУХНЯ-ГОСТИНАЯ | ВАРИАНТ D | М 1:25

B01 и проемы - фактические. Мебель и техника - проектные габаритные конверты до выбора SKU.

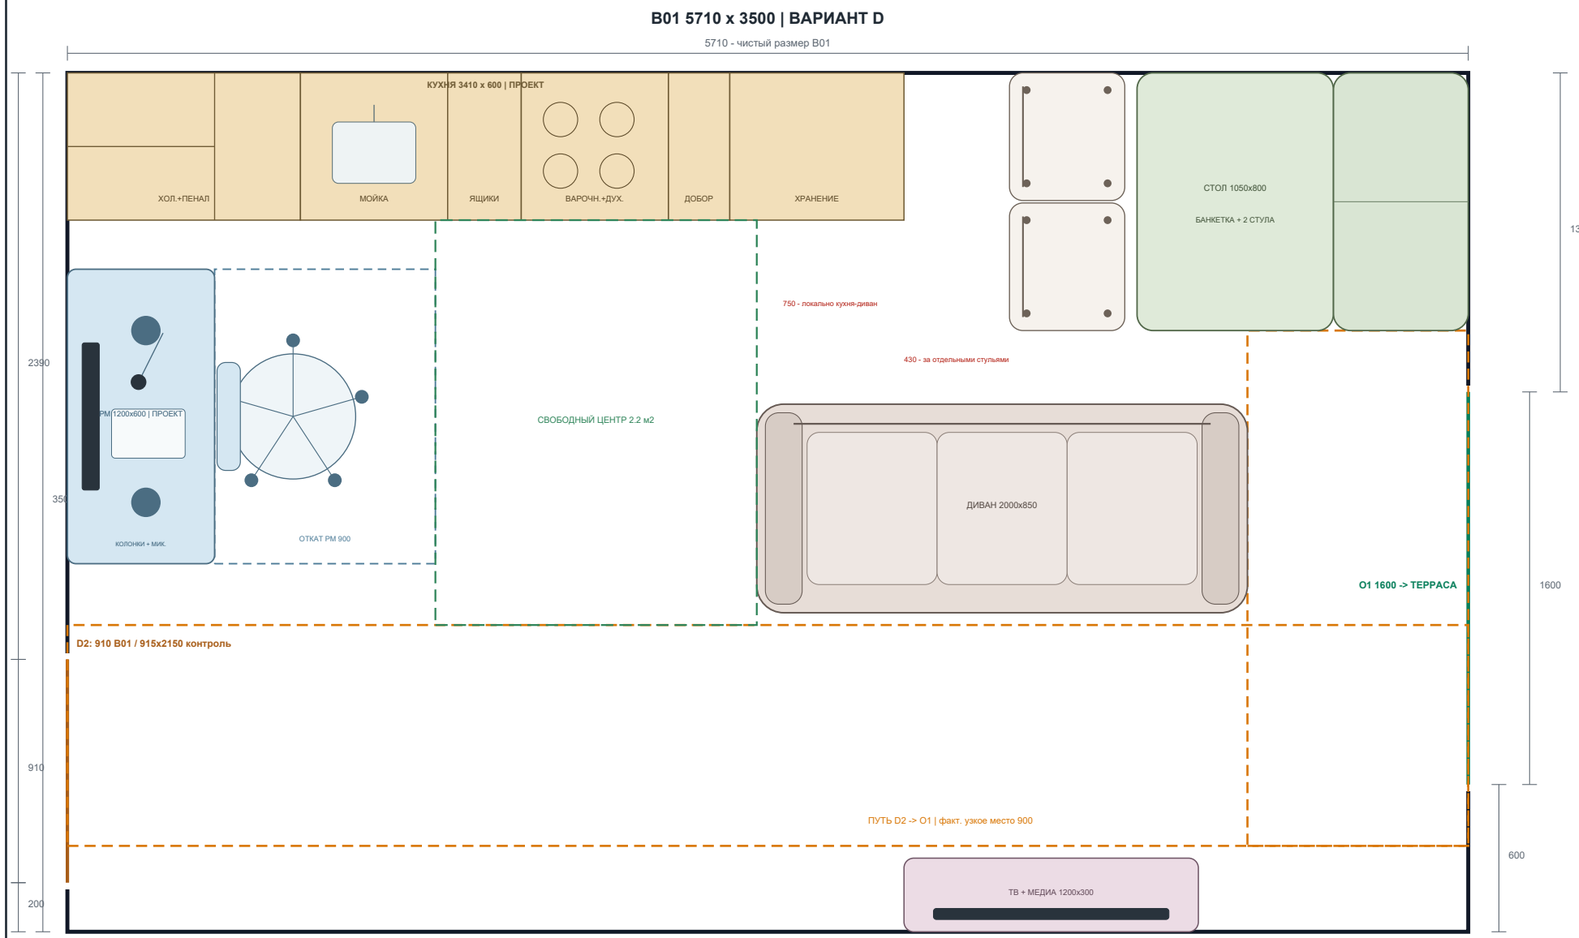

1000 мм = 40 мм на листе

D - СЕМЕЙНАЯ БАНКЕТКА

Прямая кухня, РМ слева, банкетка у верхнего простенка O1, свободный центр

3.3/5
РЕКОМЕНДУЮ

ИЗМЕРИМАЯ ОЦЕНКА

Маршрут D2-O1	900	4
Кухня-диван	750	1
За стулом	430	1
Откат РМ	900	5
Закр. хранение*	4460	5
Своб. прямоуг.*	2.2 м2	3
Ребёнок/питомцы*	1 редк.	4

ПЛЮСЫ

+ Свободный центр для ребёнка/питомцев

+ РМ 1200x600 вне маршрута

+ Детям удобно на банкетке

КОМПРОМИССЫ

- Локально кухня-диван 750

- 430 мм за отдельными стульями

- Банкетка только на заказ

ФАКТ: B01 5710x3500; D2 200+910 (контроль 915x2150); O1 600+1600+1300.

РЕКОМЕНДАЦИИ NKBA, не нормы РБ: проход 914; рабочий проход 1067 для одного; за стулом без транзита 813.

ПРОЕКТ*: откат РМ 900; хранение = кухня + закрытая сторона полуострова/банкетки; свободный прямоугольник считается выше маршрута.

ОЦЕНКА: проходы 5=ориентир; 4=до 50 ниже; 3=51-150; 2=151-250; 1=>250. Хранение: 5>=4000; 4>=3400; 3>=2800; 2>=2200; 1<2200.

СВОБ. ЗОНА*: 5>=4.0; 4>=3.0; 3>=2.2; 2>=1.5; 1<1.5 м2 непрерывного незанятого пола выше маршрута.

СЕМЬЯ*: 5=нет конфликтов; 4=один редкий; 3=один регулярный; 2=два; 1=три и более либо блокировка маршрута ребёнком/питомцем.

КОНТРОЛЬ: вода, E-01, радиаторы и конкретные модели мебели/техники требуют привязки до рабочей документации.