Ведомость рабочих чертежей

Лист	Наименование	Примечание
1	ВЕДОМОСТЬ ЧЕРТЕЖЕЙ	
2	ОБМЕРНЫЙ ПЛАН	
3	ПЛАН ДЕМОНТАЖА	
4	ПЛАН ВОЗВОДИМЫХ ПЕРЕГОРОДОК И КОНСТРУКЦИЙ	
4.1	ФРАГМЕНТ ВАННОЙ	
4.2	СХЕМА УСТАНОВКИ СТЕКЛА В ВАННОЙ	
4.3	ФРАГМЕНТ ГОСТИНОЙ	
4.4	СХЕМА УСТАНОВКИ СКРЫТЫХ ПЛИНТУСОВ	
5	ПЛАН-СХЕМА ОТОПИТЕЛЬНЫХ ПРИБОРОВ	
6	АРХИТЕКТУРНО-СТРОИТЕЛЬНЫЙ ПЛАН	
7	ПЛАН ЗАПОЛНЕНИЯ ПРОЕМОВ	
8	ПЛАН РАССТАНОВКИ МЕБЕЛИ	
9	ПЛАН РАЗМЕЩЕНИЯ САНТЕХНИЧЕСКОГО ОБОРУДОВАНИЯ. КУХНЯ.	
9.1	ПЛАН РАЗМЕЩЕНИЯ САНТЕХНИЧЕСКОГО ОБОРУДОВАНИЯ. ВАННАЯ	
9.2	СПЕЦИФИКАЦИЯ САНТЕХНИЧЕСКОГО ОБОРУДОВАНИЯ	
10	РАЗВЕРТКА ВАННОЙ	
10.1	РАЗВЕРТКА ВАННОЙ	
10.2	ВИЗУАЛИЗАЦИЯ ВАННОЙ	
11	ПЛАН НАПОЛЬНЫХ ПОКРЫТИЙ	
12	ПЛАН ТЕПЛОГО ПОЛА	

Ведомость рабочих чертежей

Лист	Наименование	Примечание
13	ПЛАН ПОТОЛКА	
13.1	СЕЧЕНИЯ ПОТОЛКА.	
13.2	ПЛАН ПОТОЛКА С ОТДЕЛКОЙ	
14	ПЛАН ОСВЕЩЕНИЯ С ПРИВЯЗКАМИ	
15	СХЕМА ВЫКЛЮЧЕНИЯ СВЕТИЛЬНИКОВ	
16	ПЛАН РАССТАНОВКИ РОЗЕТОК И ВЫКЛЮЧАТЕЛЕЙ	
16.1	СПЕЦИФИКАЦИИ ЭЛЕКТОРООБОРУДОВАНИЯ	
17	ПЛАН ОТДЕЛКИ СТЕН	
18	РАЗВЕРТКА ПРИХОЖЕЙ	
18.1	ВИЗУАЛИЗАЦИЯ ПРИХОЖЕЙ	
19	РАЗВЕРТКА КУХНИ ГОСТИНОЙ	
19.1	РАЗВЕРТКА КУХНИ ГОСТИНОЙ	
19.3	ВИЗУАЛИЗАЦИЯ КУХНИ ГОСТИНОЙ	
19.4	ВИЗУАЛИЗАЦИЯ КУХНИ ГОСТИНОЙ	
20	РАЗВЕРТКА СПАЛЬНИ	
20.1	РАЗВЕРТКА ЛОДЖИИ	
20.2	ВИЗУАЛИЗАЦИЯ СПАЛЬНИ	
20.3	ВИЗУАЛИЗАЦИЯ ЛОДЖИИ	
21	РАЗВЕРТКА ДЕТСКОЙ	
21.1	ВИЗУАЛИЗАЦИЯ ДЕТСКОЙ	
22	3Д схема шкафов в прихожей + кухня	

IVANCHUKINTERIOR

НАИМЕНОВАНИЕ ЧЕРТЕЖА / DRAWING TITLE

ВЕДОМОСТЬ ЧЕРТЕЖЕЙ

№ ЛИСТА/ DRAWING NO	1	ВЫПОЛНИЛ/ DRAWN BY	ИВАНЧУК А.Ю.
		ДАТА/ DATE	13.02.2026
		ГОРОД/ CITY	МИНСК

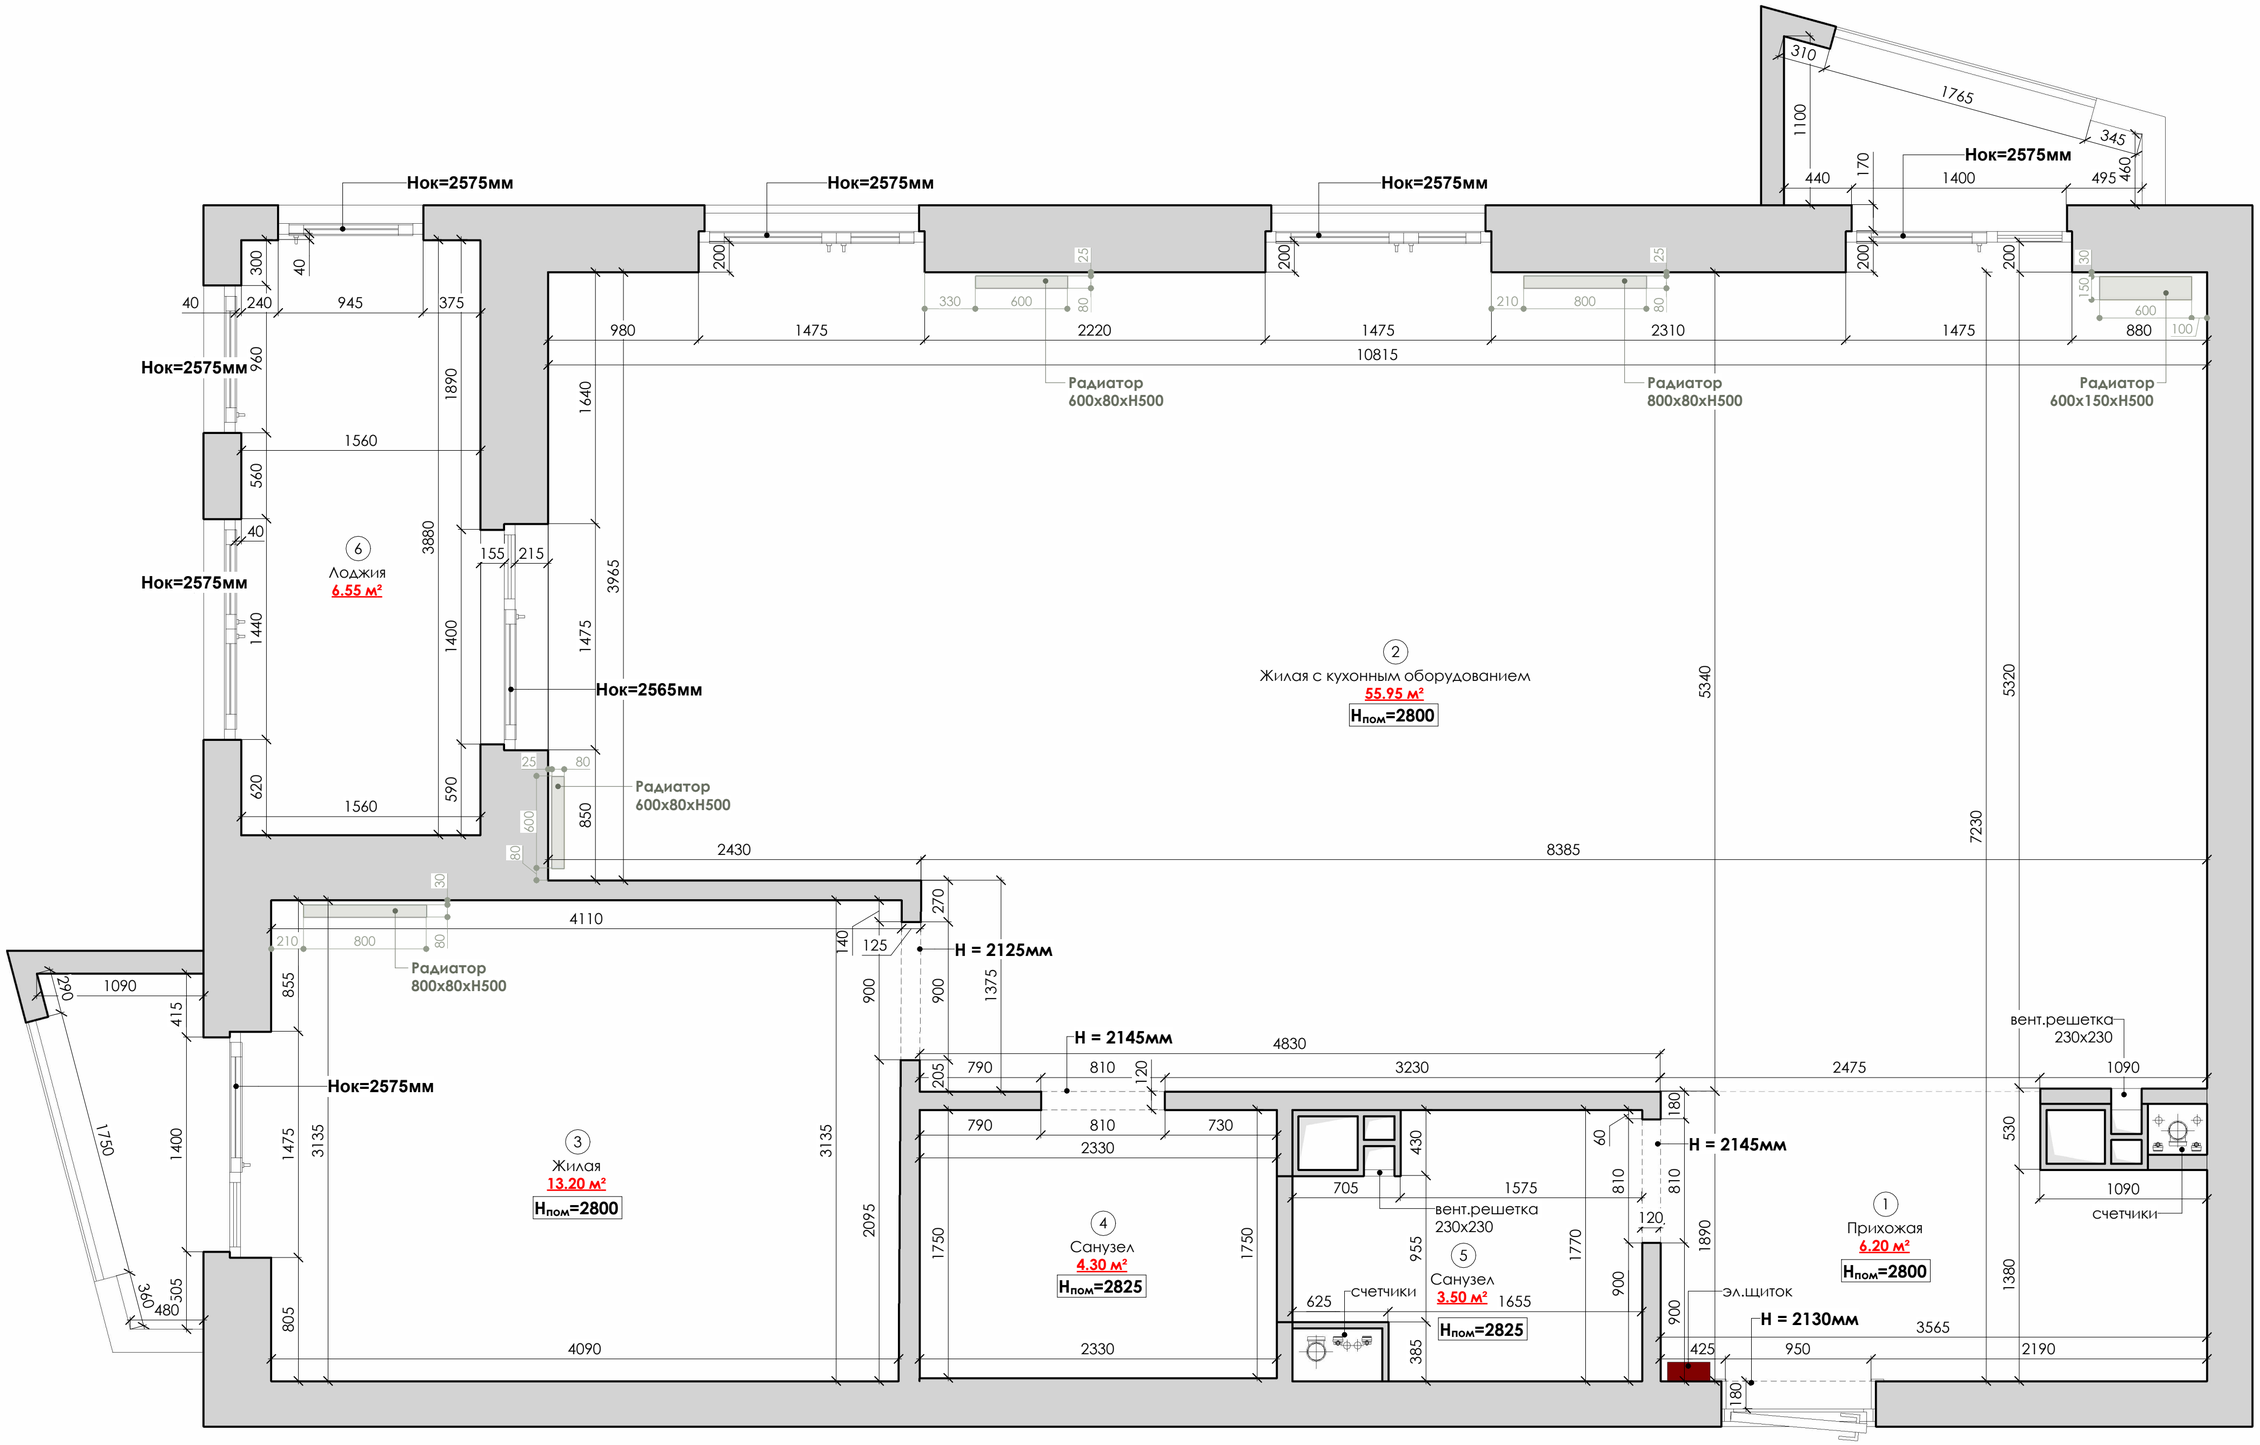
Нок=2575мм
Нок=2575мм
Нок=2575мм
Нок=2575мм
Нок=2575мм
Нок=2565мм
Нок=2575мм
6
Лоджия
6.55 м²
2
Жилая с кухонным оборудованием
55.95 м²
Нпом=2800
Радиатор
600x80xH500
Радиатор
800x80xH500
Радиатор
600x150xH500
Радиатор
600x80xH500
Радиатор
800x80xH500
H = 2125мм
H = 2145мм
H = 2145мм
H = 2130мм
3
Жилая
13.20 м²
Нпом=2800
4
Санузел
4.30 м²
Нпом=2825
5
Санузел
3.50 м²
Нпом=2825
1
Прихожая
6.20 м²
Нпом=2800
вент.решетка
230x230
вент.решетка
230x230
счетчики
счетчики
эл.щиток
10815
8385
4830
4110
4090
2330
2330
7230
5340
5320
3965
3880
3135
3135
2095
1640
1890
1400
1475
1400
1440
960
300
1560
560
620
1560
590
850
2430
1090
1750
1400
1475
415
855
805
1090
880
1380
530
1090
2190
3565
2475
3230
2310
2220
1475
1475
980
945
375
240
40
40
1765
1100
310
345
460
495
1400
440
170
1765
1100
310
345
460
495
1400
440
170
1090
880
100
150
30
600
1090
счетчики
1090
1090
вент.решетка
230x230
1090
счетчики
1090
1090
вент.решетка
230x230
1090
счетчики
1090
1090
вент.решетка
230x230

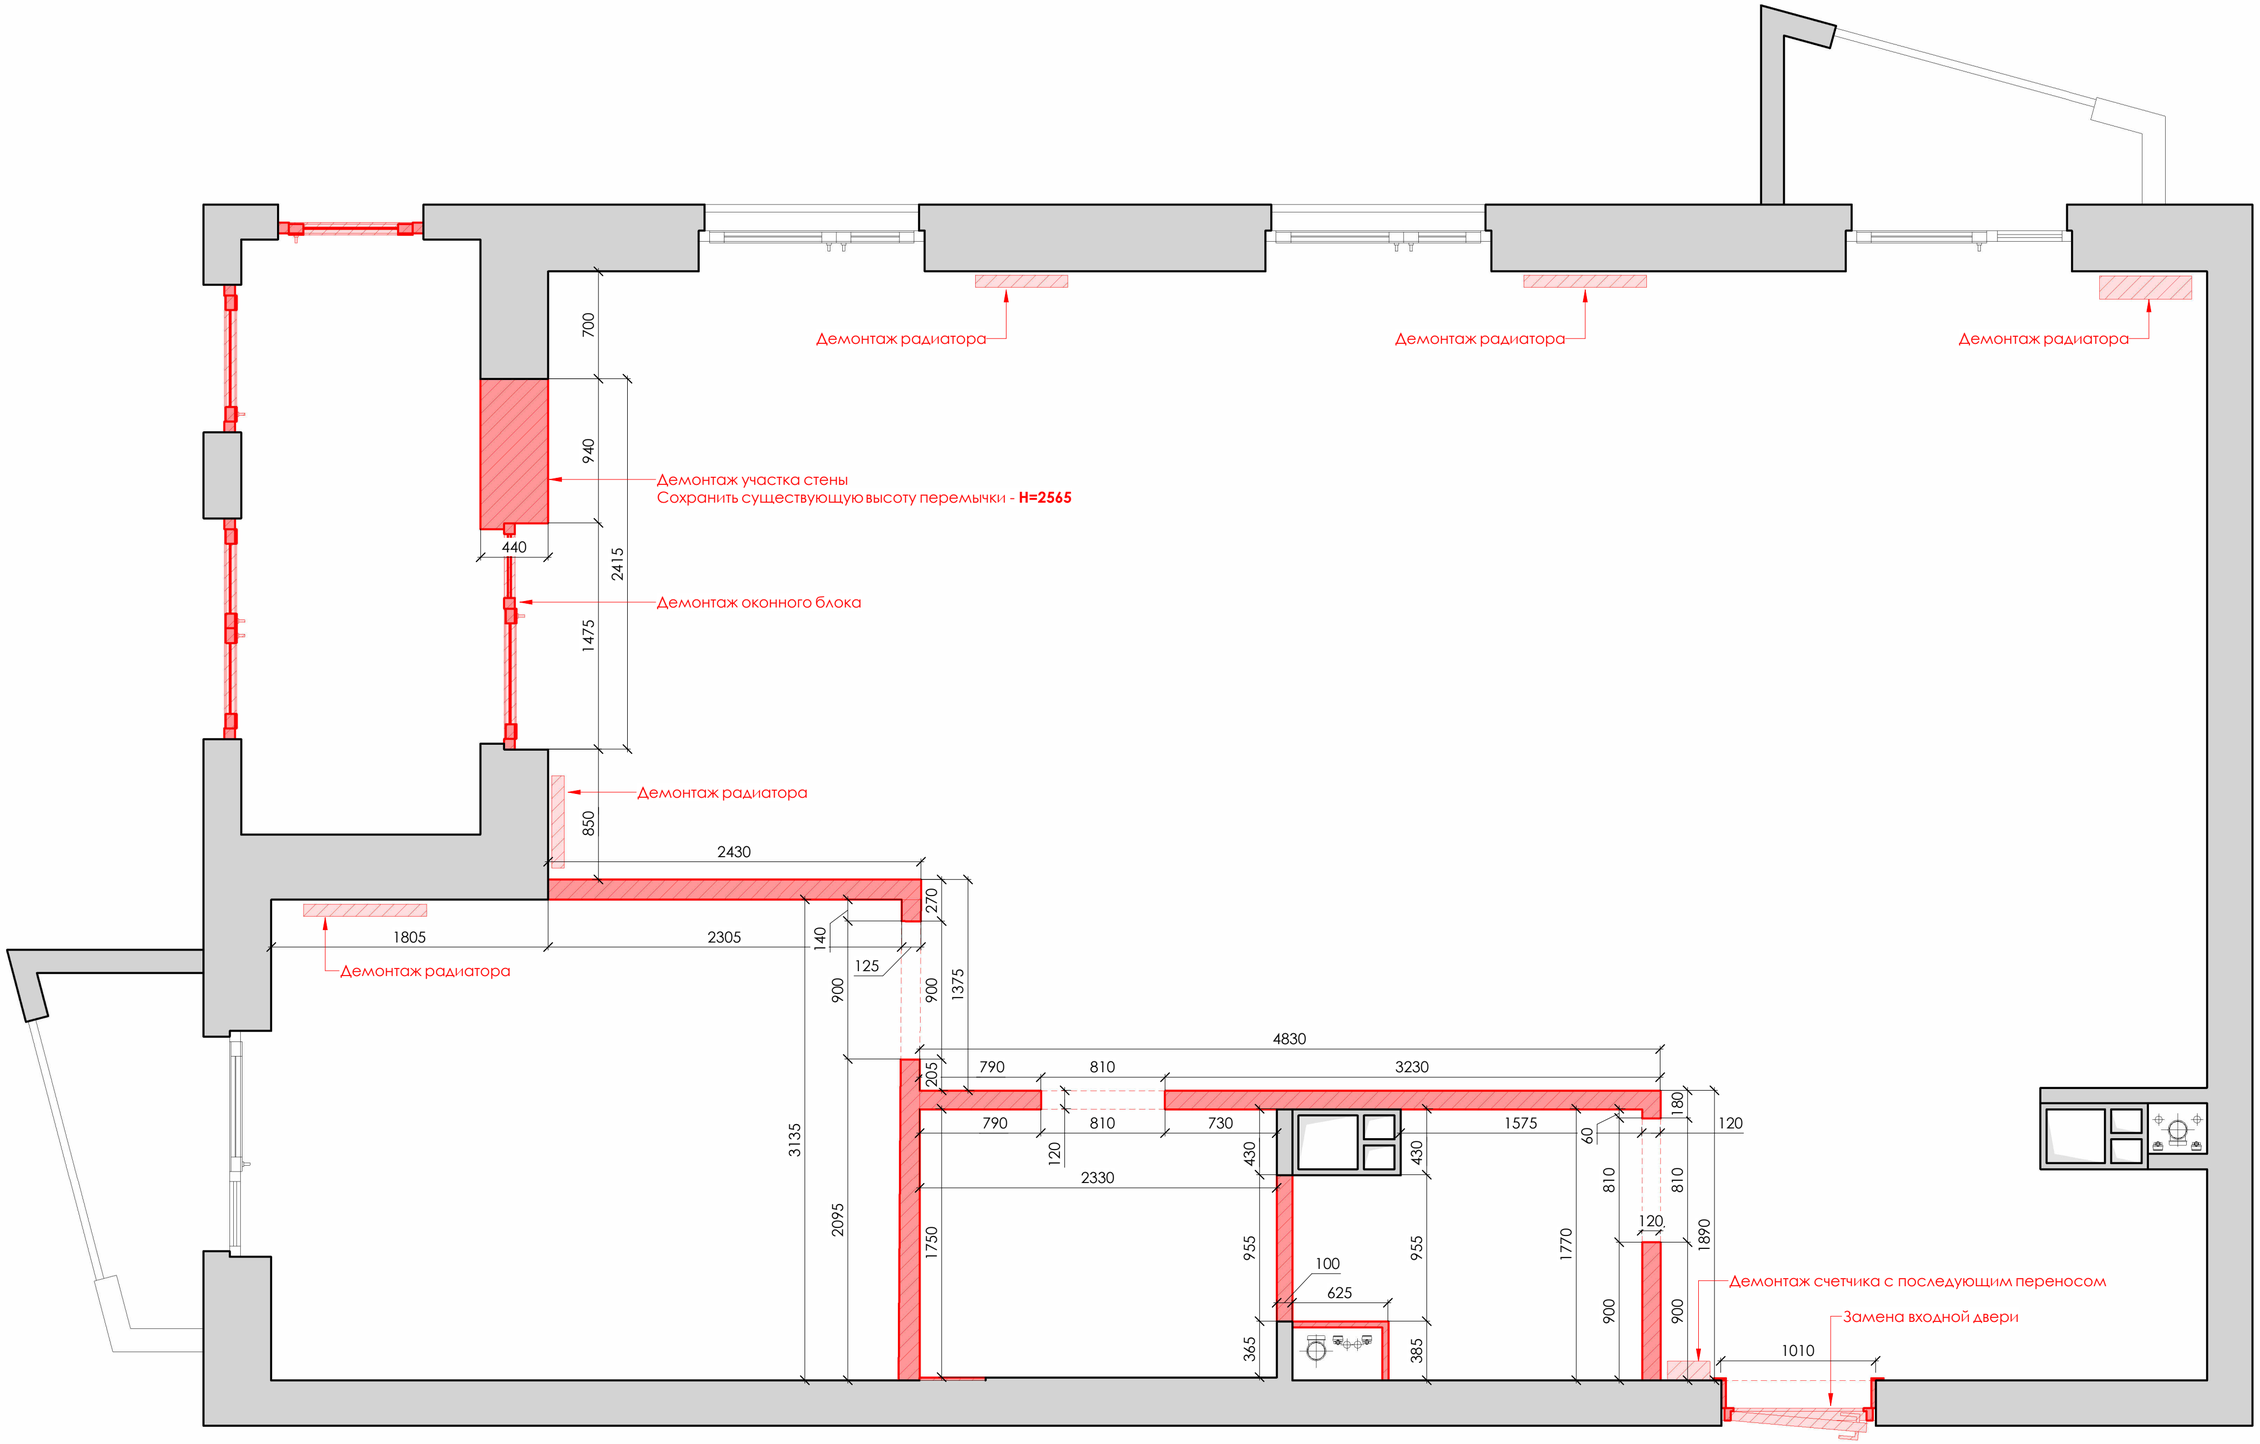

Условные обозначения:

- существующие стены
- демонтируемые перегородки
- шахта
- канализация, хол. , гор. водоснабжение

Примечания:

- Все размеры указаны в мм;
- Выполнить демонтаж штукатурки в углах, которые в обязательном порядке должны быть прямыми после выравнивания стен, если на момент демонтажа видна некачественно выполненная штукатурка;
- Выполнить демонтаж потрескавшейся стяжки.

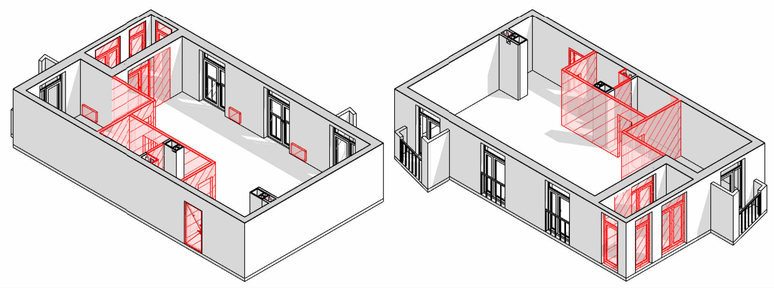

IVANCHUKINTERIOR

НАИМЕНОВАНИЕ ЧЕРТЕЖА / DRAWING TITLE

ПЛАН ДЕМОНТАЖА

№ ЛИСТА/ DRAWING NO	3	ВЫПОЛНИЛ/ DRAWN BY	ИВАНЧУК А.Ю.
		ДАТА/ DATE	13.02.2026
		ГОРОД/ CITY	МИНСК

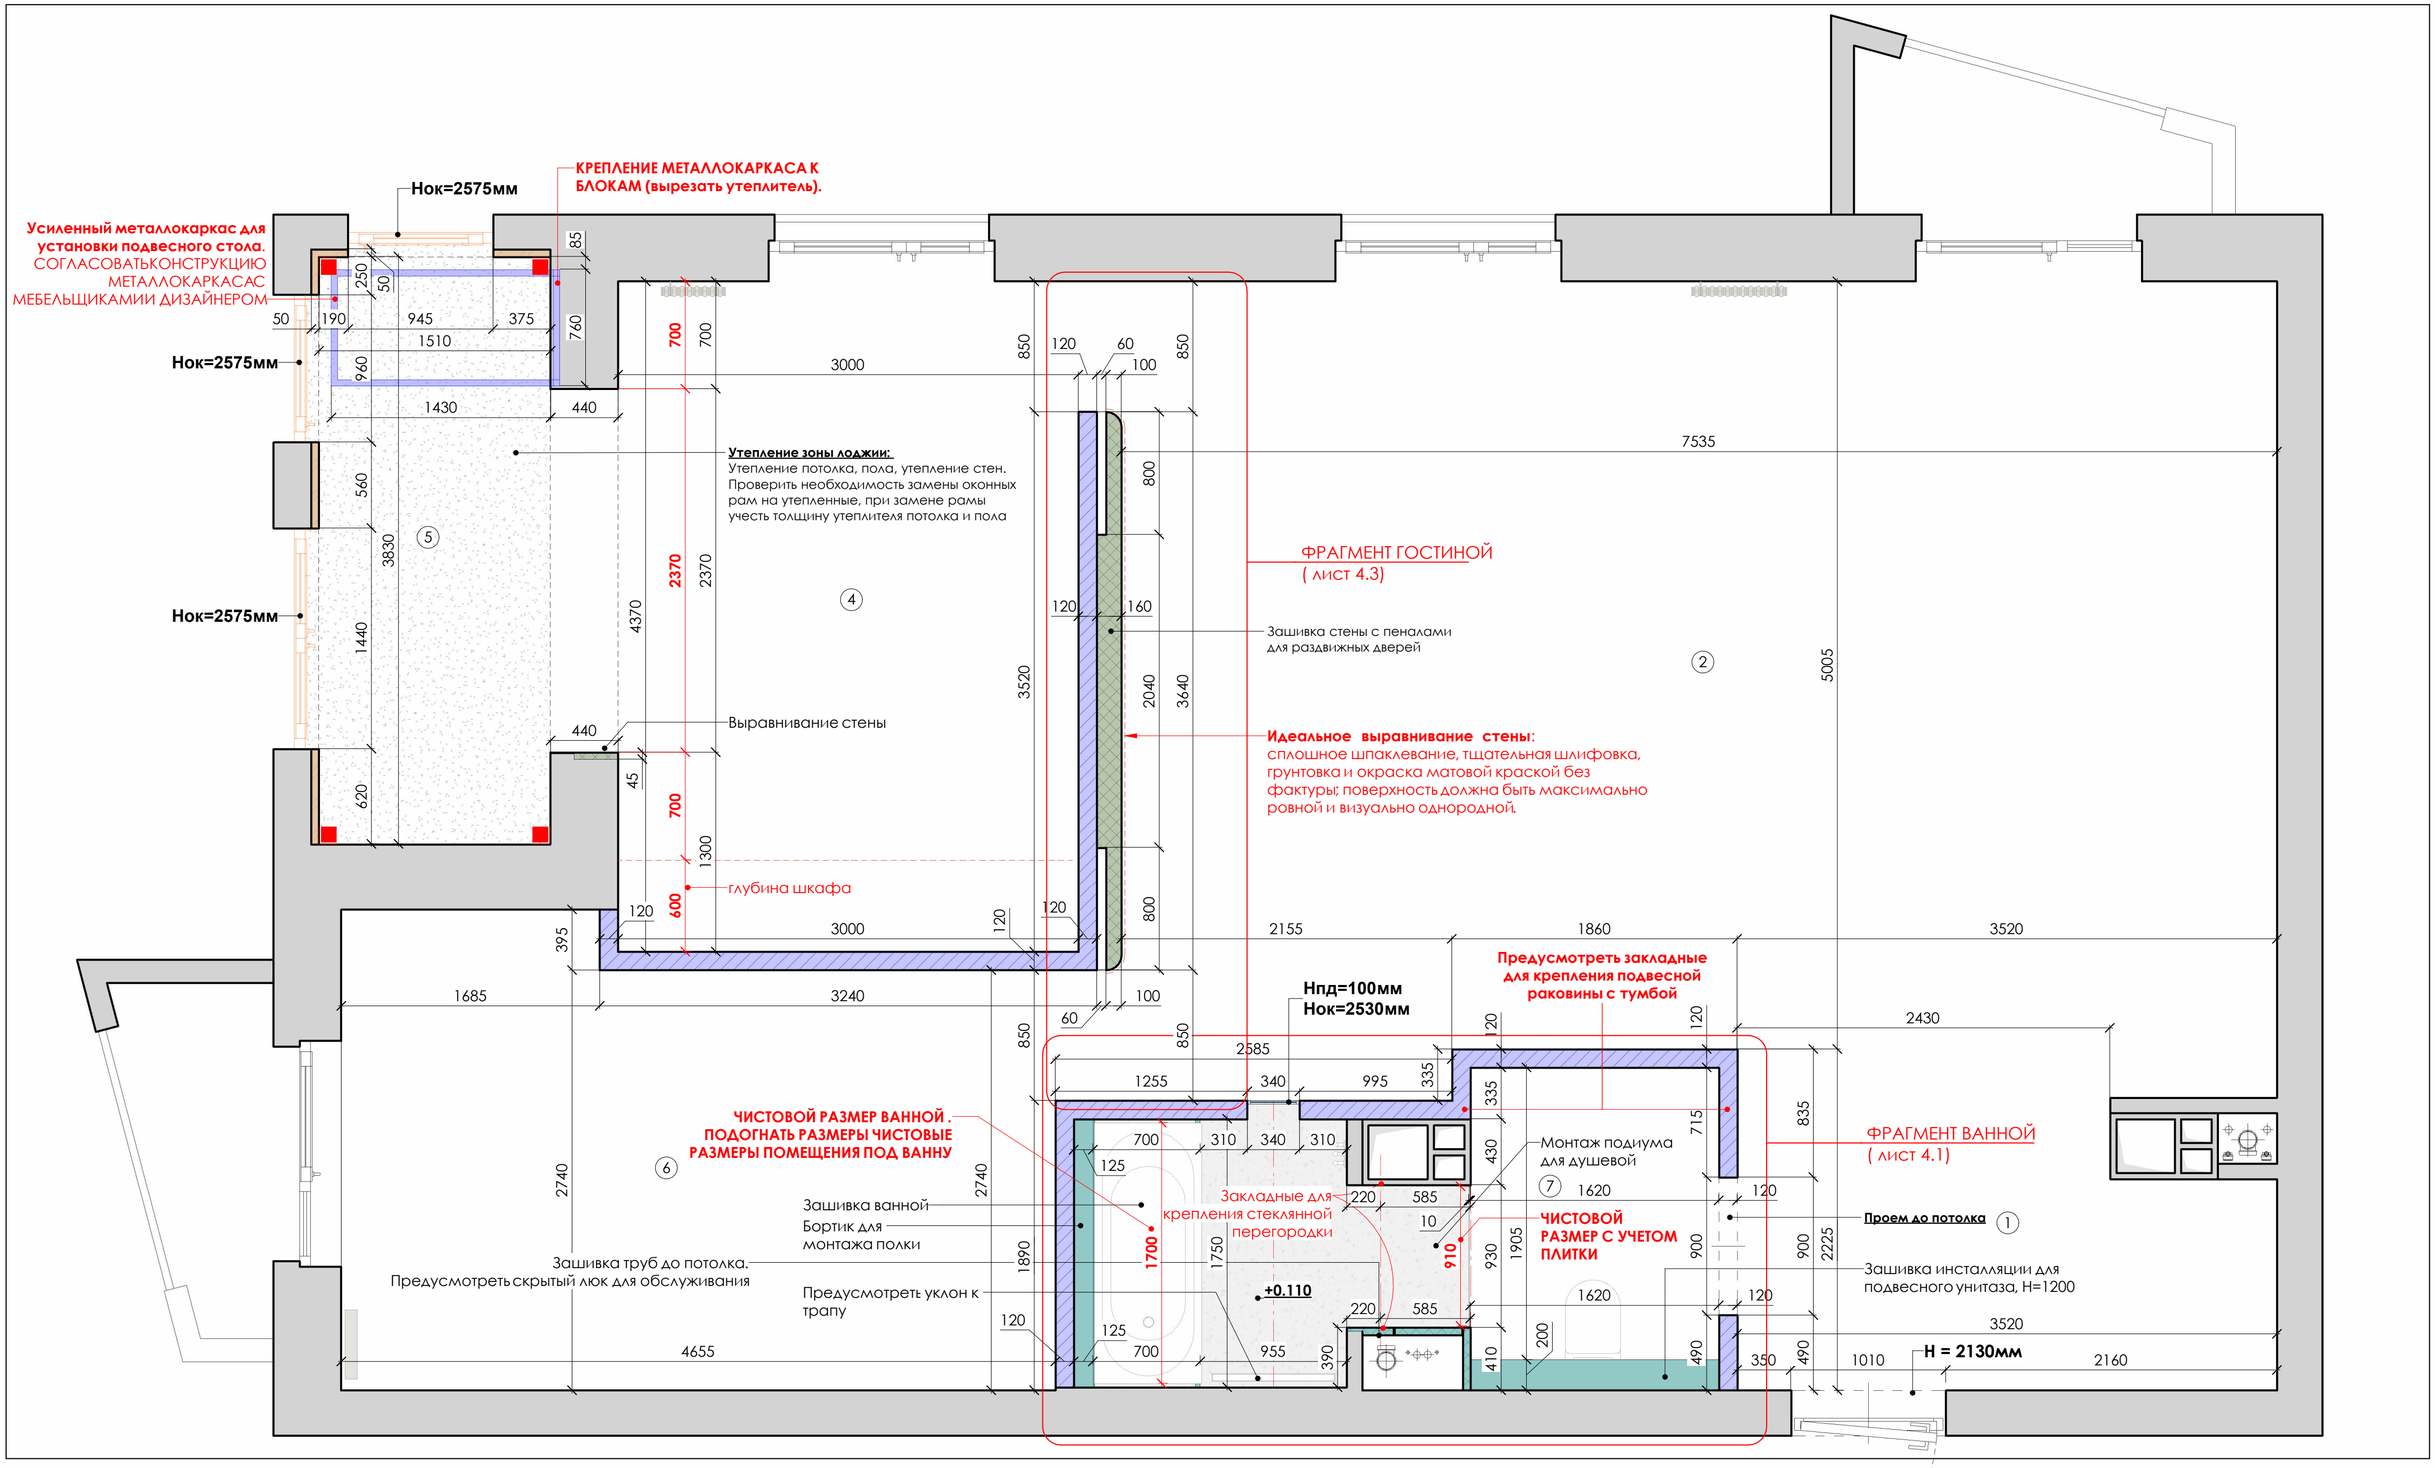

Примечания:

- Искажение чистовых размеров недопустимо;
- Все размеры сверять по факту;
- Перед возведением перегородок провести предварительную разметку в один ряд блока;
- При расхождении размеров на чертежах - связаться с автором проекта;
- **Размеры указаны с учетом штукатурки на существующих стенах и вновь возводимых** ;
- При проведении монтажных работ в ванной комнате произвести дополнительную гидроизоляцию пола;
- Выровнять существующе стены и перегородки, все оконные откосы и сущ.проемы;
- Материал перегородок согласовать перед монтажом;
- Вопросы согласовать с заказчиком или представителем авторского надзора;
- Лист 4 смотреть совместно с листом 4.1, 4.2.

Спецификация перегородок

УГО	Описание	S, кв.м.
	Перегородки из блоков	40 m²
	Возводимые конструкции из ГКЛ	11 m²
	Возводимые конструкции из ГКЛВ	8 m²
	Утеплитель	6 m²

Условные обозначения:

- (1) - марка обозначения помещений
- - существующие стены
- - радиатор отопления
- - шахта
- - канализация, хол. , гор. водоснабжение

Экспликация помещений

№	Наименование	S, кв.м.
1	Прихожая	6.90
2	Кухня-гостиная	39.75
4	Спальня	14.10
5	Лоджия	6.70
6	Детская	14.00
7	Ванная	7.25
		88.70

IVANCHUKINTERIOR

НАИМЕНОВАНИЕ ЧЕРТЕЖА / DRAWING TITLE

ПЛАН ВОЗВОДИМЫХ ПЕРЕГОРОДОК И КОНСТРУКЦИЙ

№ ЛИСТА/ DRAWING NO	4	ВЫПОЛНИЛ/ DRAWN BY	ИВАНЧУК А.Ю.
		ДАТА/ DATE	13.02.2026
		ГОРОД/ CITY	МИНСК

ФРАГМЕНТ ВАННОЙ

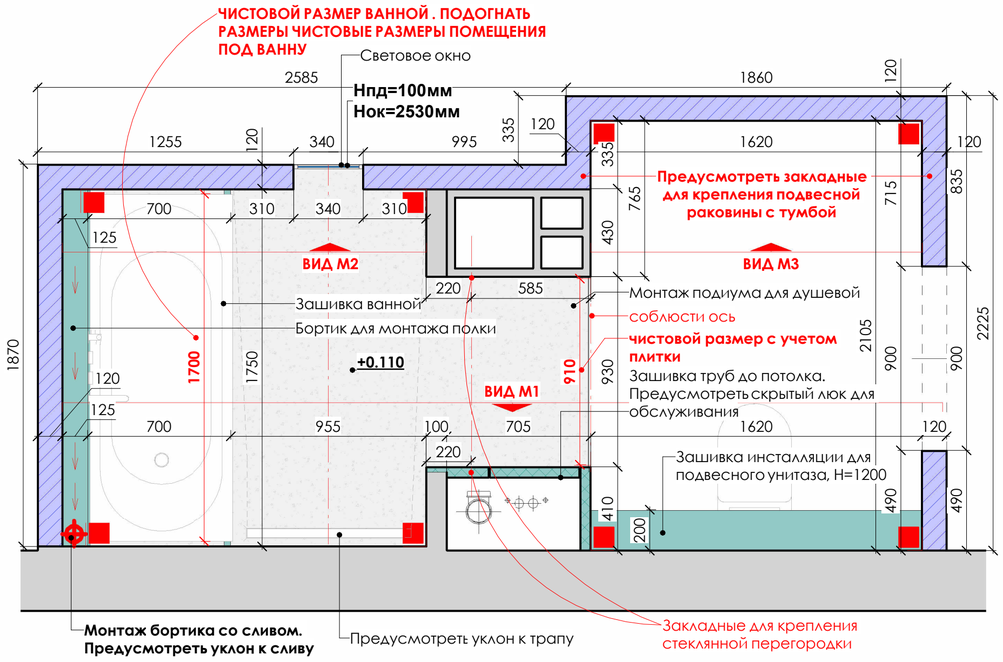

ВИД М2

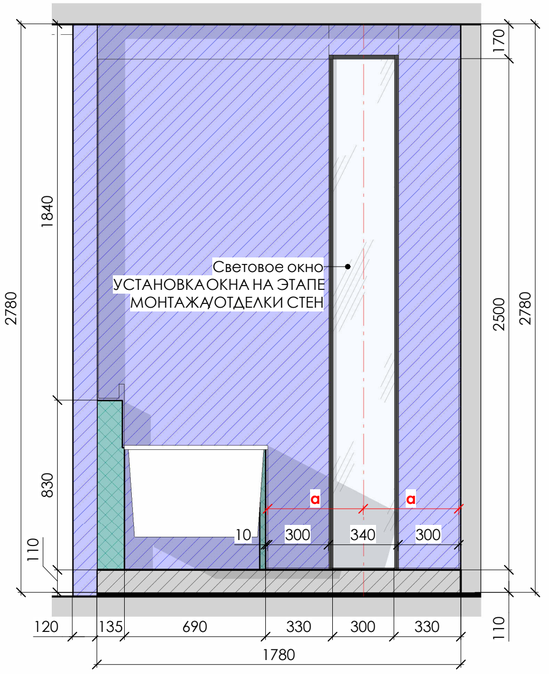

Сифон "клик-клак" на бортике

Подключение слива с полки выполнить через слив ванны: от сифона вывести прямой участок, далее сделать раздвоение, в одну ветку подключить перелив ванны, во вторую — слив с полки через гофру.

Согласовать схему подключения с сантехником на месте

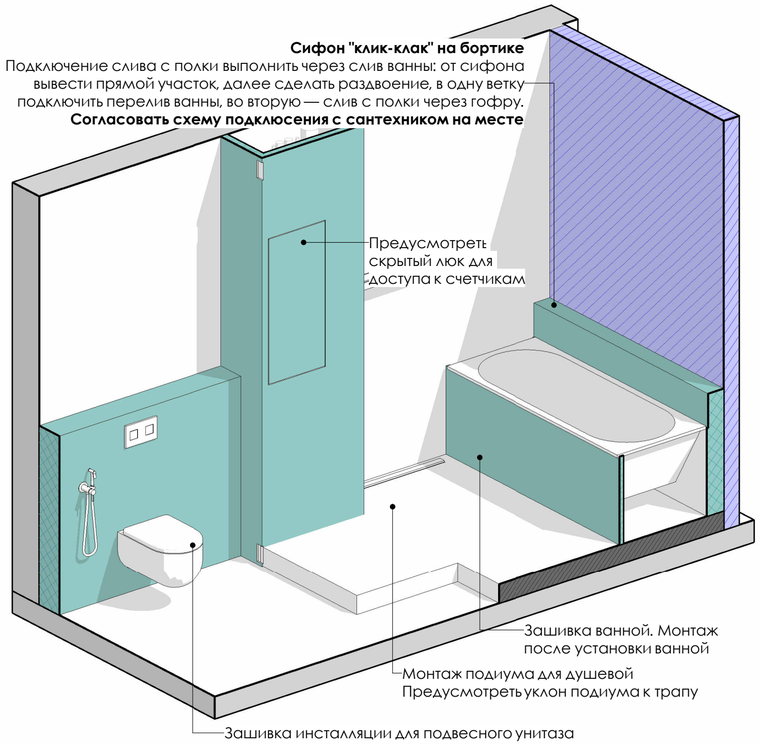

ВИД М1

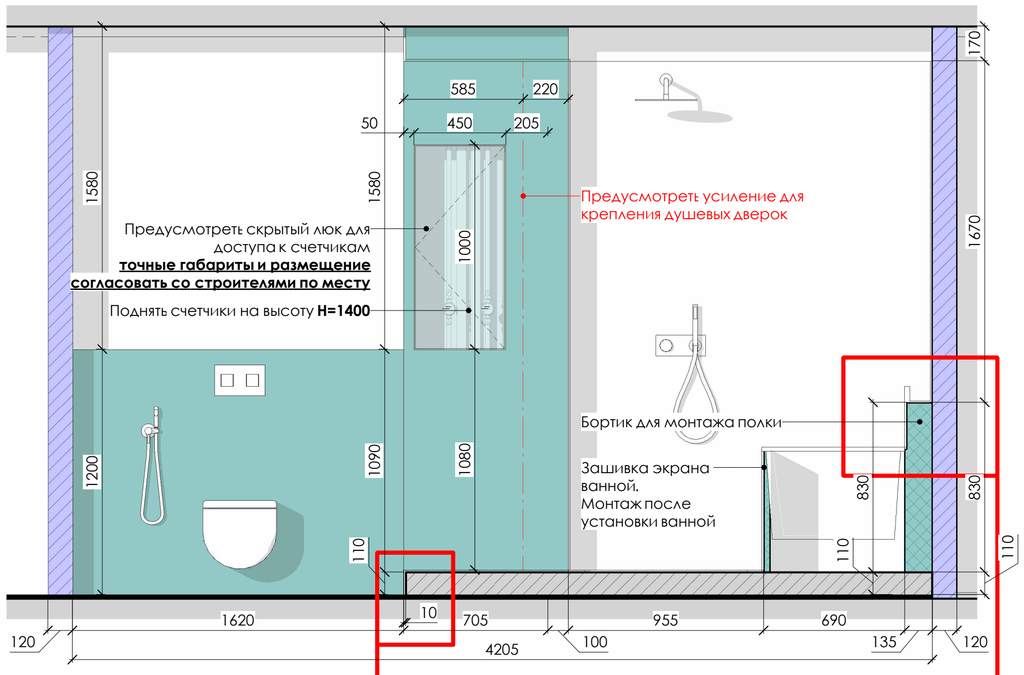

ВИД М3

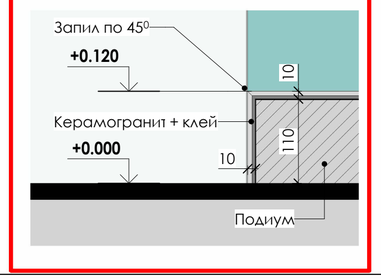

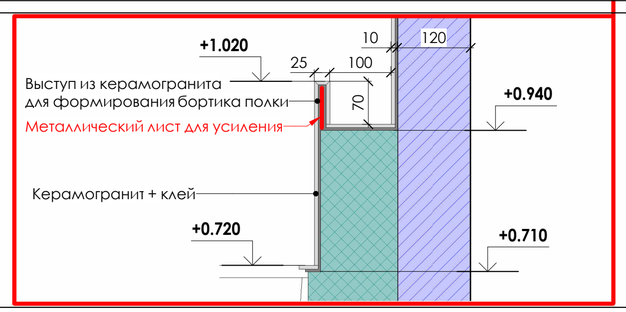

Условные обозначения:

- Существующие перегородки
- Возводимые перегодки из блоков
- Возводимые конструкции из ГКЛВ

Примечания:

- Смотреть совместно с листом 4, развертками и визуализациями помещений;
- Размеры уточнять по месту;
- Вопросы согласовать с заказчиком или представителем авторского надзора.

IVANCHUKINTERIOR

НАИМЕНОВАНИЕ ЧЕРТЕЖА / DRAWING TITLE

ФРАГМЕНТ ВАННОЙ

№ ЛИСТА/ DRAWING NO	4.1	ВЫПОЛНИЛ/ DRAWN BY	ИВАНЧУК А.Ю.
		ДАТА/ DATE	13.02.2026
		ГОРОД/ CITY	МИНСК

РАЗРЕЗ 1-1

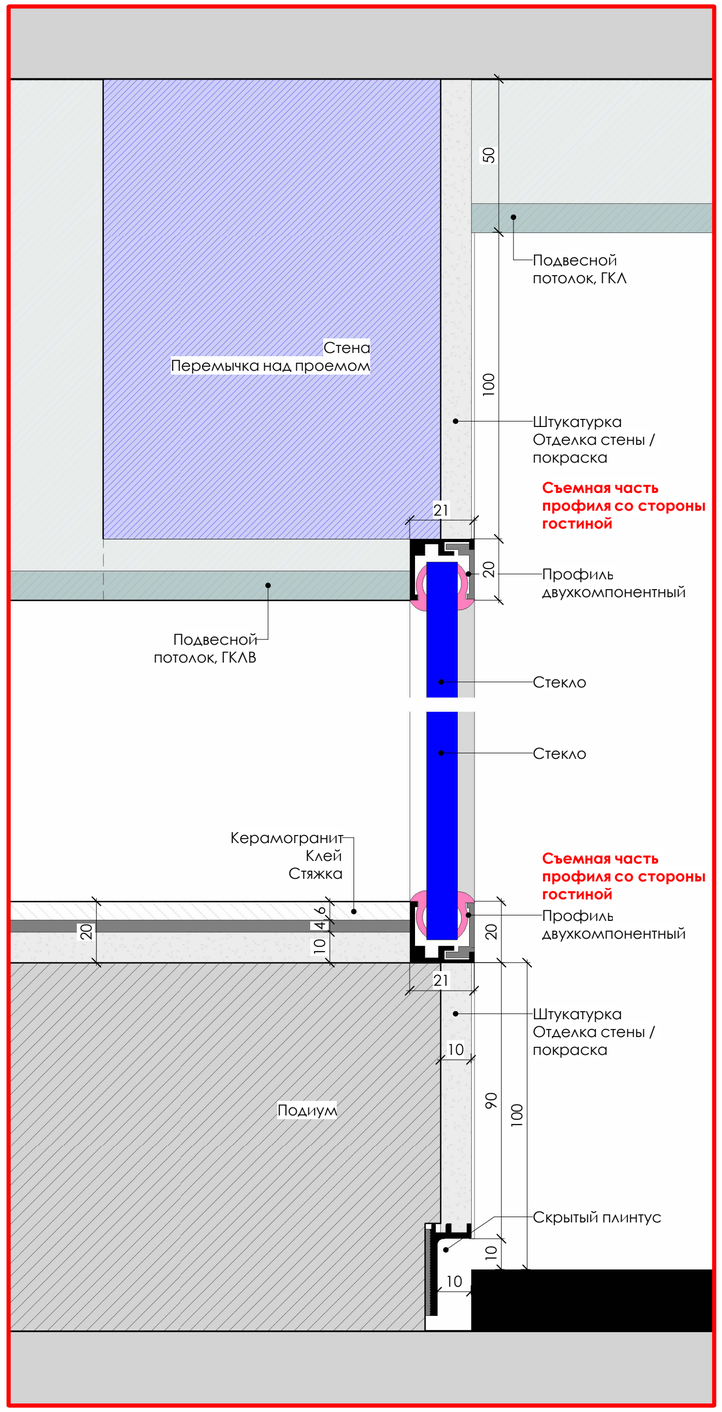

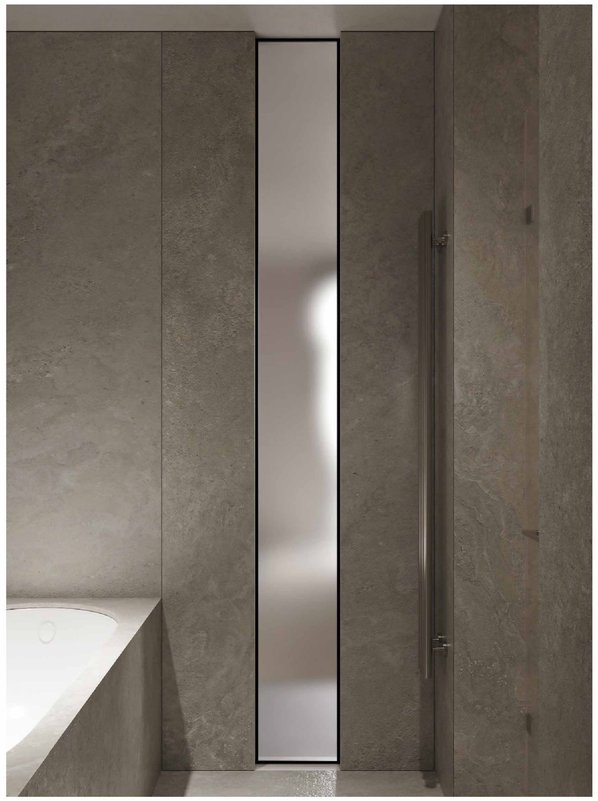

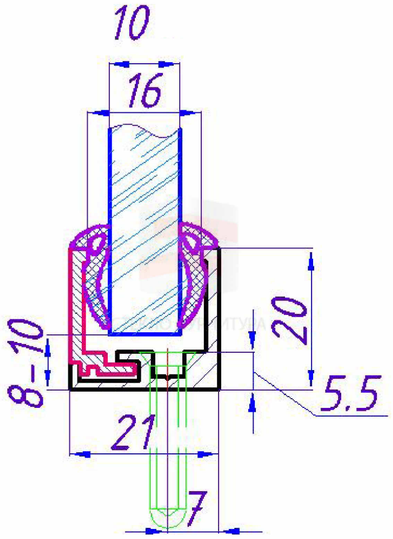

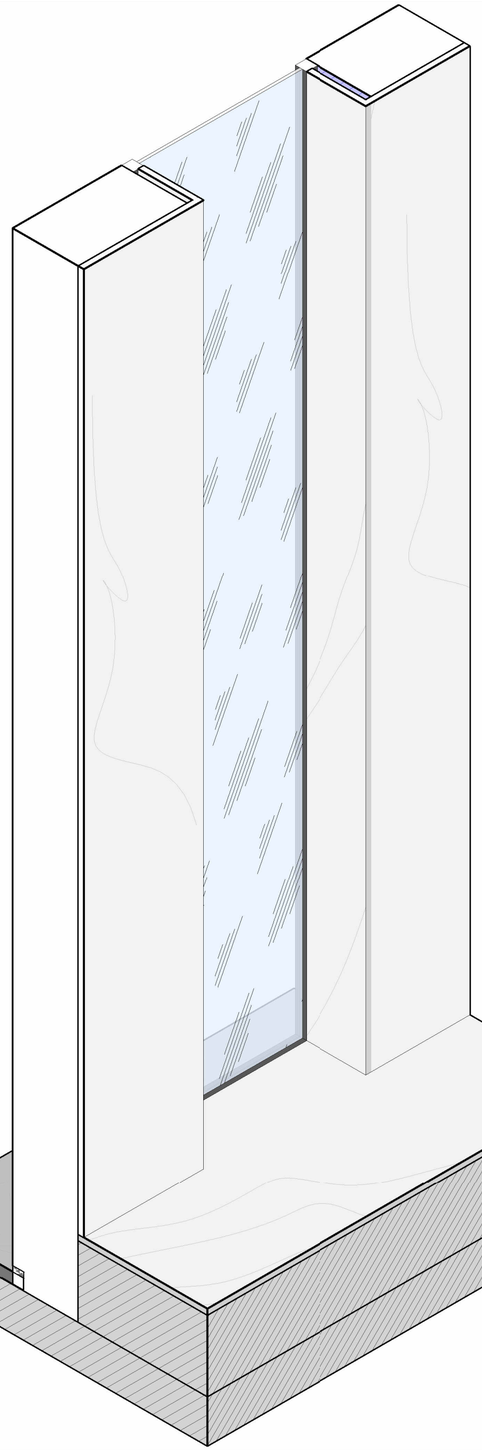

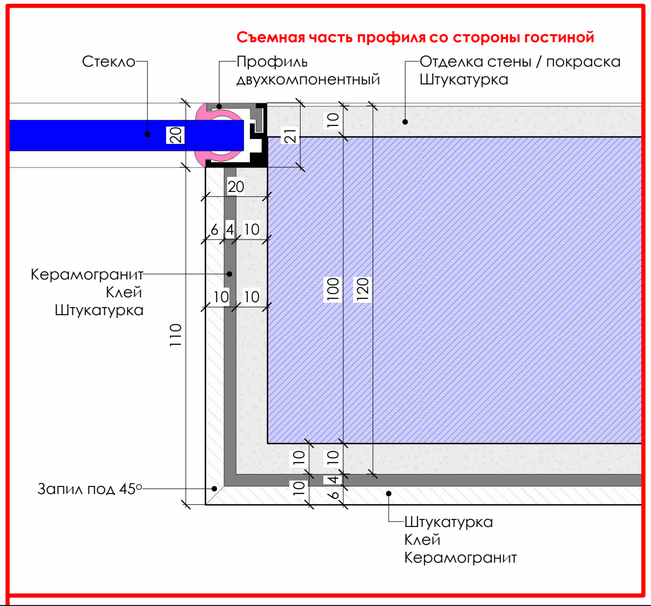

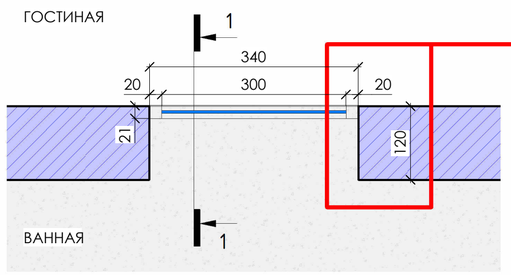

IVANCHUKINTERIOR

НАИМЕНОВАНИЕ ЧЕРТЕЖА / DRAWING TITLE

СХЕМА УСТАНОВКИ СТЕКЛА В ВАННОЙ

№ ЛИСТА/ DRAWING NO	4.2	ВЫПОЛНИЛ/ DRAWN BY	ИВАНЧУК А.Ю.
		ДАТА/ DATE	13.02.2026
		ГОРОД/ CITY	МИНСК

ФРАГМЕНТ ГОСТИНОЙ

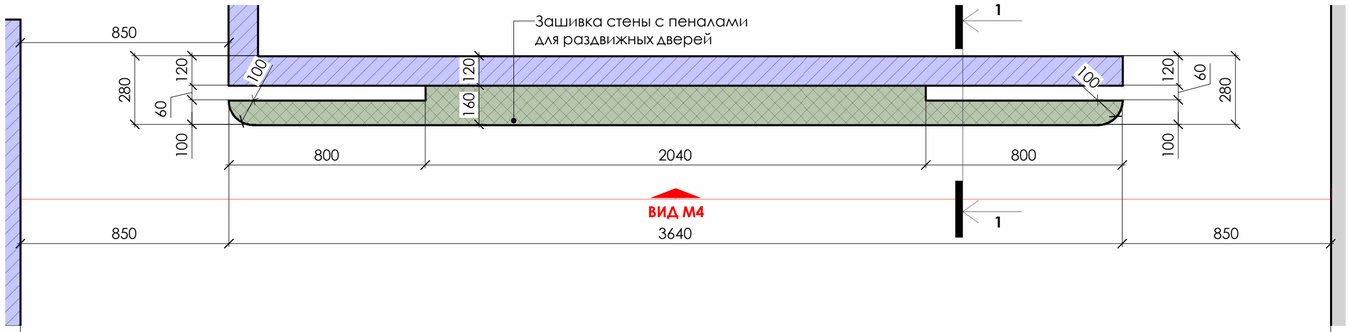

ВИД М4

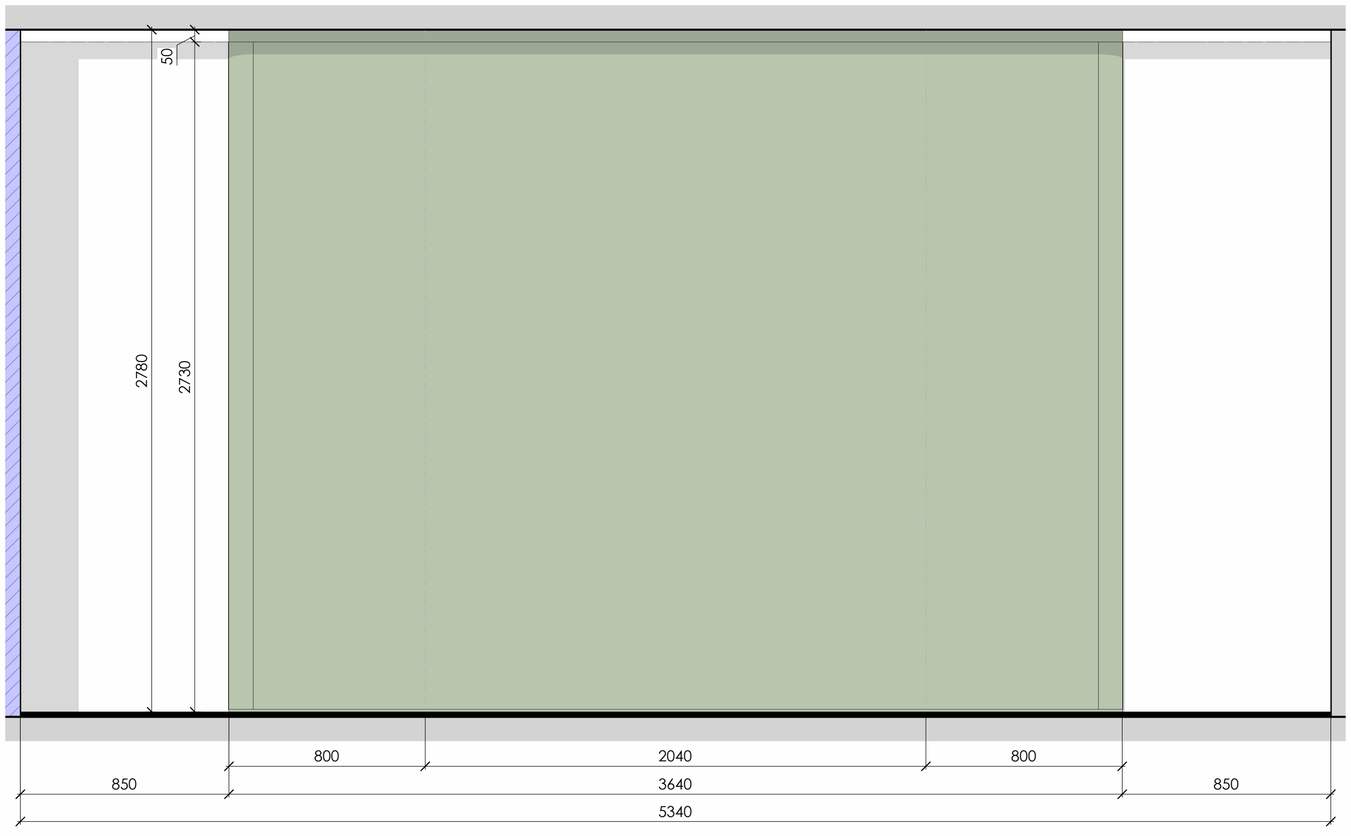

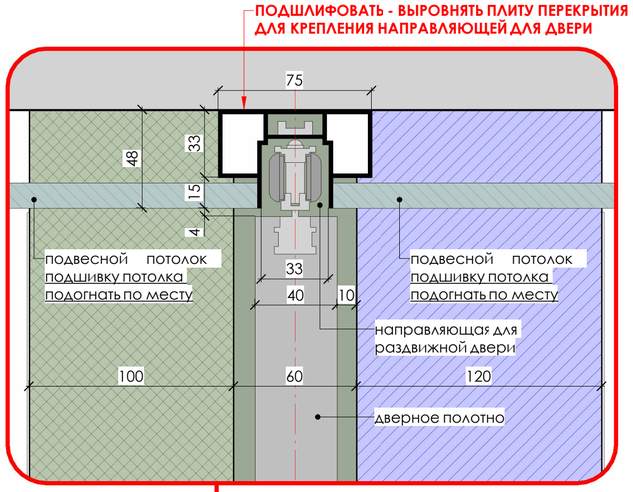

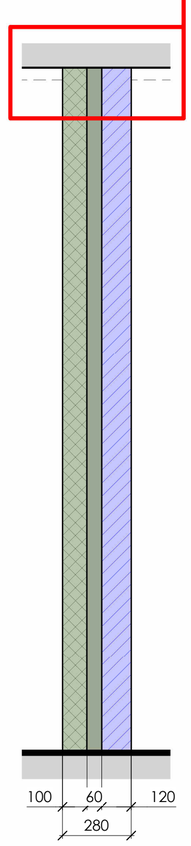

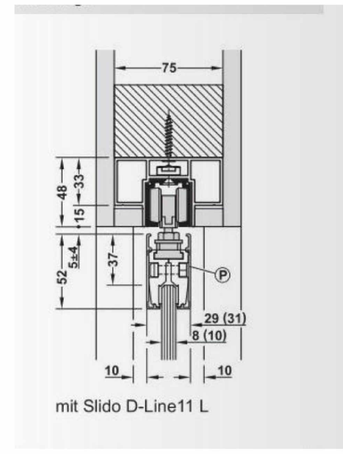

mit Slido D-Line11 L

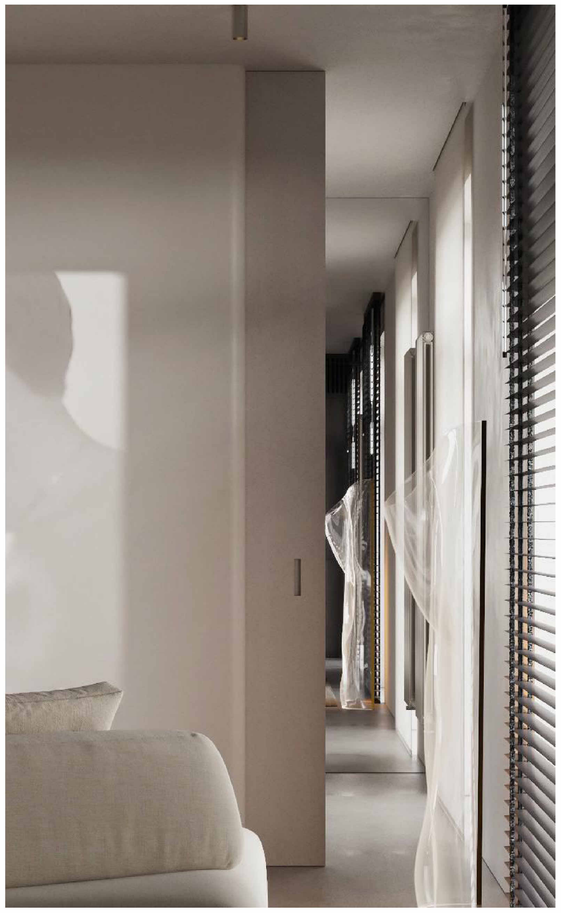

Условные обозначения:

- Существующие перегородки
- Возводимые конструкции из ГКЛ
- Возводимые перегородки из блоков

Примечания:

- Смотреть совместно с листом 4, развертками и визуализациями помещений;
- Размеры уточнять по месту;
- Вопросы согласовать с заказчиком или представителем авторского надзора.

IVANCHUKINTERIOR

НАИМЕНОВАНИЕ ЧЕРТЕЖА / DRAWING TITLE

ФРАГМЕНТ ГОСТИНОЙ

№ ЛИСТА/ DRAWING NO	4.3	ВЫПОЛНИЛ/ DRAWN BY	ИВАНЧУК А.Ю.
		ДАТА/ DATE	13.02.2026
		ГОРОД/ CITY	МИНСК

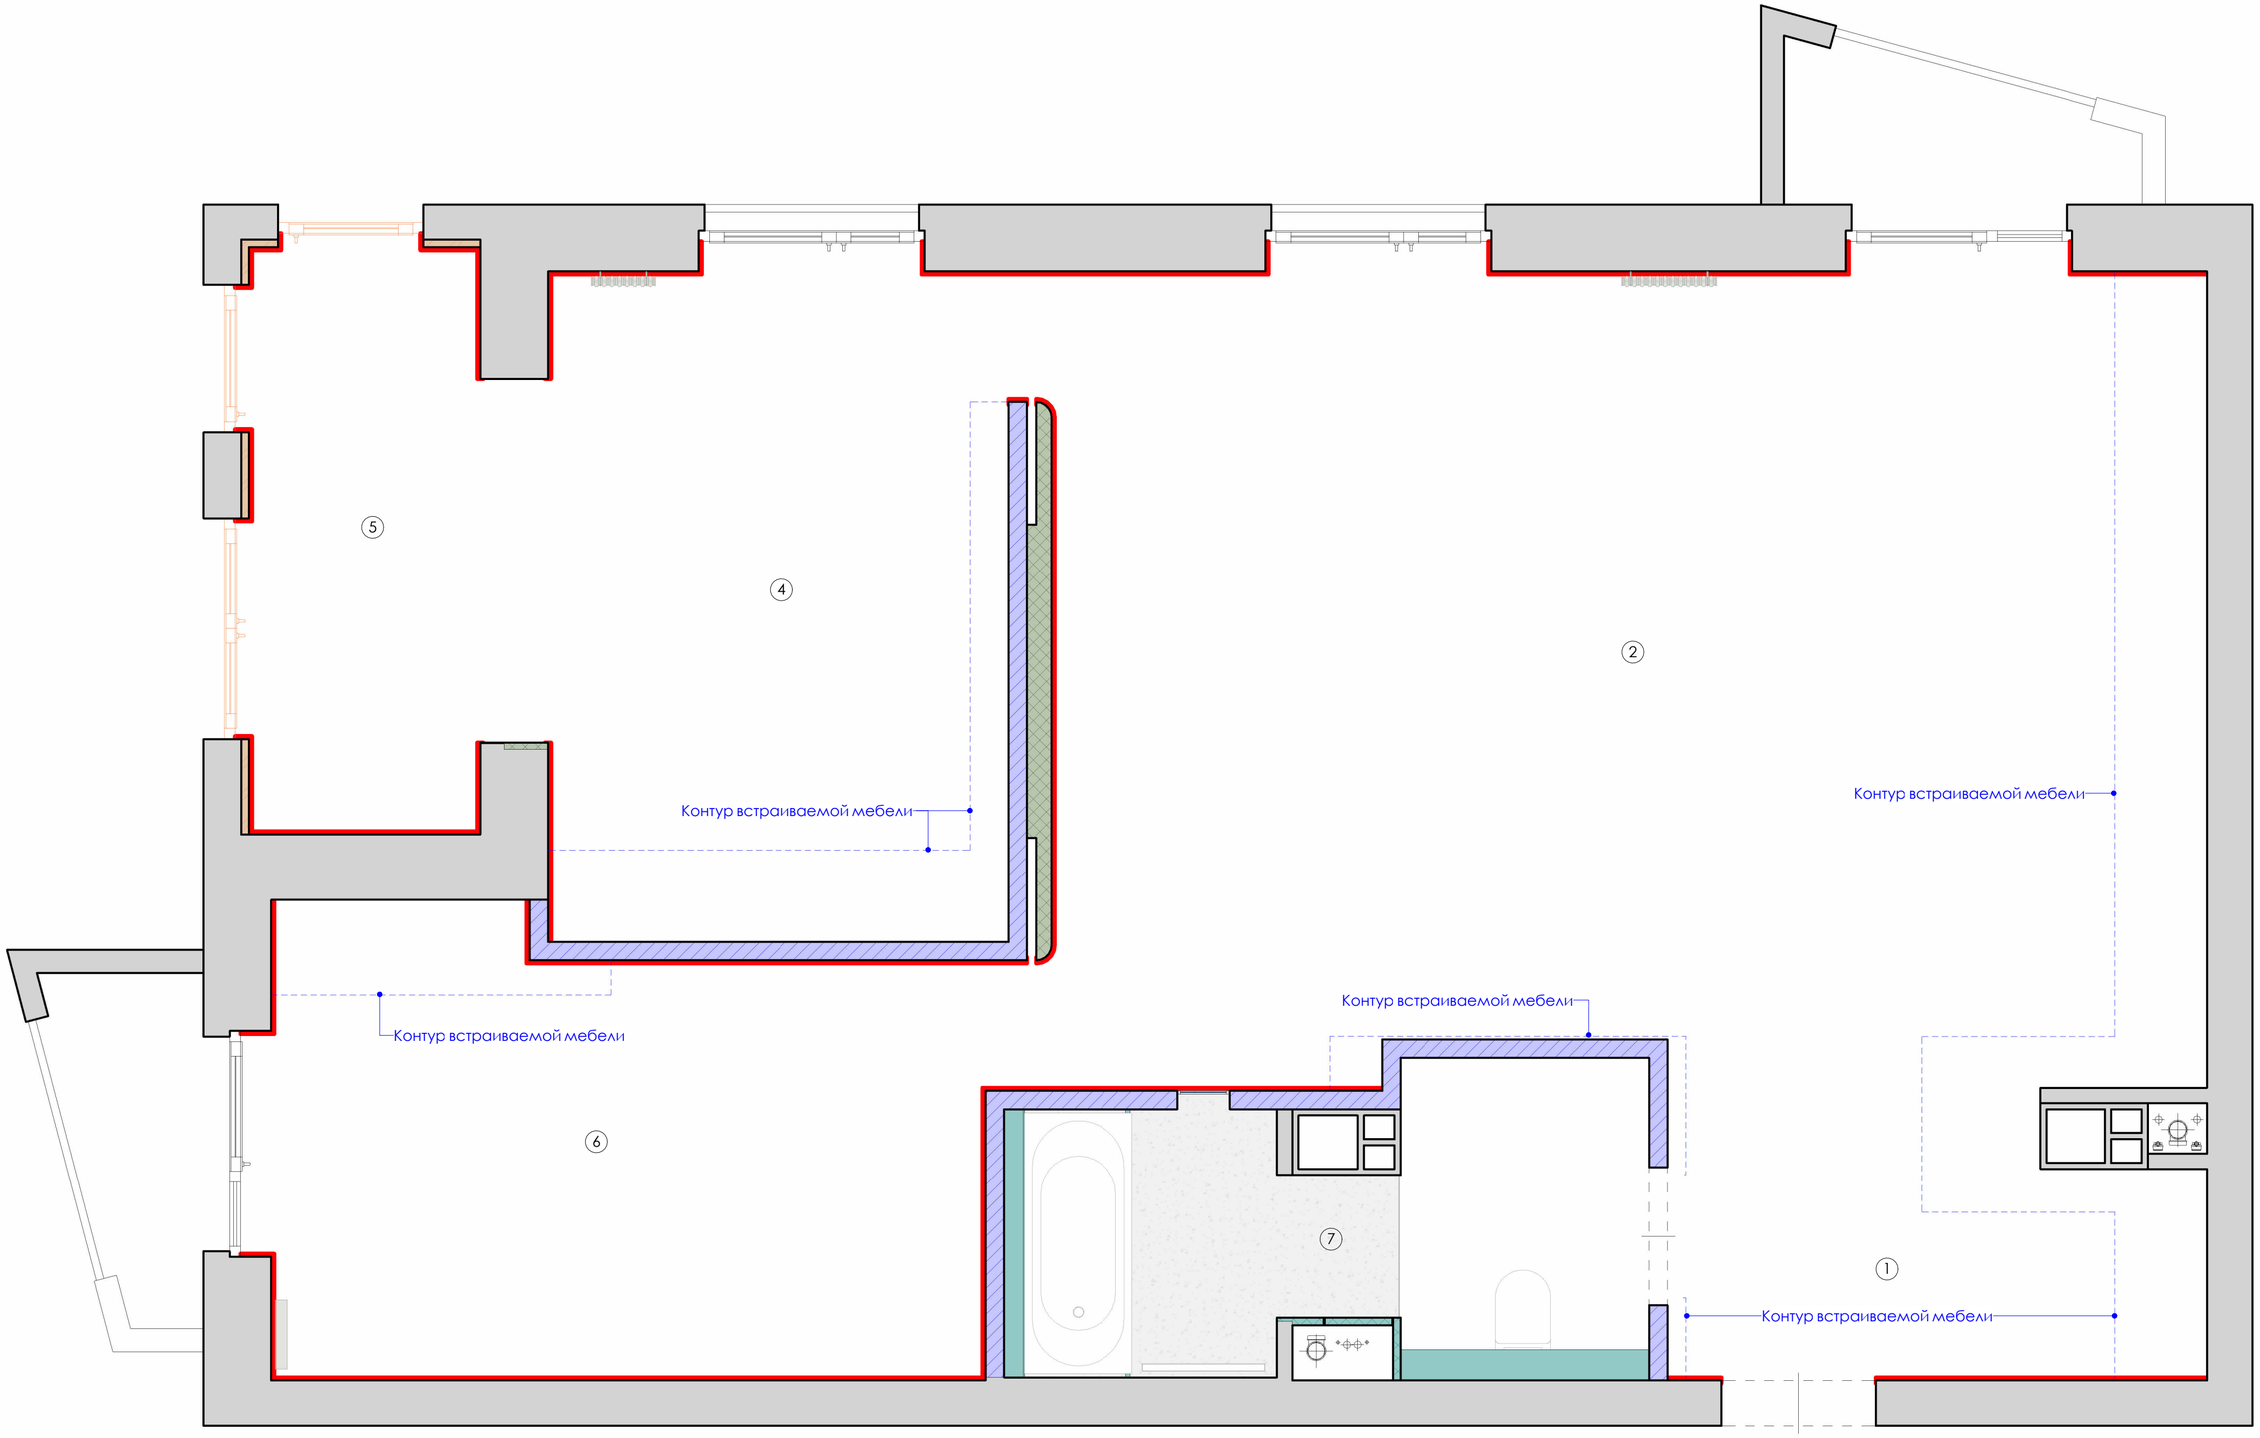

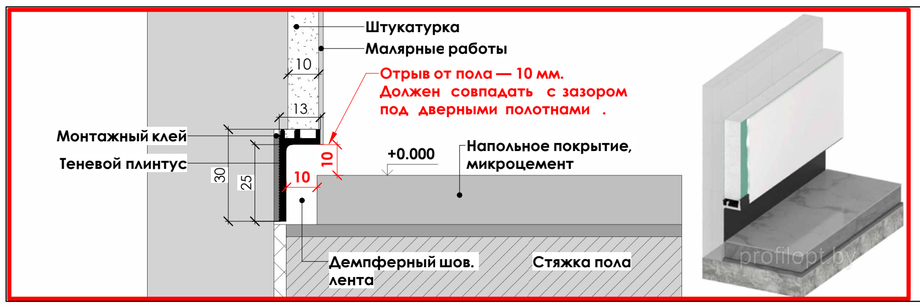

Спецификация скрытых плинтусов

УГО	Примечание	Длина, пог.м
	Плинтус теневой AUF-PROFILL 25 алюминиевый. Цвет:черный матовый	36.3

Экспликация помещений

№	Наименование	S, кв.м.
1	Прихожая	6.90
2	Кухня-гостиная	39.75
4	Спальня	14.10
5	Лоджия	6.70
6	Детская	14.00
7	Ванная	7.25
		88.70

IVANCHUKINTERIOR

НАИМЕНОВАНИЕ ЧЕРТЕЖА / DRAWING TITLE

СХЕМА УСТАНОВКИ СКРЫТЫХ ПЛИНТУСОВ

№ ЛИСТА/ DRAWING NO: 4.4

ВЫПОЛНИЛ/ DRAWN BY	ИВАНЧУК А.Ю.
ДАТА/ DATE	13.02.2026
ГОРОД/ CITY	МИНСК

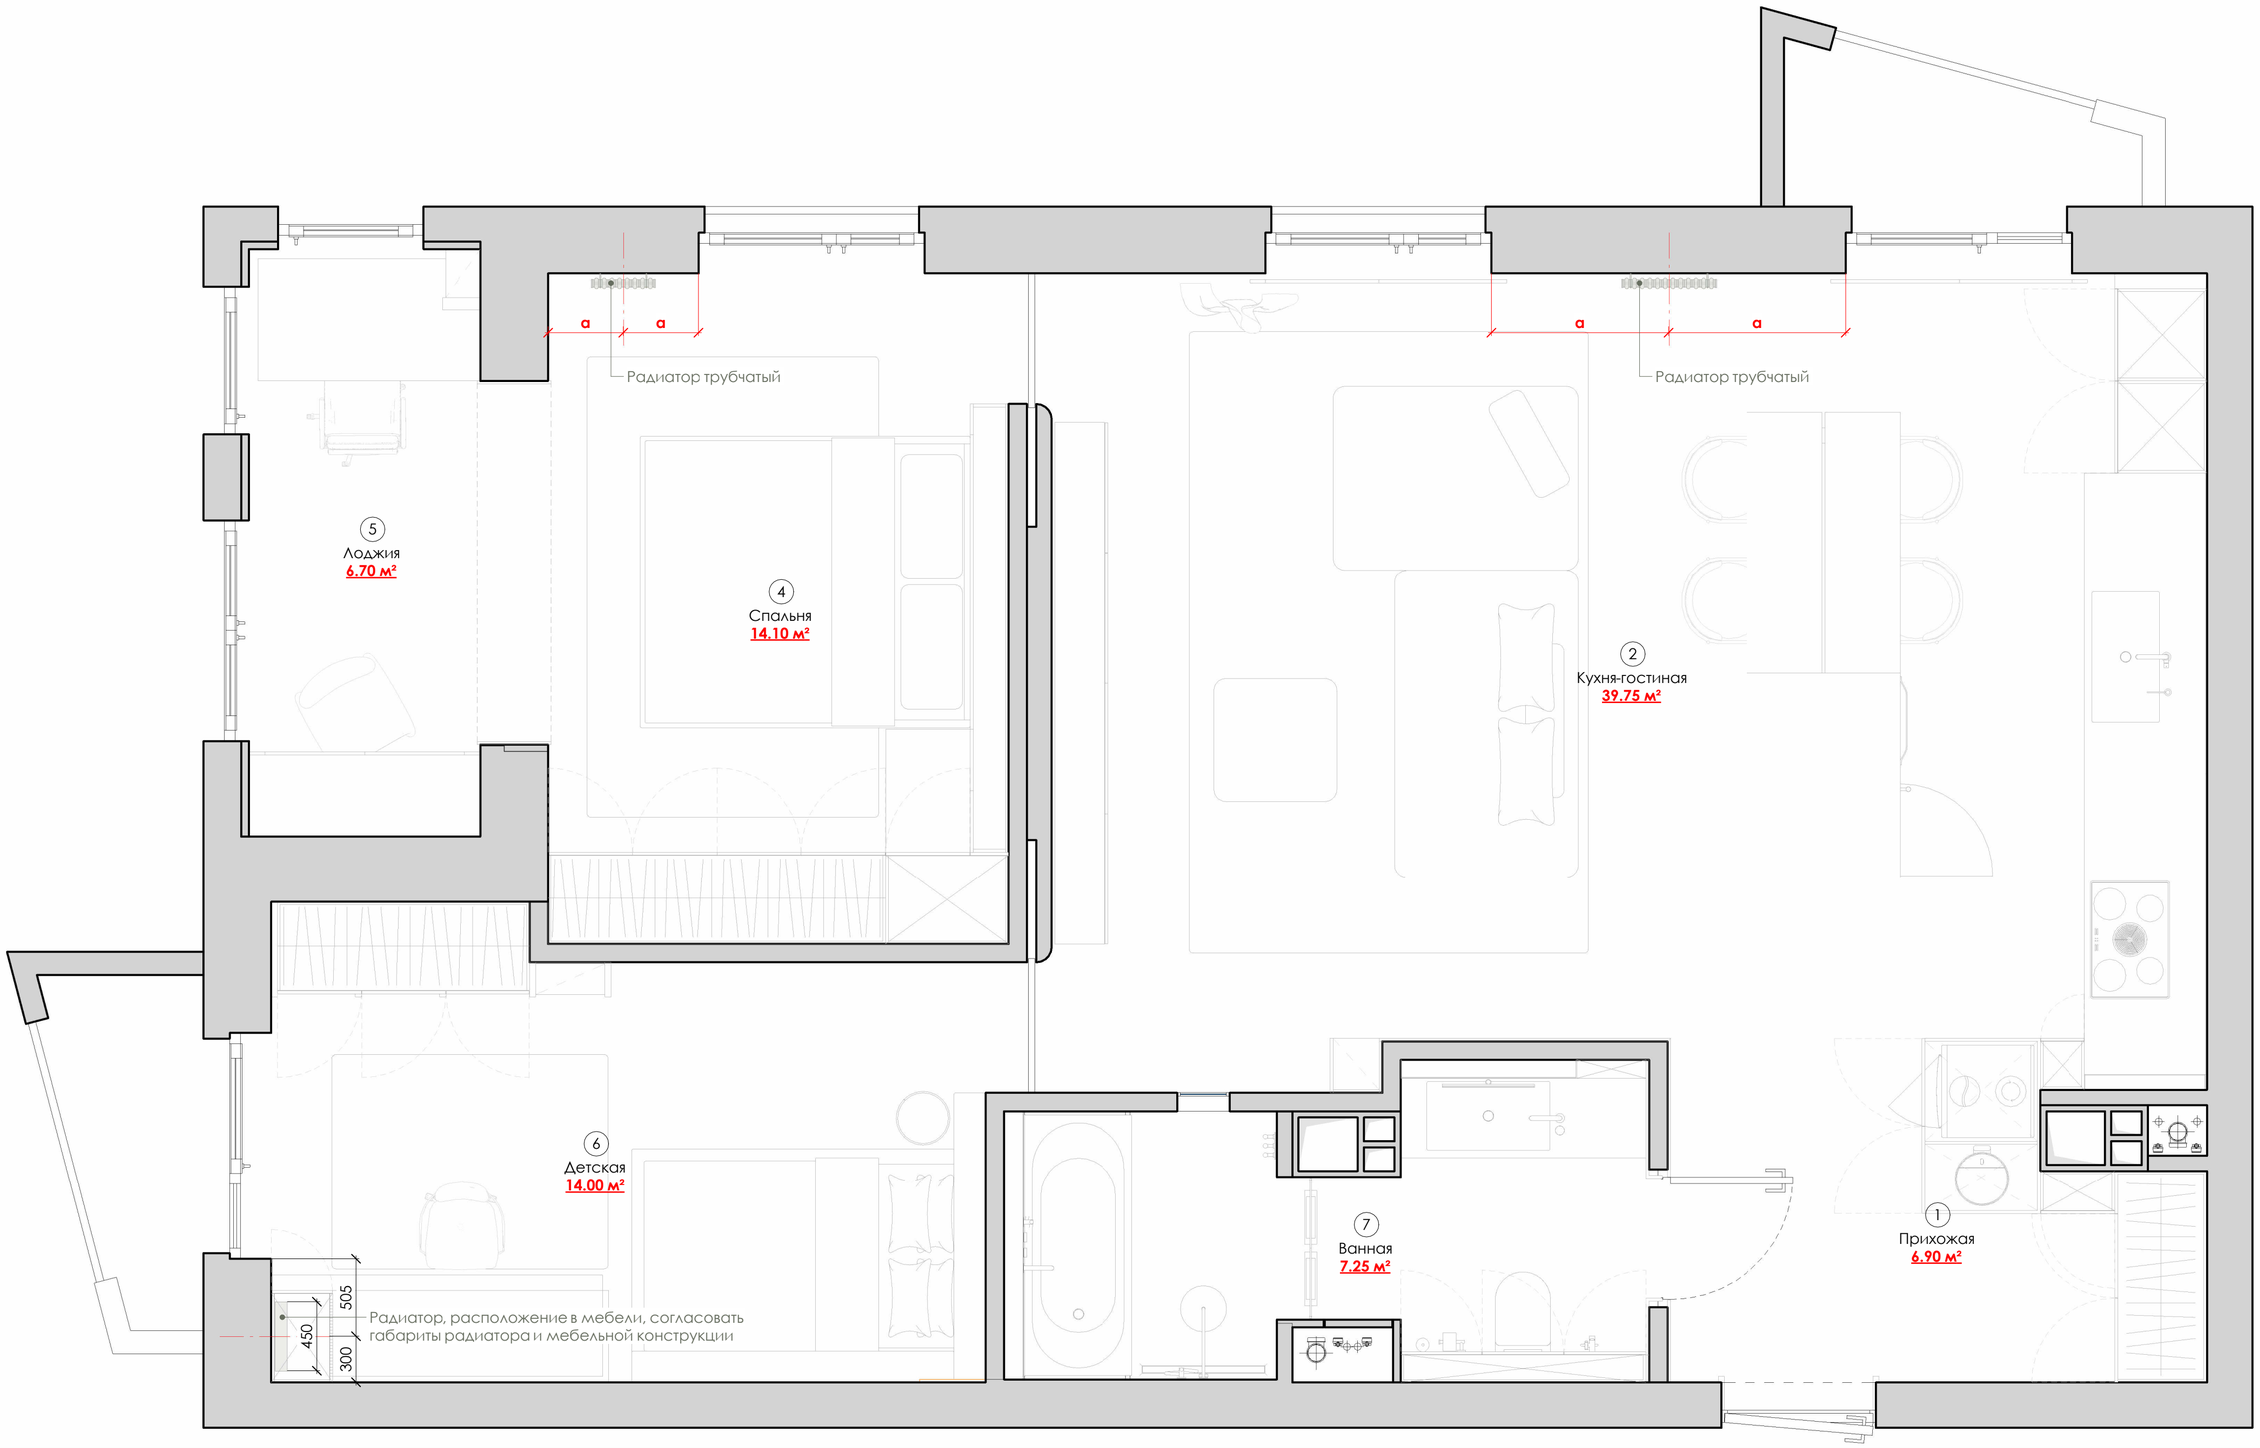

Условные обозначения:

- (1) - марка обозначения помещений
- - существующие стены
- - радиатор отопления
- - шахта
- - канализация, хол. , гор. водоснабжение

Примечания:

- За отметку 0.000 принята отметка чистого пола квартиры.
- Все размеры уточняются по месту.
- Вопросы согласовать с заказчиком или представителем авторского надзора

Экспликация помещений

№	Наименование	S, кв.м.
1	Прихожая	6.90
2	Кухня-гостиная	39.75
4	Спальня	14.10
5	Лоджия	6.70
6	Детская	14.00
7	Ванная	7.25
		88.70

IVANCHUKINTERIOR

НАИМЕНОВАНИЕ ЧЕРТЕЖА / DRAWING TITLE

ПЛАН-СХЕМА ОТОПИТЕЛЬНЫХ ПРИБОРОВ

№ ЛИСТА/ DRAWING NO: 5

ВЫПОЛНИЛ/ DRAWN BY	ИВАНЧУК А.Ю.
ДАТА/ DATE	13.02.2026
ГОРОД/ CITY	МИНСК

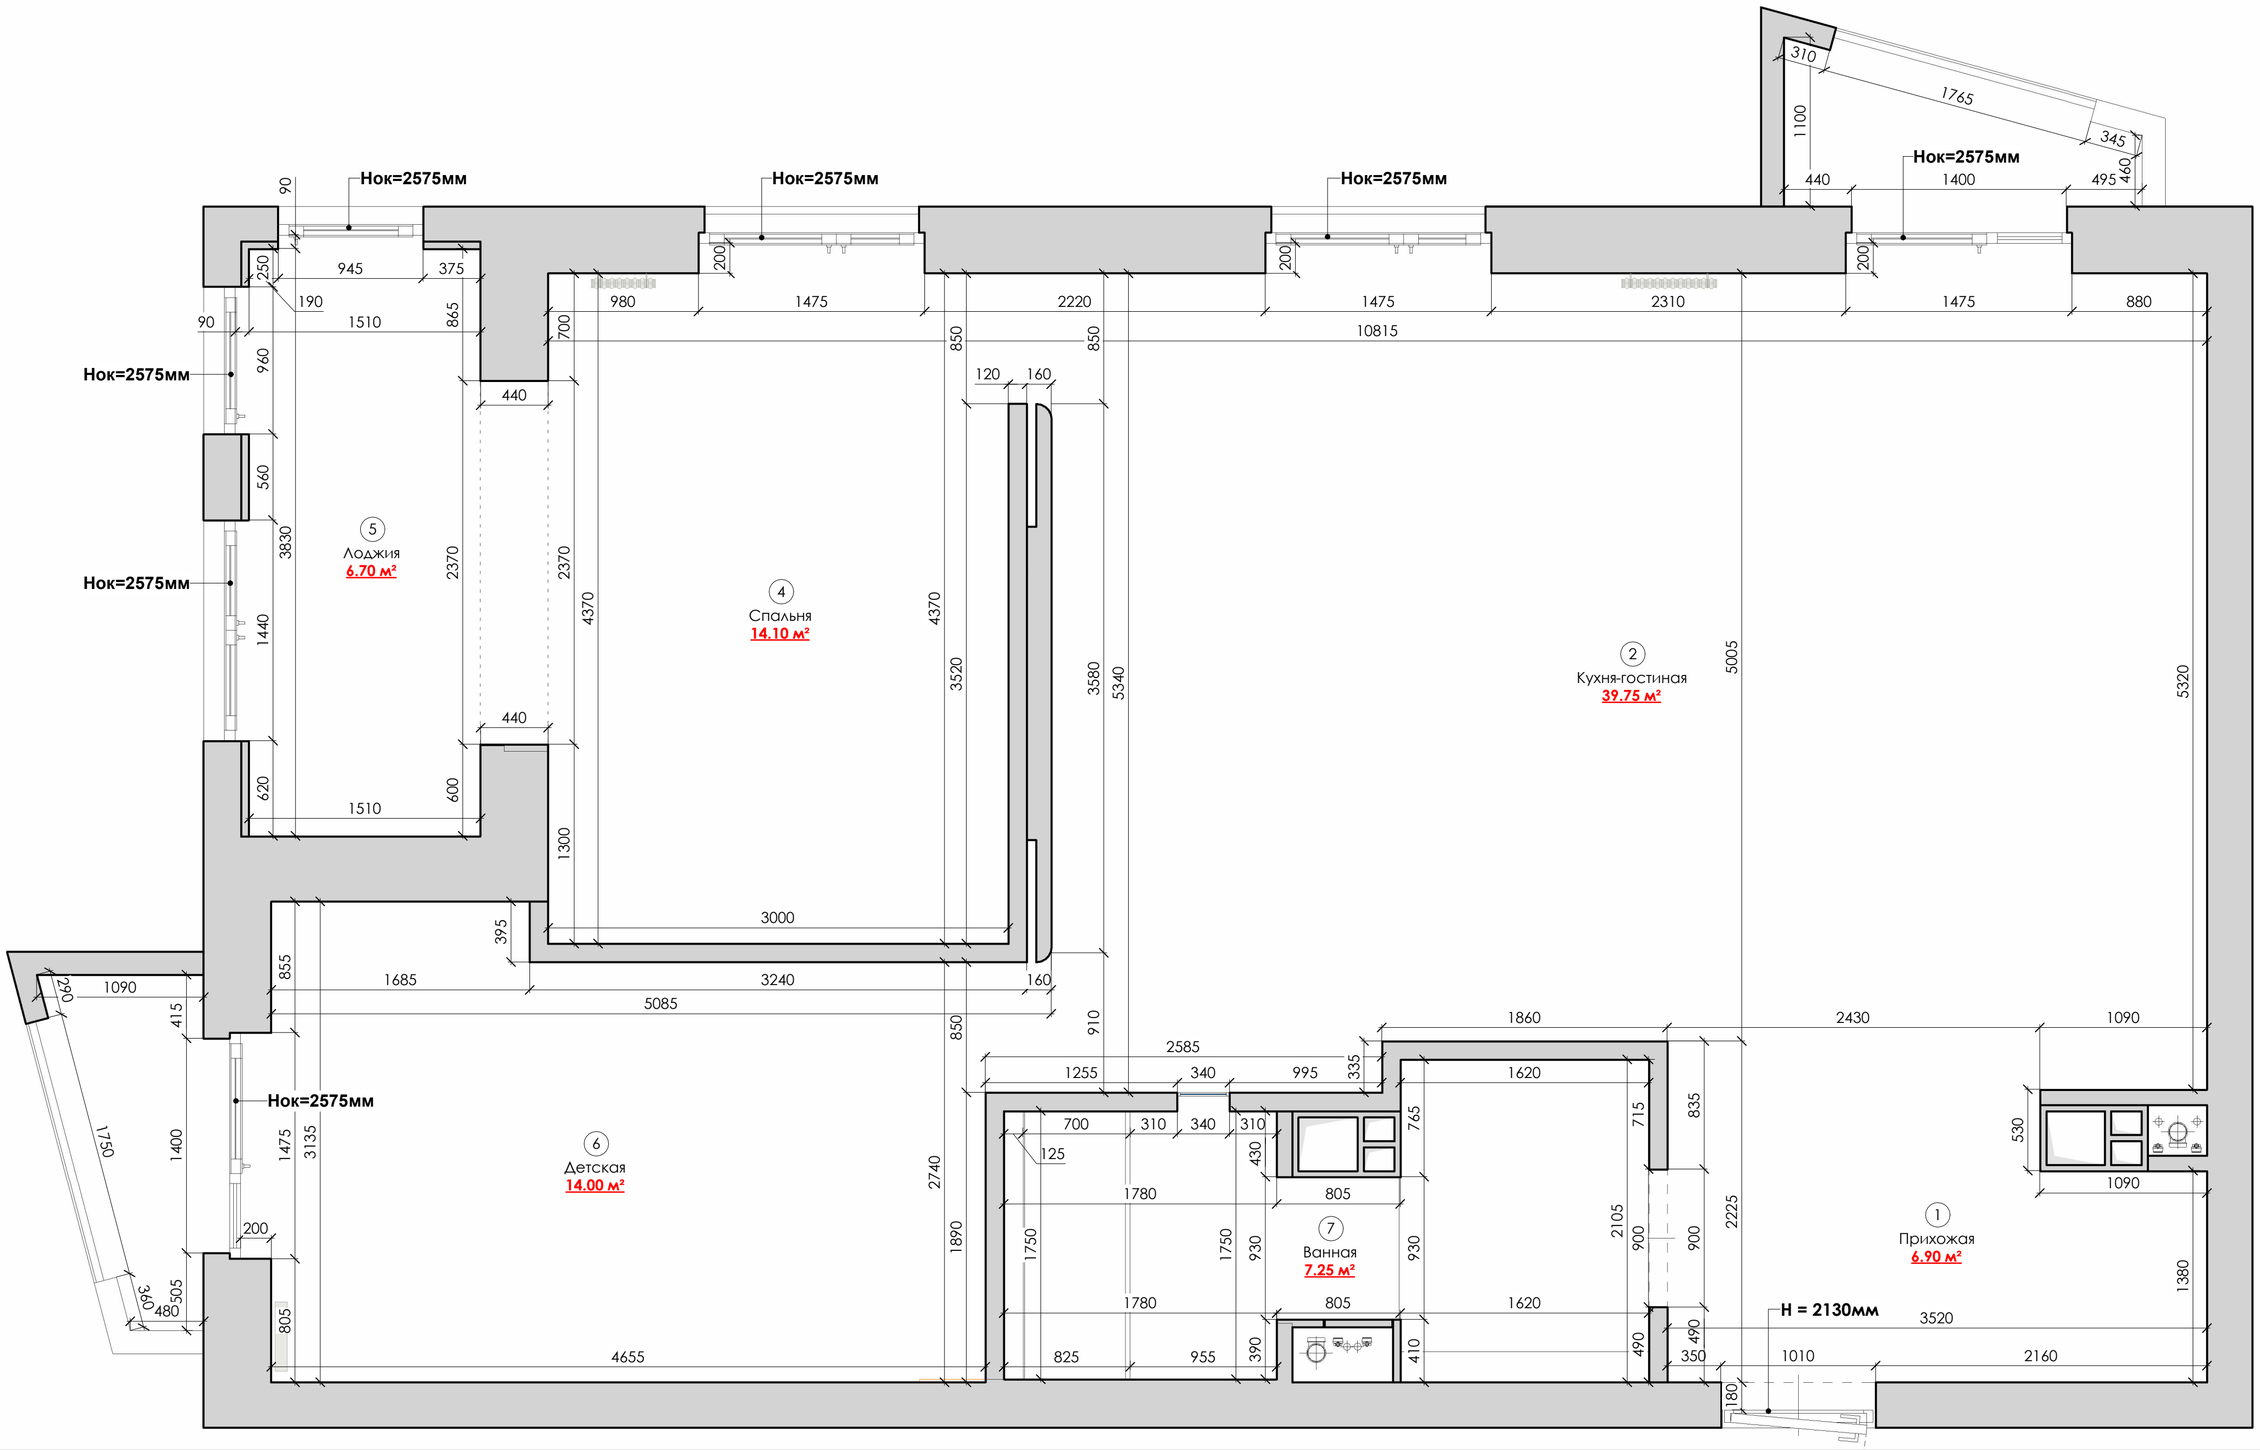

Условные обозначения:

1 - марка обозначения помещений

- существующие стены
- радиатор отопления
- шахта
- канализация, хол. , гор. водоснабжение

Примечания:

• Все размеры уточнить по месту;
• Данный план НЕ ЯВЛЯЕТСЯ ОРИЕНТИРОМ ДЛЯ МОНТАЖА ПЕРЕГОРОДОК.
Все важные размеры указаны на плане МОНТАЖА

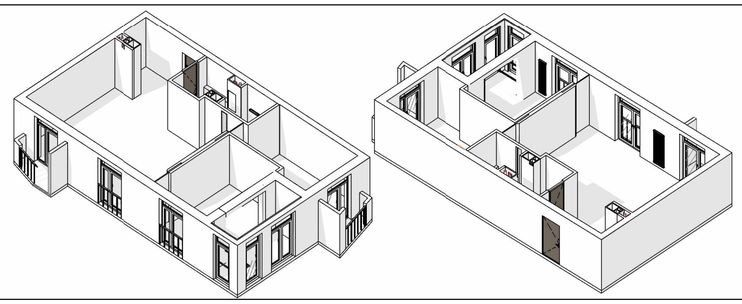

Экспликация помещений

№	Наименование	S, кв.м.
1	Прихожая	6.90
2	Кухня-гостиная	39.75
4	Спальня	14.10
5	Лоджия	6.70
6	Детская	14.00
7	Ванная	7.25
		88.70

IVANCHUKINTERIOR

НАИМЕНОВАНИЕ ЧЕРТЕЖА / DRAWING TITLE

АРХИТЕКТУРНО-СТРОИТЕЛЬНЫЙ ПЛАН

№ ЛИСТА/ DRAWING NO: 6

ВЫПОЛНИЛ/ DRAWN BY	ИВАНЧУК А.Ю.
ДАТА/ DATE	13.02.2026
ГОРОД/ CITY	МИНСК

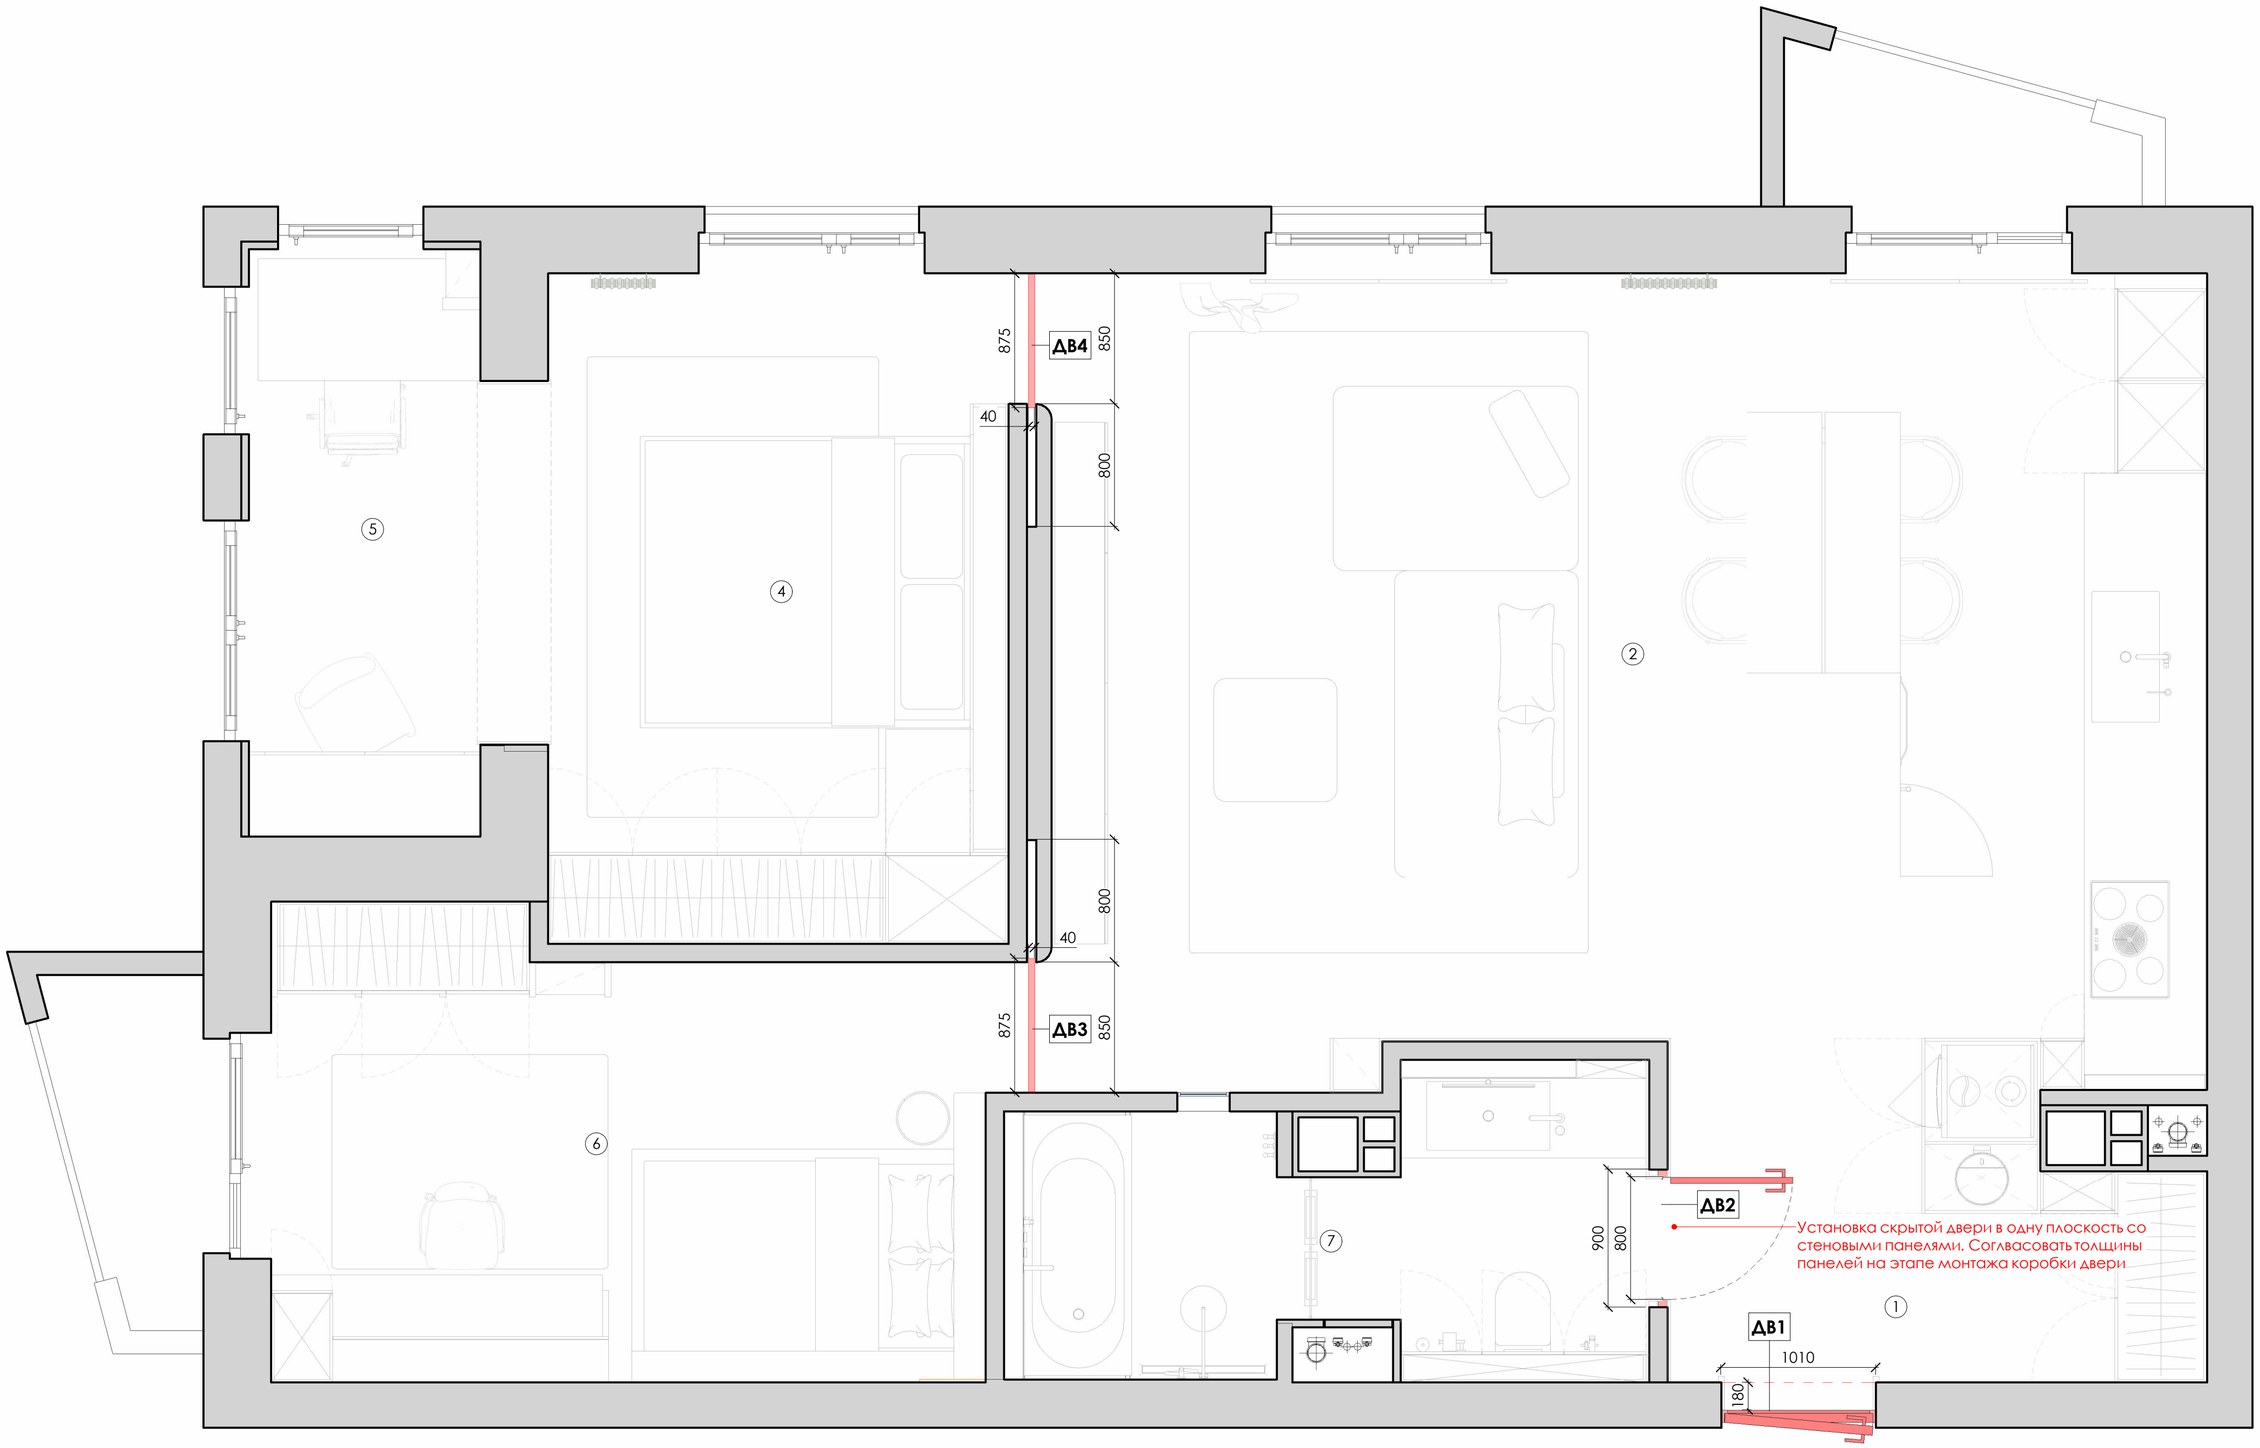

Примечания:

- Все размеры уточнить по месту;
- Все высоты указаны от чистового пола;
- Проемы, имеющие нестандартную толщину, отделываются дверными доборами, изготавливаемыми под заказ фирмой-изготовителем дверей;
- Все чертежи и размеры нетиповых изделий заполнения и отделки проемов выполнены условно. Перед заказом в производство фирма-изготовитель обязана произвести обмеры, включающие корректировку проектных размеров с учетом отделки, выполнить и предоставить заказчику на подпись технологические чертежи с учетом особенностей мебельного производства и пожеланий заказчика;
- Предусмотреть ограничители для дверей.

Спецификация дверей

Тип	Комментарии	Габариты проема	Габариты полотна	Кол-во, шт
ДВ1	Входная дверь Отделка- шпон	Н2130х1010	по факту	1
ДВ2	Дверь скрытого монтажа прямого открывания Отделка - шпон	Н2780х900	Н2720х800	1
ДВ3	Раздвижная дверь в пенал Отделка под покраску	Н2780х850	Н2720х875	1
ДВ4	Раздвижная дверь в пенал Отделка под покраску	Н2780х850	Н2720х875	1

Условные обозначения:

- (1) - марка обозначения помещений
- - существующие стены
- - радиатор отопления
- - шахта
- - канализация, хол. , гор. водоснабжение

Экспликация помещений

№	Наименование	S, кв.м.
1	Прихожая	6.90
2	Кухня-гостиная	39.75
4	Спальня	14.10
5	Лоджия	6.70
6	Детская	14.00
7	Ванная	7.25
		88.70

IVANCHUKINTERIOR

НАИМЕНОВАНИЕ ЧЕРТЕЖА / DRAWING TITLE

ПЛАН ЗАПОЛНЕНИЯ ПРОЕМОВ

№ ЛИСТА/ DRAWING NO: 7

ВЫПОЛНИЛ/ DRAWN BY	ИВАНЧУК А.Ю.
ДАТА/ DATE	13.02.2026
ГОРОД/ CITY	МИНСК

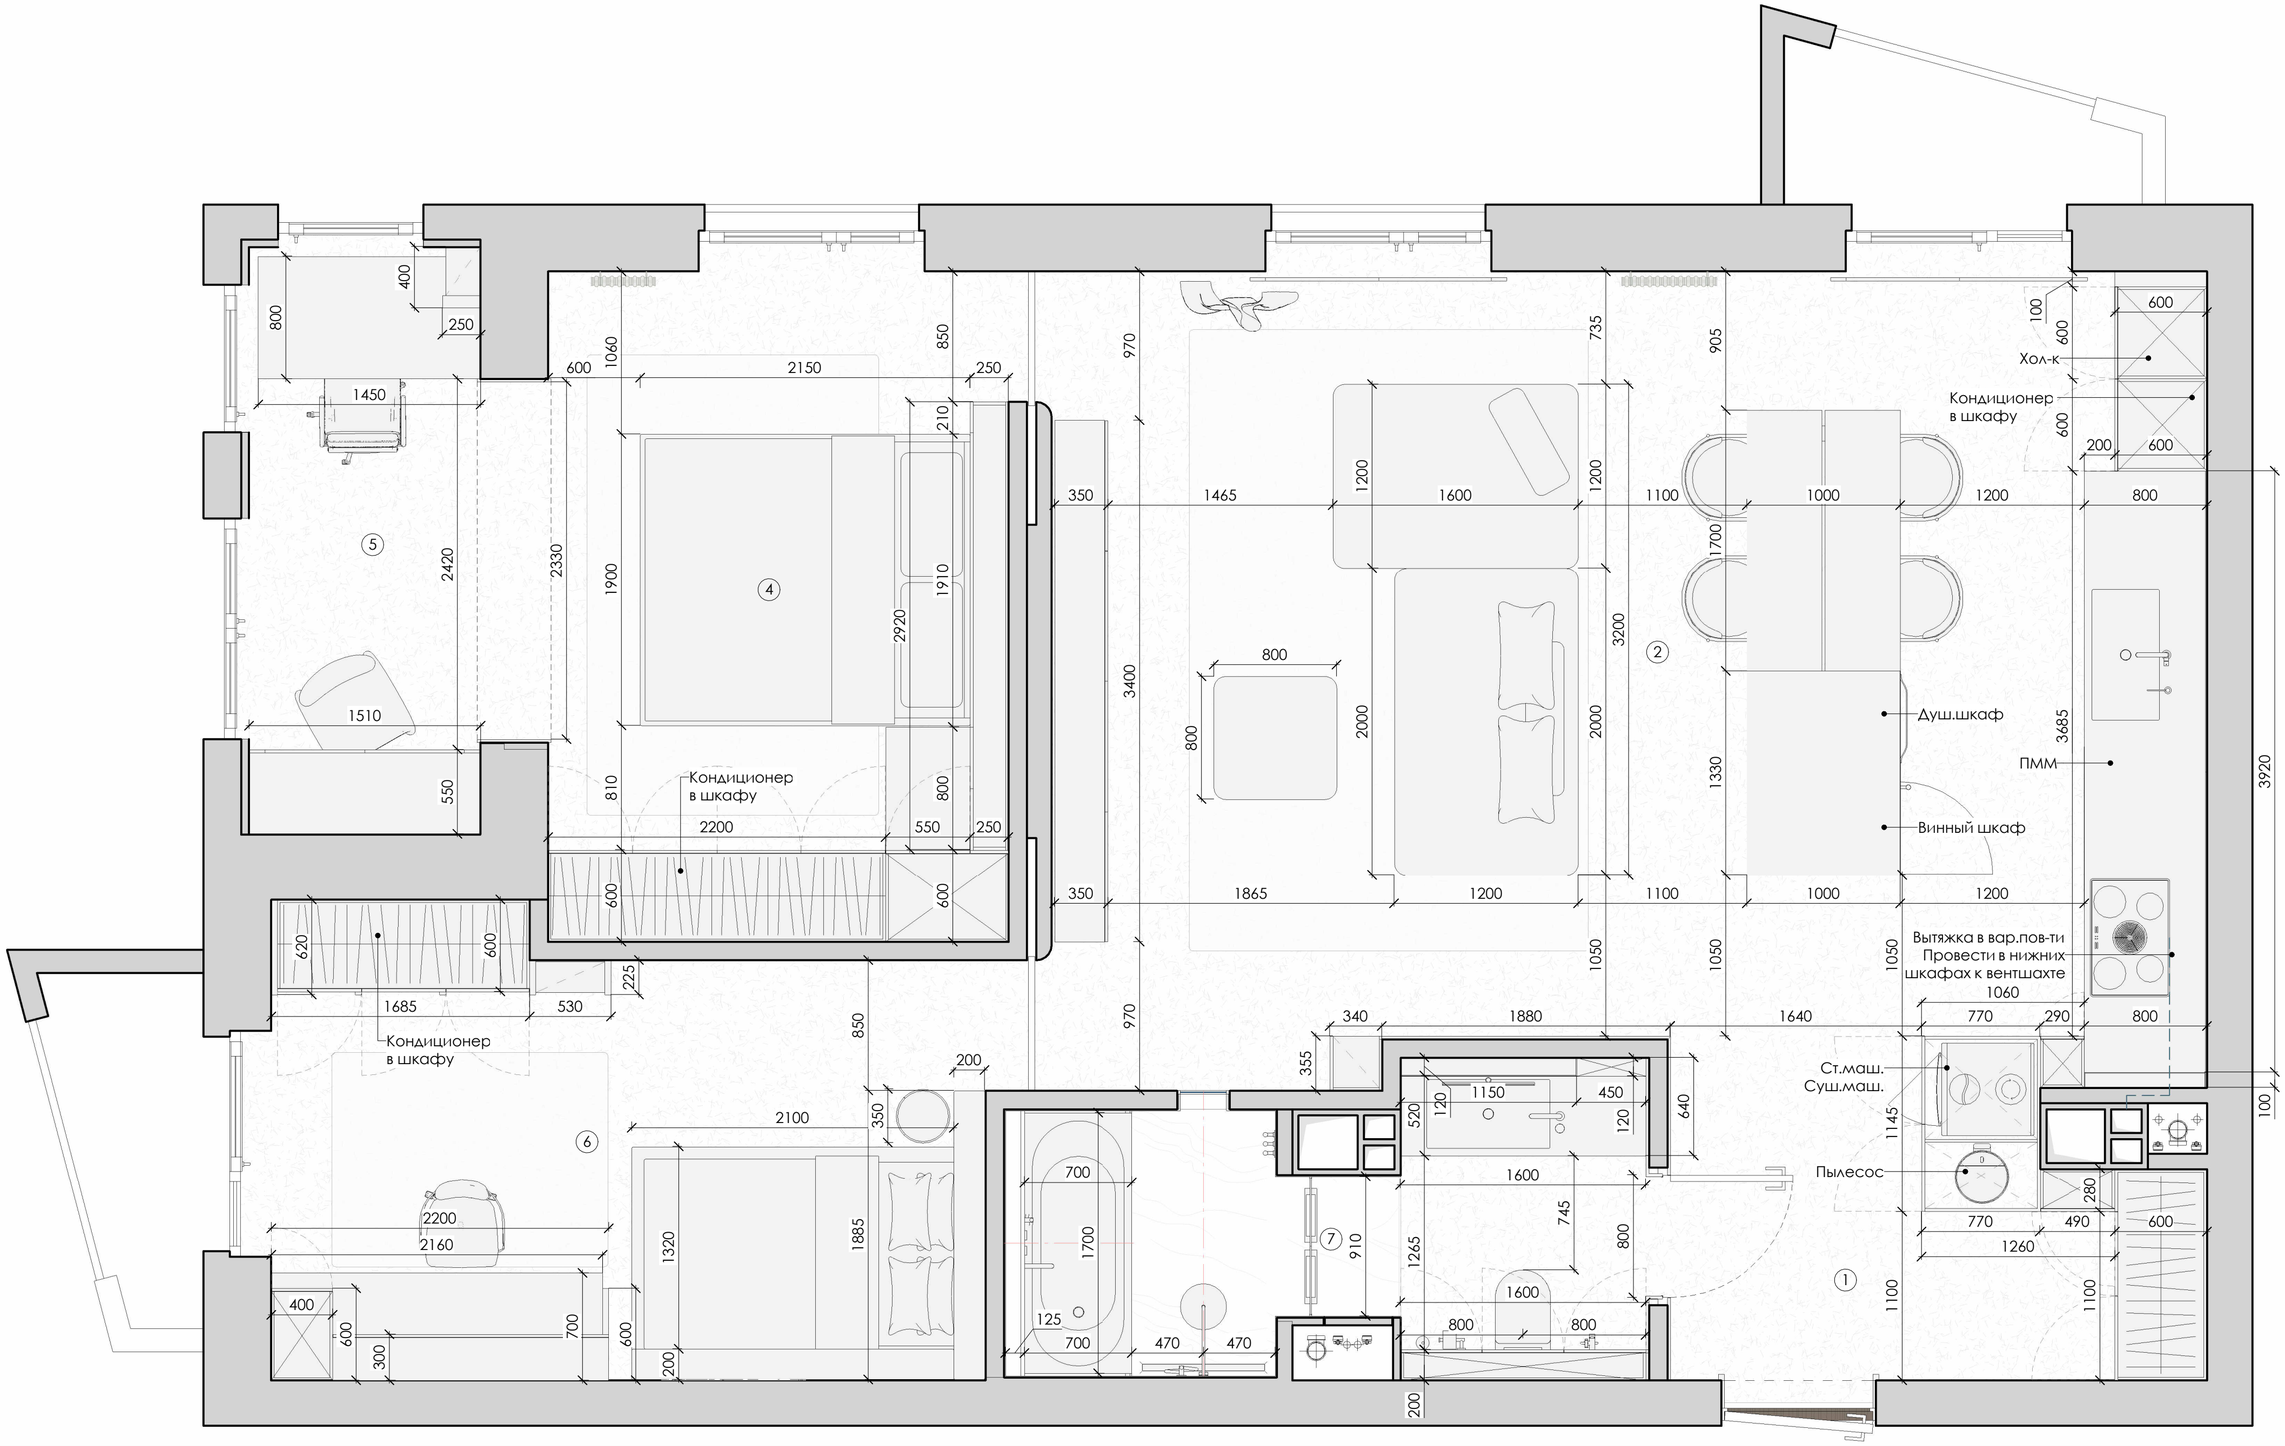

Примечания:

- Мебель и оборудование на плане показаны условно;
- Данный лист см. совместно с графическим материалом - визуализацией помещений;
- Размеры уточнить по месту;
- В случае замены или перемещения сантехнического оборудования в проекте - учесть возможные изменения привязок;
- Перед производством работ и заказом мебели измерить фактические размеры подготовленных конструкций;
- Все размеры мебели, конструкций столярного производства, металлоконструкций уточняются фирмой-изготовителем после обмеров на объекте;
- Окончательный состав и комплектация кухни определяется в момент подписания договора с производителем кухни и согласовывается с автором проекта;
- Вопросы согласовать с заказчиком или представителем авторского надзора.

Условные обозначения:

- (1) - марка обозначения помещений
- - существующие стены
- - радиатор отопления
- - шахта
- - канализация, хол. , гор. водоснабжение

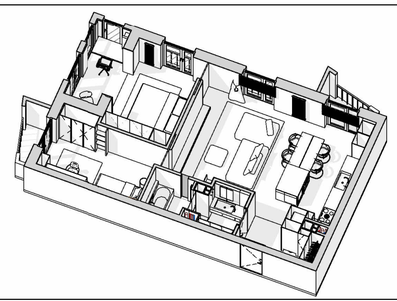

Экспликация помещений

№	Наименование	S, кв.м.
1	Прихожая	6.90
2	Кухня-гостиная	39.75
4	Спальня	14.10
5	Лоджия	6.70
6	Детская	14.00
7	Ванная	7.25
		88.70

IVANCHUKINTERIOR

НАИМЕНОВАНИЕ ЧЕРТЕЖА / DRAWING TITLE

ПЛАН РАССТАНОВКИ МЕБЕЛИ

№ ЛИСТА/ DRAWING NO: 8

ВЫПОЛНИЛ/ DRAWN BY	ИВАНЧУК А.Ю.
ДАТА/ DATE	13.02.2026
ГОРОД/ CITY	МИНСК

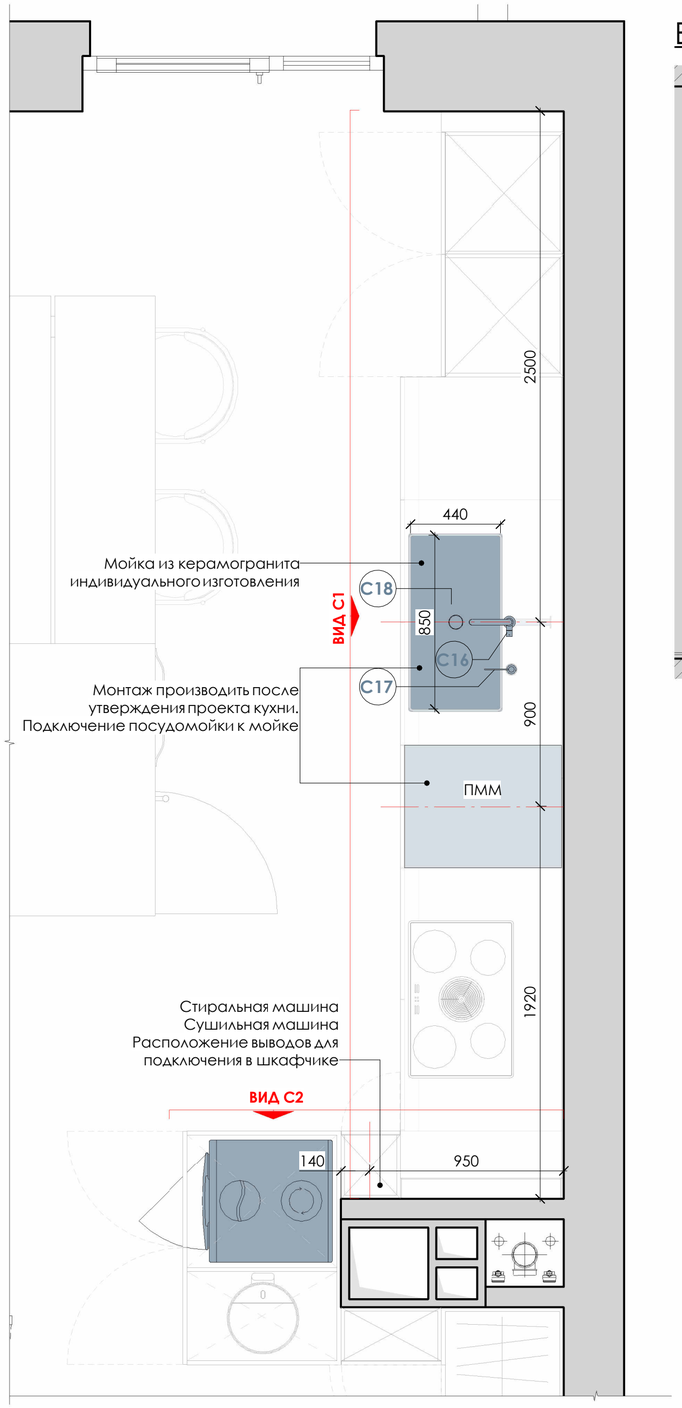

ВИД С1

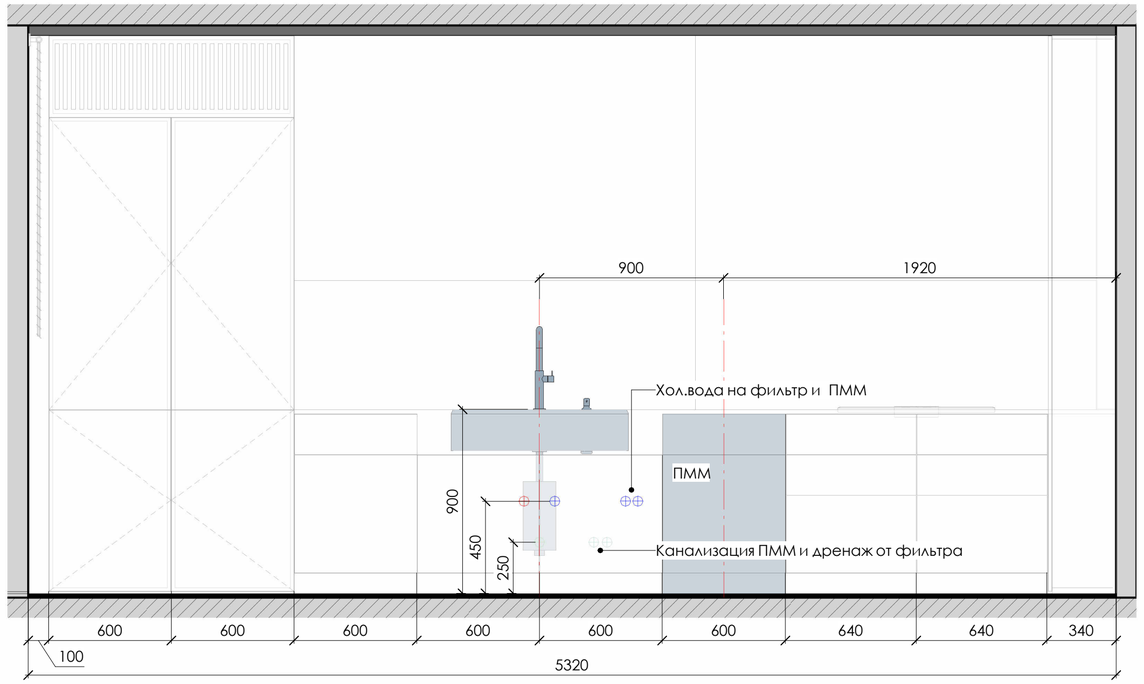

ВИД С2

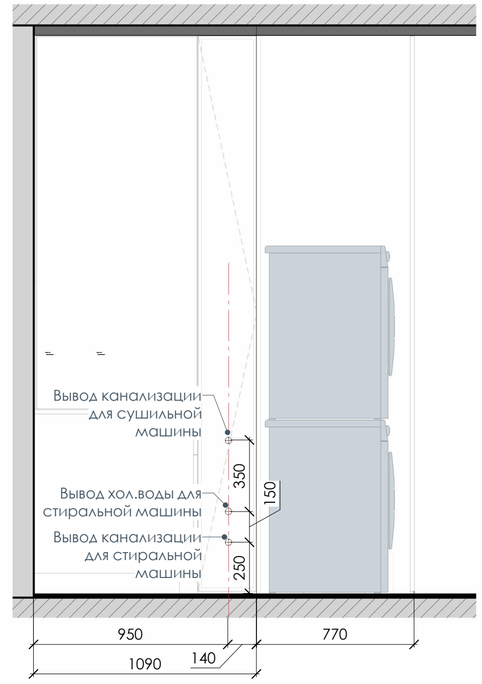

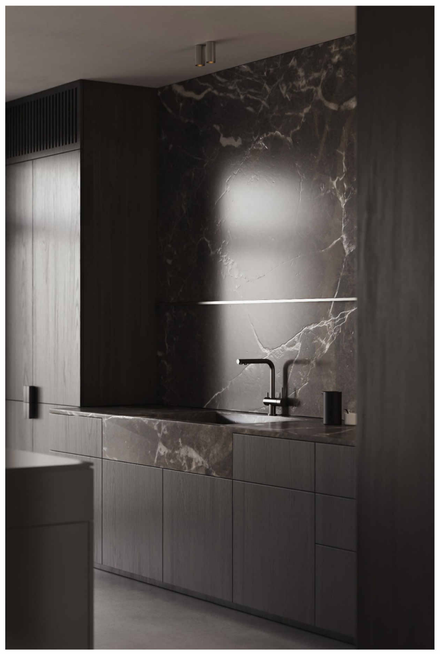

Примечания:

- Данная схема является заданием для мастеров по сантехническому оборудованию;
- Выводы для сантехнических точек и подключение сантехники в санузлах выполняют мастера, отвечающие за ремонт данного помещения;
- Размещение и прокладка труб дополнительно согласуется на месте. В случае невозможности прокладки труб внутри стены, предусмотреть фальшстену либо короб, предварительно согласовав с дизайнером;
- Точные схемы установки сантехнического оборудования смотреть в техническом паспорте продукции (предоставляет поставщик конкретной продукции);
- **Внимание: указанные на схеме модели сантехоборудования могут отличаться от купленных! Высоты и привязки сантехники уточнить после выбора конкретных моделей;**
- Привязки сантехнич. оборудования даны без учета толщины плитки и штукатурки (мастер по сантехническому оборудованию должен самостоятельно прибавить необходимые цифры к размерам) ;
- Следует заменить вводные краны и фильтры грубой очистки воды;
- Смотреть совместно с листами 9.1, 9.2

Условные обозначения:

C1 - марка сантехнического оборудования

- существующие стены

- шахта

- канализация, хол. , гор. водоснабжение

IVANCHUKINTERIOR

НАИМЕНОВАНИЕ ЧЕРТЕЖА / DRAWING TITLE

ПЛАН РАЗМЕЩЕНИЯ САНТЕХНИЧЕСКОГО ОБОРУДОВАНИЯ. КУХНЯ.

№ ЛИСТА/ DRAWING NO	9	ВЫПОЛНИЛ/ DRAWN BY	ИВАНЧУК А.Ю.
		ДАТА/ DATE	13.02.2026
		ГОРОД/ CITY	МИНСК

ВИД С3

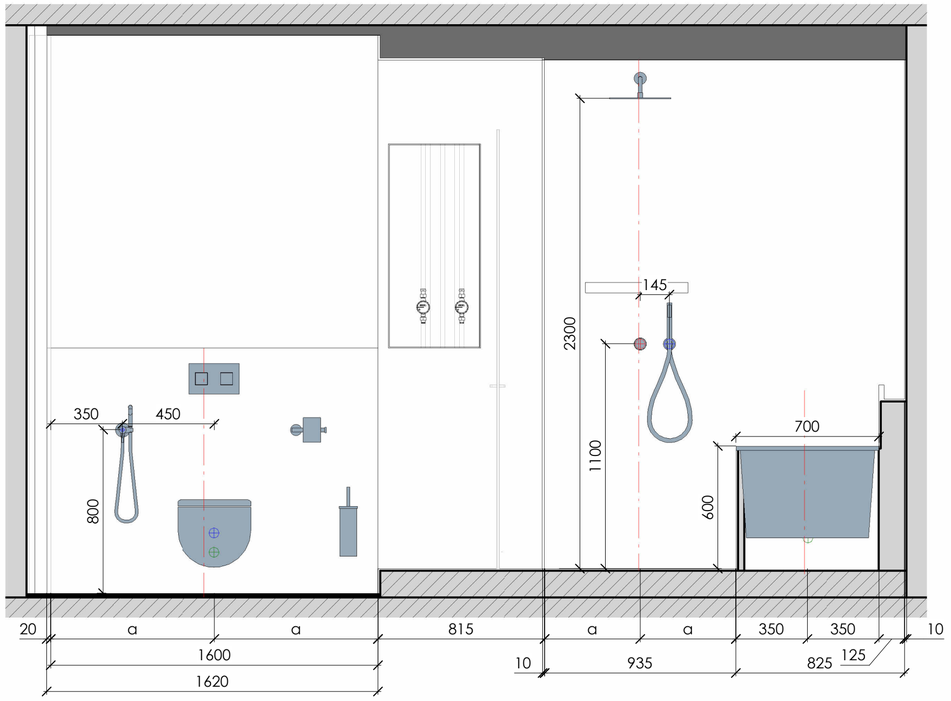

ВИД С4

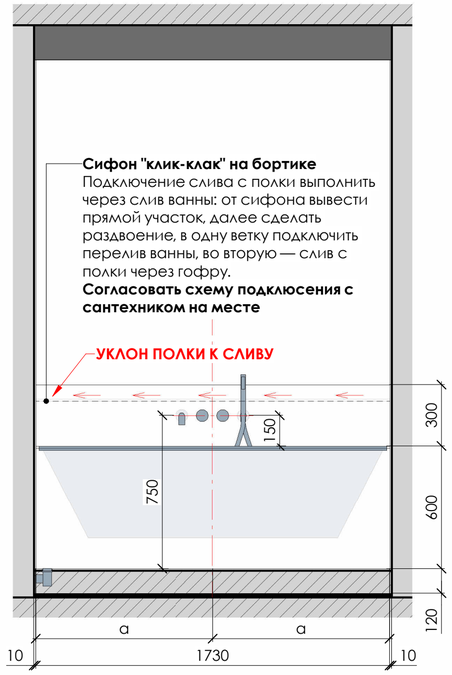

ВИД С5

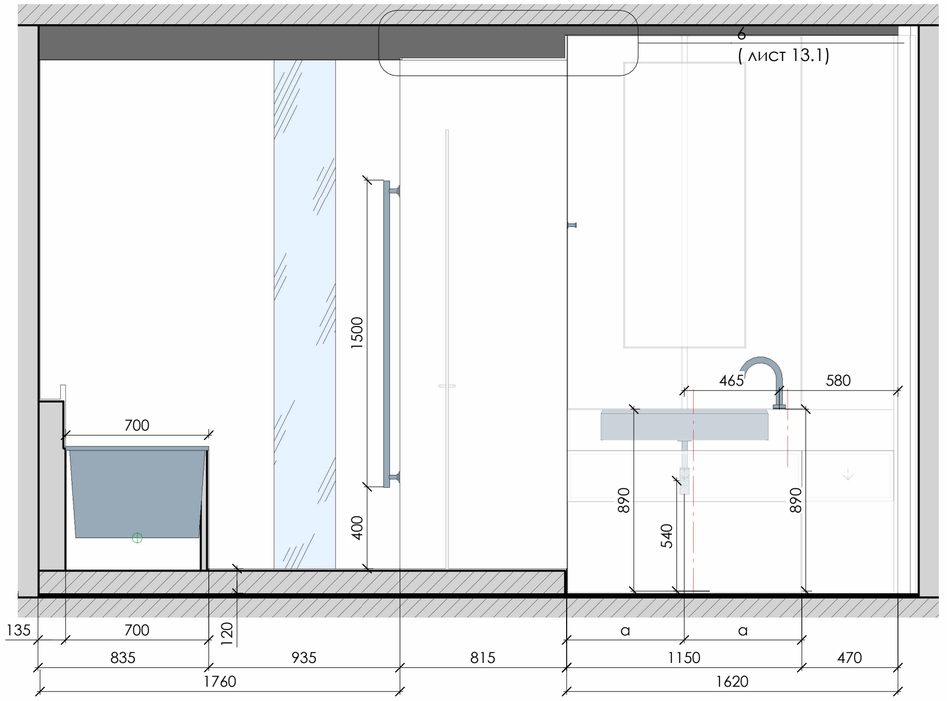

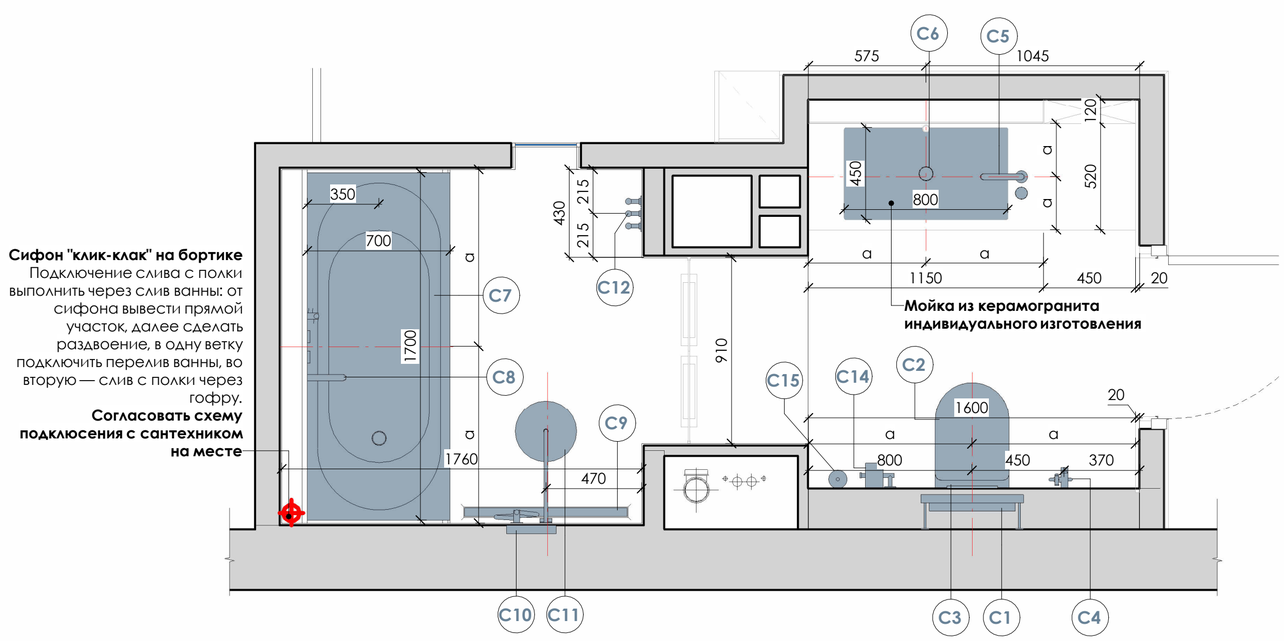

Примечания:

- Данная схема является заданием для мастеров по сантехническому оборудованию;
- Выводы для сантехнических точек и подключение сантехники в санузлах выполняют мастера, отвечающие за ремонт данного помещения;
- Размещение и прокладка труб дополнительно согласуется на месте. В случае невозможности прокладки труб внутри стены, предусмотреть фальшстену либо короб, предварительно согласовав с дизайнером;
- Точные схемы установки сантехнического оборудования смотреть в техническом паспорте продукции (предоставляет поставщик конкретной продукции);
- **Внимание: указанные на схеме модели сантехоборудования могут отличаться от купленных! Высоты и привязки сантехники уточнить после выбора конкретных моделей;**
- Привязки сантехнич. оборудования даны без учета толщины плитки и штукатурки (мастер по сантехническому оборудованию должен самостоятельно прибавить необходимые цифры к размерам) ;
- Следует заменить вводные краны и фильтры грубой очистки воды;
- Смотреть совместно с листами 9.1, 9.2

Условные обозначения:

C1 - марка сантехнического оборудования

- существующие стены

- шахта

- канализация, хол. , гор. водоснабжение

IVANCHUKINTERIOR

НАИМЕНОВАНИЕ ЧЕРТЕЖА / DRAWING TITLE

ПЛАН РАЗМЕЩЕНИЯ САНТЕХНИЧЕСКОГО ОБОРУДОВАНИЯ. ВАННАЯ

№ ЛИСТА/ DRAWING NO	9.1	ВЫПОЛНИЛ/ DRAWN BY	ИВАНЧУК А.Ю.
		ДАТА/ DATE	13.02.2026
		ГОРОД/ CITY	МИНСК

Спецификация сантехнического оборудования и аксессуаров.

Тип	Изображение	Описание	Кол-во, шт.
C1		Инсталляция для унитаза Фабрика: Tece Коллекция: TECEbase Страна: Германия	1
C2		Унитаз подвесной с сиденьем и крышкой SQ Фабрика: domusfalerii Коллекция: Multipla Страна: Италия Описание: цвет белый, 360x520 mm	1
C3		Клавиша смыва TECEsolid Фабрика: Tece Коллекция: Solid Страна: Германия Описание: цвет чёрный матовый	1
C4		Смесителя для п/биде Фабрика: GRB Коллекция: Intimixer Страна: Испания Описание: цвет чёрный металл	1
C5		Смеситель для умывальника 120 Фабрика: GRB Коллекция: Cool Страна: Испания Описание: цвет чёрный металл	1
C6		Выпуск Cl-Cl Фабрика: GRB Коллекция: Universal Страна: Германия Описание: черный металл	2
C7		Ванна кварриловая Oberon Фабрика: Villeroy&Boch Коллекция: Oberon Страна: Германия Описание: 170x70	1
C8	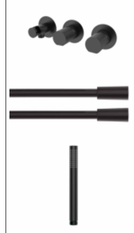	Встроенный смеситель на 2 потребителя Фабрика: GRB Коллекция: Cool Страна: Испания Описание: цвет чёрный металл Душевой шланг Фабрика: GRB Коллекция: Universal Страна: Испания Описание: длинна 170 см, цвет чёрный металл Ручная лейка Фабрика: GRB Коллекция: Tube Страна: Испания Описание: цвет чёрный металл	1
C9		Трап для душа линейный Фабрика: Viega Коллекция: Advantix Vario Страна: Германия Описание: матовая вставка SR1, 80 см	1

Спецификация сантехнического оборудования и аксессуаров.

Тип	Изображение	Описание	Кол-во, шт.
C10	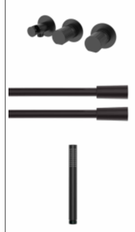	Встроенный смеситель на 2 потребителя Фабрика: GRB Коллекция: Cool Страна: Испания Описание: цвет чёрный металл Душевой шланг Фабрика: GRB Коллекция: Universal Страна: Испания Описание: длинна 170 см, цвет чёрный металл Ручная лейка Фабрика: GRB Коллекция: Tube Страна: Испания Описание: цвет чёрный металл	1
C11		Верхний душ с кронштейном Фабрика: GRB Коллекция: Hydro Страна: Испания Описание: цвет чёрный металл, D=250 мм, кронштейн 400 мм	1
C12		Полотенцесушитель Фабрика: Сунержа Коллекция: Терция PRO Страна: Россия Описание: 1500x100, сатин, тэн справа	1
C13		Крючок Фабрика: Sonia Коллекция: TECNO PROJECT Страна: Испания Описание: цвет чёрный металл	3
C14		Держатель туалетной бумаги открытый Фабрика: Sonia Коллекция: TECNO PROJECT Страна: Испания Описание: цвет чёрный металл	1
C15		Ёрш подвесной Фабрика: Sonia Коллекция: TECNO PROJECT Страна: Испания Описание: цвет чёрный металл	1
C16		Смеситель для кухни Фабрика: Omoikiri Коллекция: Takamatsu-S Страна: Япония Описание: цвет нержавеющая сталь	1
C17		Дозатор Фабрика: Omoikiri Коллекция: OM-02 Страна: Япония Описание: цвет нержавеющая сталь	1
C18		Измельчитель пищевых отходов Фабрика: McAlpine Коллекция: Perfect Grind Страна: Описание: Мощность-обороты: 0,75Лс-2500/min, камера 1070 мл	1

IVANCHUKINTERIOR

НАИМЕНОВАНИЕ ЧЕРТЕЖА / DRAWING TITLE

СПЕЦИФИКАЦИЯ САНТЕХНИЧЕСКОГО ОБОРУДОВАНИЯ

№ ЛИСТА/ DRAWING NO	9.2	ВЫПОЛНИЛ/ DRAWN BY	ИВАНЧУК А.Ю.
		ДАТА/ DATE	13.02.2026
		ГОРОД/ CITY	МИНСК

ВИД 7.1

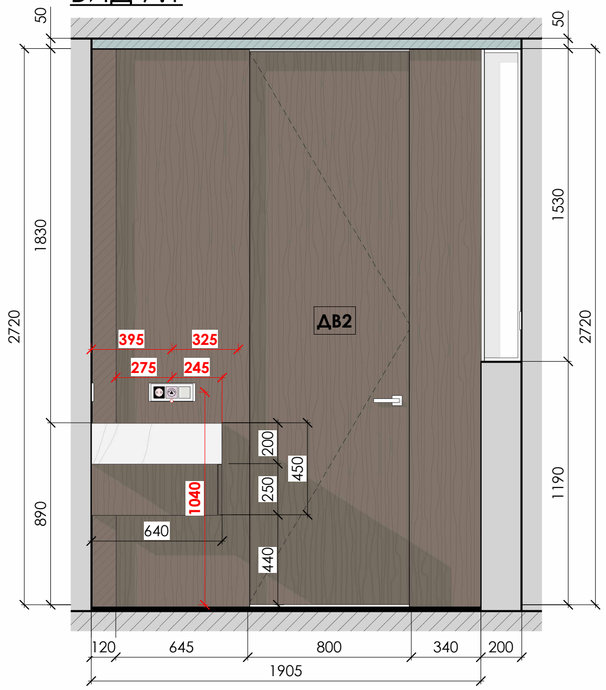

ВИД 7.2

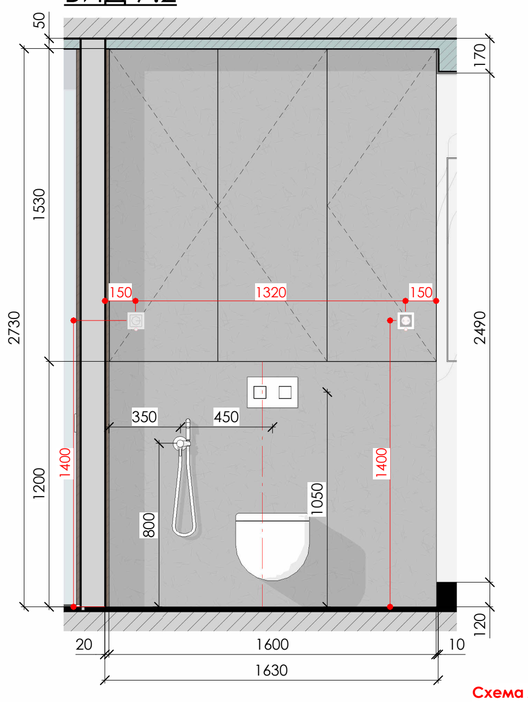

ВИД 7.3

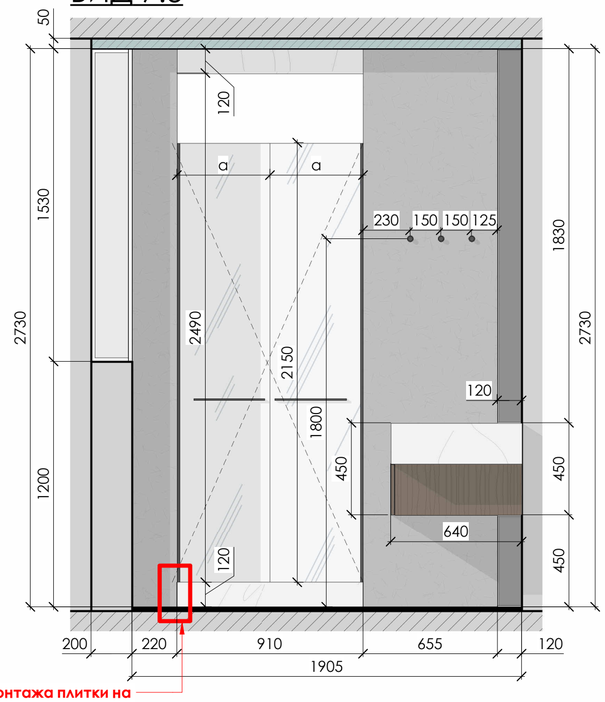

Схема монтажа плитки на торце подиума, см Узел А

ВИД 7.4

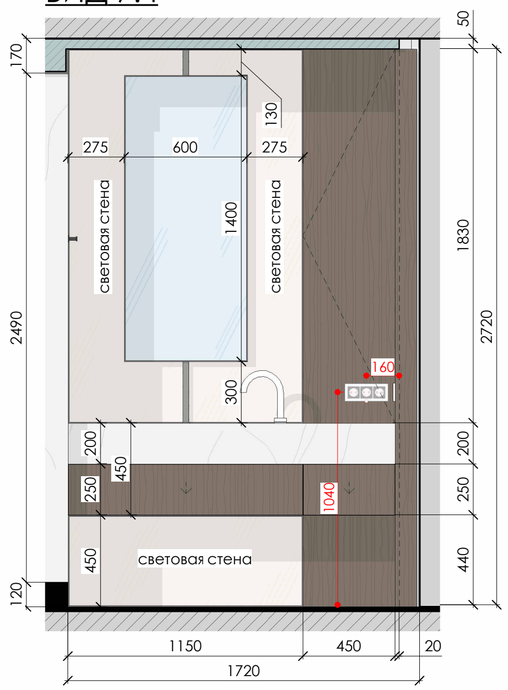

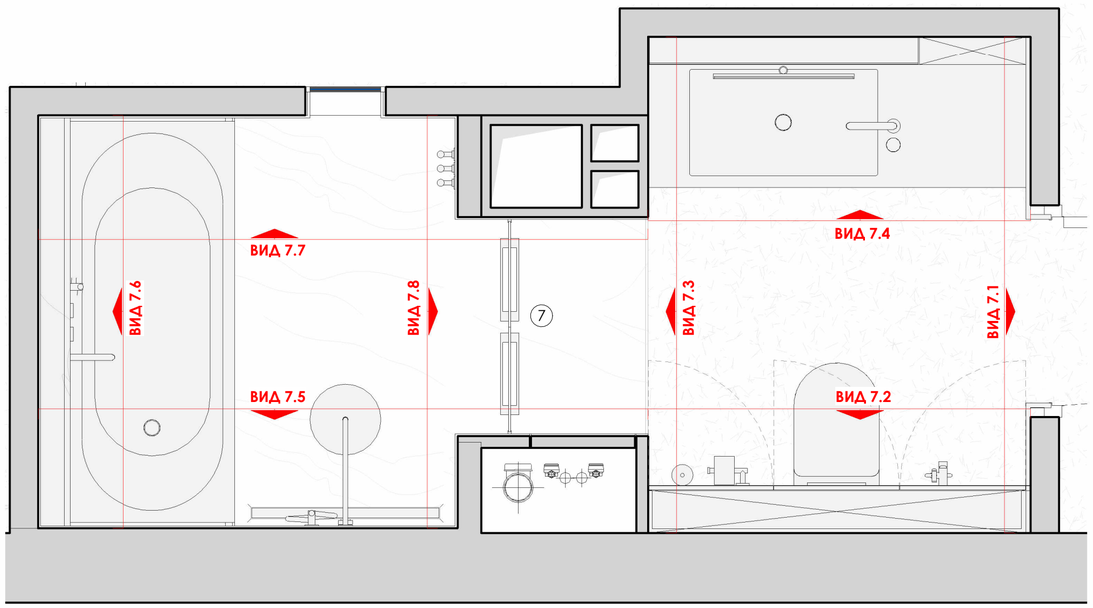

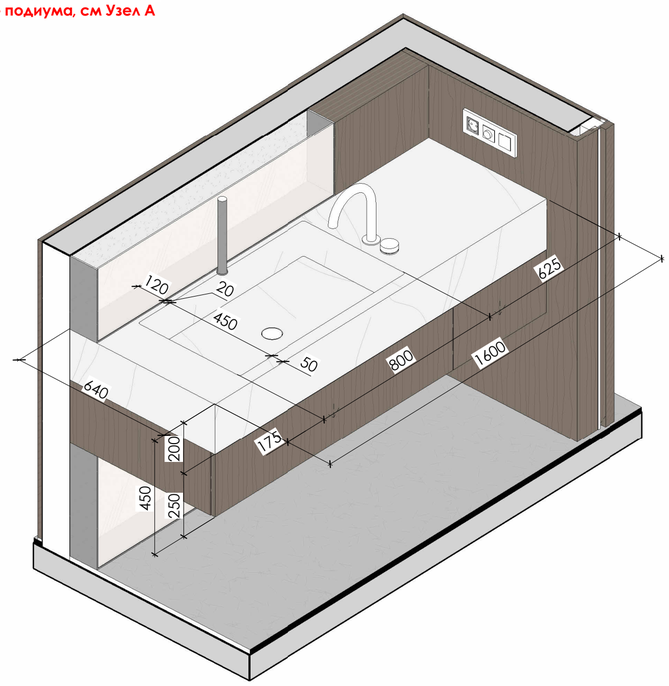

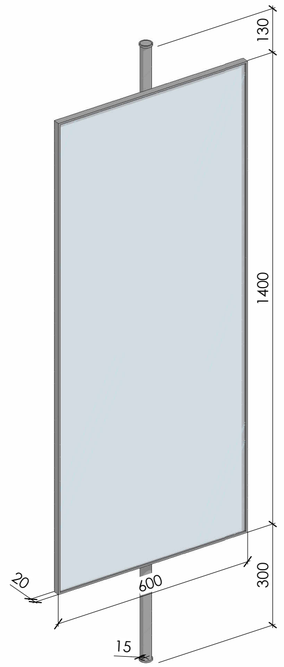

Примечания:

- Все отделочные материалы должны быть выполнены в единой плоскости. При установке материалов учесть их толщину и соблюдение допусков для предотвращения неровностей и зазоров.
- Мебель и встроенные элементы должны быть установлены в соответствии с проектом. Все размеры и положения, указанные в проекте, подлежат перепроверке на этапе монтажа.
- Расположение осветительных приборов, выключателей и розеток соответствует проекту. Необходимо обеспечить правильную высоту установки и проверить расположение электрических точек в реальных условиях.
- До покупки полного объема краски выполнить предварительные выкрасы на небольших участках для проверки цвета и покрытия.

Спецификация отделочных материалов.Ванная.

Тип	УГО	Описание	Площадь, кв.м.
ОС2		Микроцемент	7.3
ОС3		Покраска влагостойкой краской	13.1
ОС6		Керамогранит LINEN / Museum / Desert / 1000x2750x6 mm	28.0

Площадь плитки посчитана у учетом пола, стен, ванной, потолка

Узел А

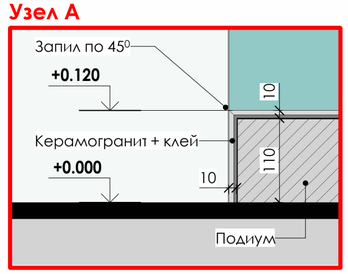

IVANCHUKINTERIOR

НАИМЕНОВАНИЕ ЧЕРТЕЖА / DRAWING TITLE

РАЗВЕРТКА ВАННОЙ

№ ЛИСТА/ DRAWING NO	10	ВЫПОЛНИЛ/ DRAWN BY	ИВАНЧУК А.Ю.
		ДАТА/ DATE	13.02.2026
		ГОРОД/ CITY	МИНСК

ВИД 7.5

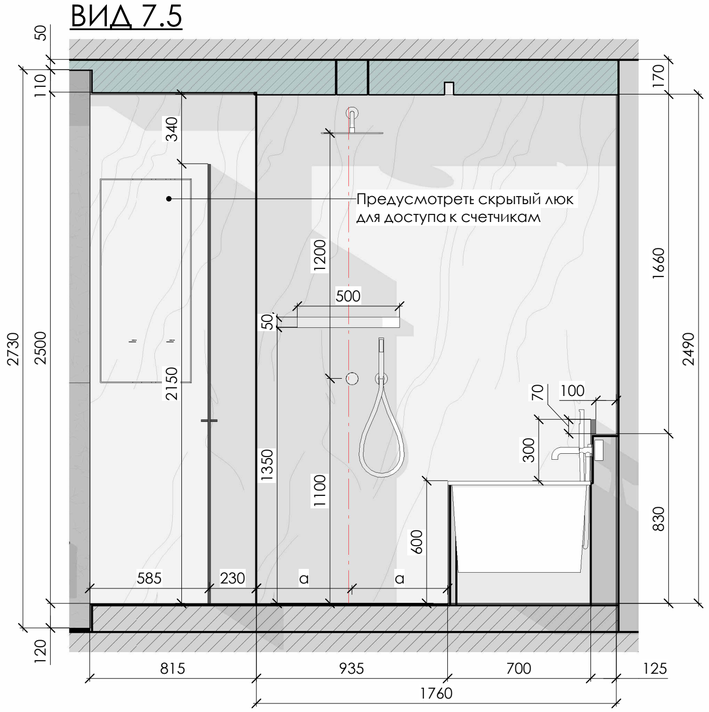

ВИД 7.6

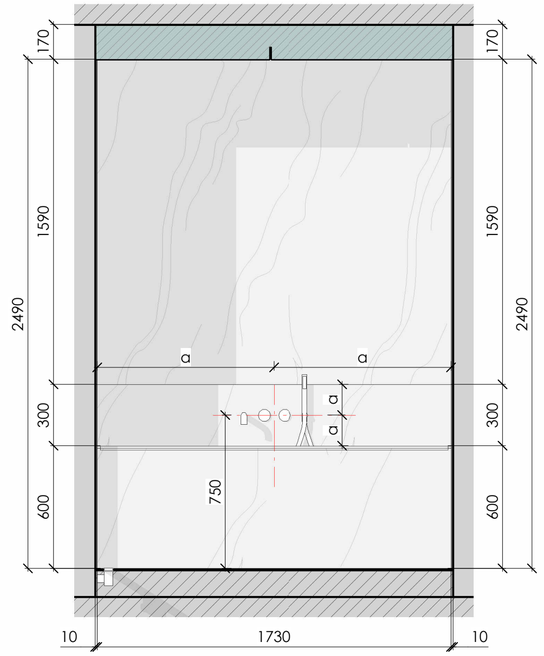

ВИД 7.7

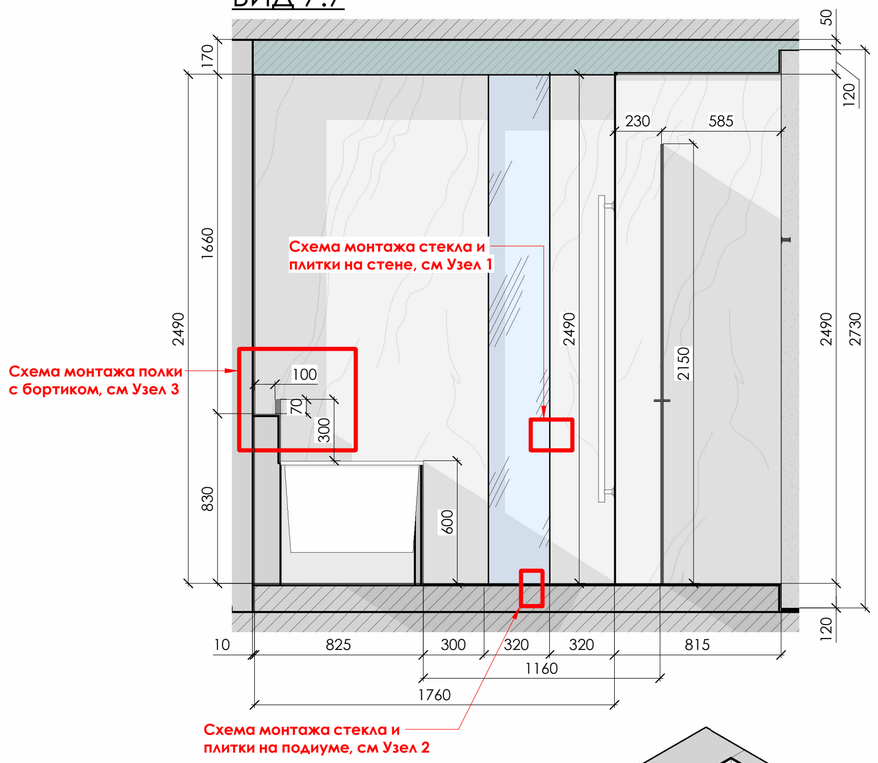

ВИД 7.8

Узел 1

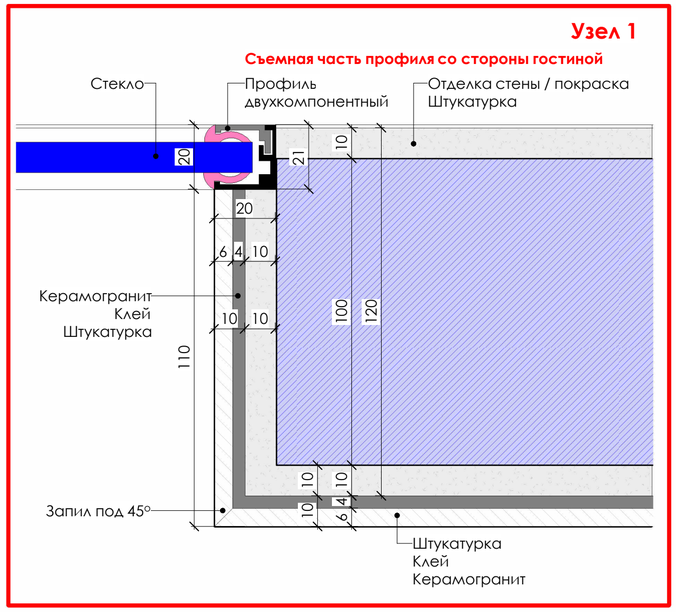

Примечания:

- Все отделочные материалы должны быть выполнены в единой плоскости. При установке материалов учесть их толщину и соблюдение допусков для предотвращения неровностей и зазоров.
- Мебель и встроенные элементы должны быть установлены в соответствии с проектом. Все размеры и положения, указанные в проекте, подлежат перепроверке на этапе монтажа.
- Расположение осветительных приборов, выключателей и розеток соответствует проекту. Необходимо обеспечить правильную высоту установки и проверить расположение электрических точек в реальных условиях.
- До покупки полного объема краски выполнить предварительные выкрасы на небольших участках для проверки цвета и покрытия.

Узел 2

Узел 3

IVANCHUKINTERIOR

НАИМЕНОВАНИЕ ЧЕРТЕЖА / DRAWING TITLE

РАЗВЕРТКА ВАННОЙ

№ ЛИСТА/ DRAWING NO	10.1	ВЫПОЛНИЛ/ DRAWN BY	ИВАНЧУК А.Ю.
		ДАТА/ DATE	13.02.2026
		ГОРОД/ CITY	МИНСК

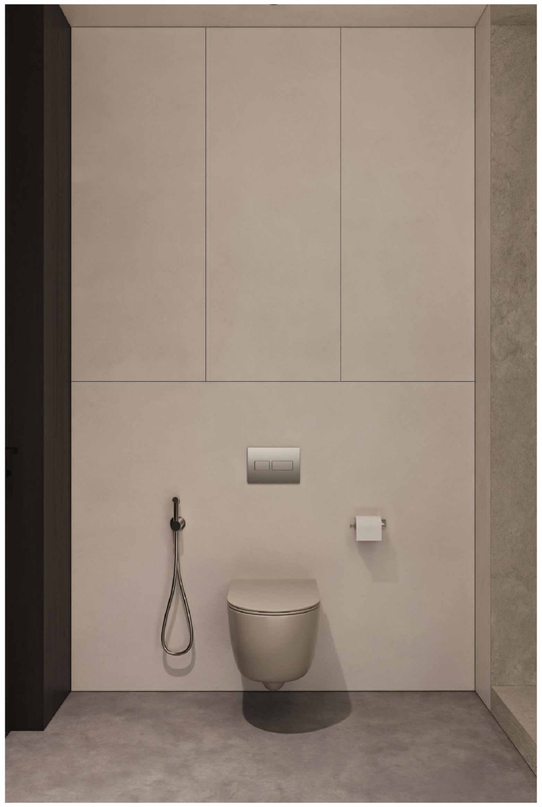

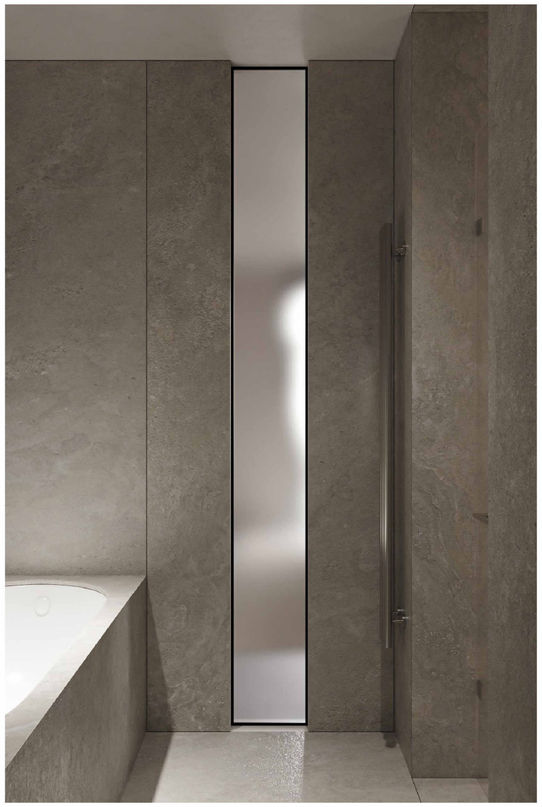

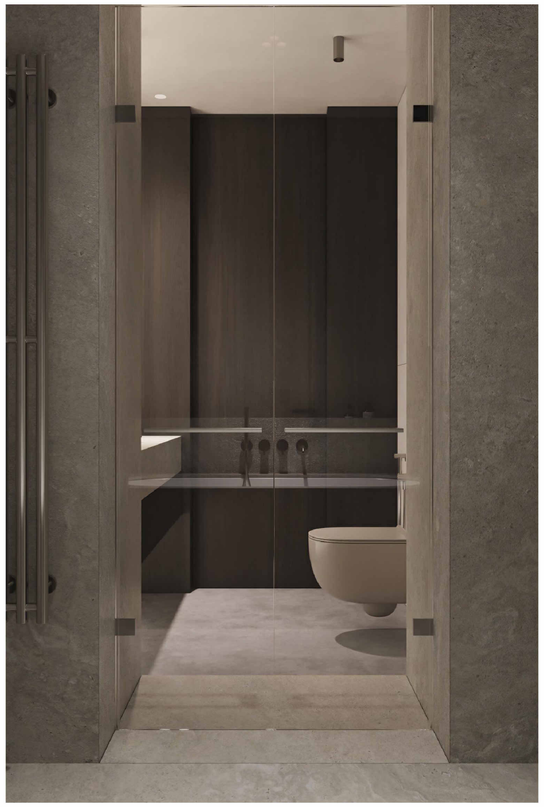

Примечания:

- На чертежах указаны чистые площади напольных покрытий, точный расчет материалов с учетом подрезок и комплектации под ящики производит фирма-поставщик;
- Отметки верха напольного покрытия должны быть выполнены в одном уровне (без перепадов);
- Периметр плинтусовки выполняется отдельно (по факту). Замеры выполняются подрядчиком;
- Окончательное крепление плинтуса выполнять после установки шкафов;
- Цвет фуги согласовывается с дизайнером;
- В ванной комнате предусмотреть устройство дополнительного защитного гидроизоляционного покрытия пола;
- Вопросы согласовать с заказчиком или представителем авторского надзора.

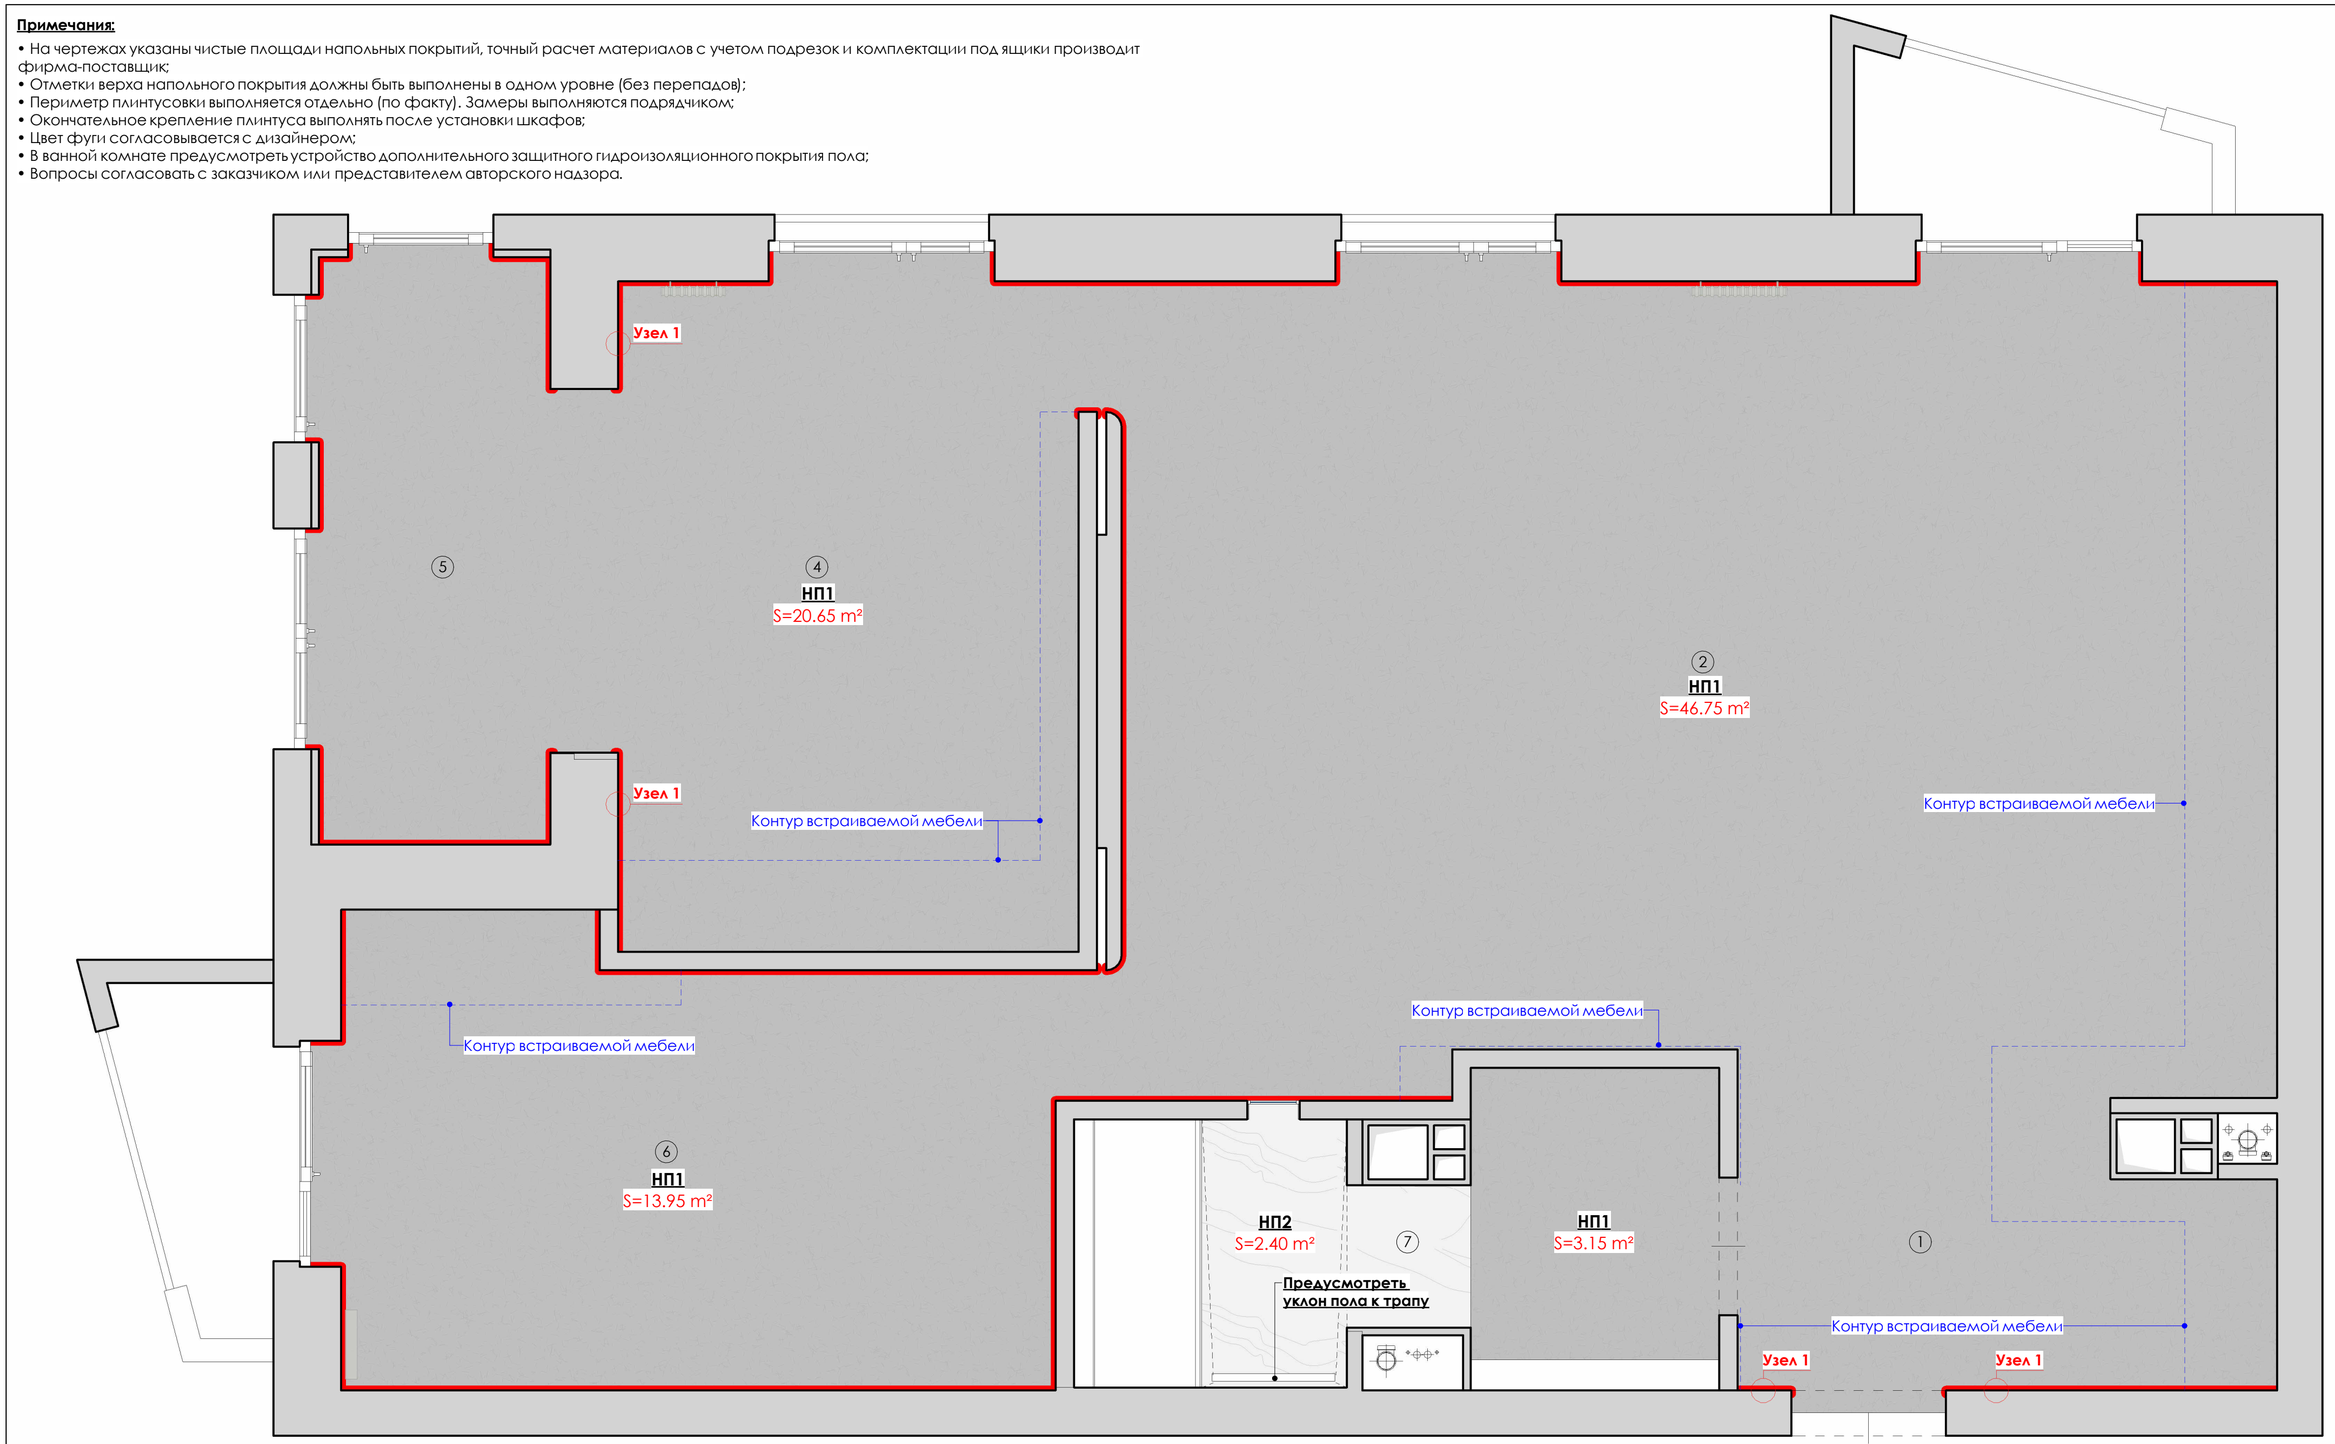

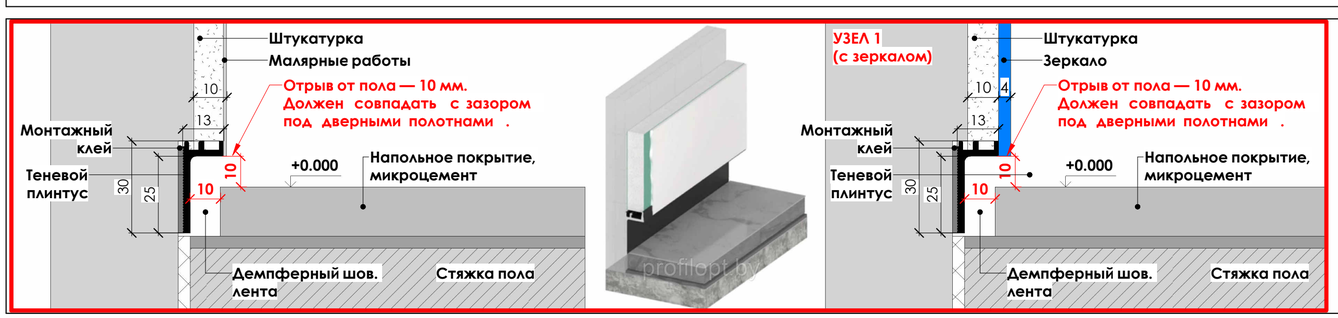

Спецификация напольных покрытий

Тип	УГО	Описание	S, кв.м
НП1		Микроцемент	84.45 m²
НП2		Керамогранит Ceramiche Coem | TERRAZZO Caolino mini 1200x600 мм, 10 мм	2.40 m²

Спецификация скрытых плинтусов

УГО	Примечание	Длина, пог.м
	Плинтус теневой AUF-PROFILL 25 алюминиевый. Цвет:черный матовый	36.3

IVANCHUKINTERIOR

НАИМЕНОВАНИЕ ЧЕРТЕЖА / DRAWING TITLE

ПЛАН НАПОЛЬНЫХ ПОКРЫТИЙ

№ ЛИСТА/ DRAWING NO	11	ВЫПОЛНИЛ/ DRAWN BY	ИВАНЧУК А.Ю.
		ДАТА/ DATE	13.02.2026
		ГОРОД/ CITY	МИНСК

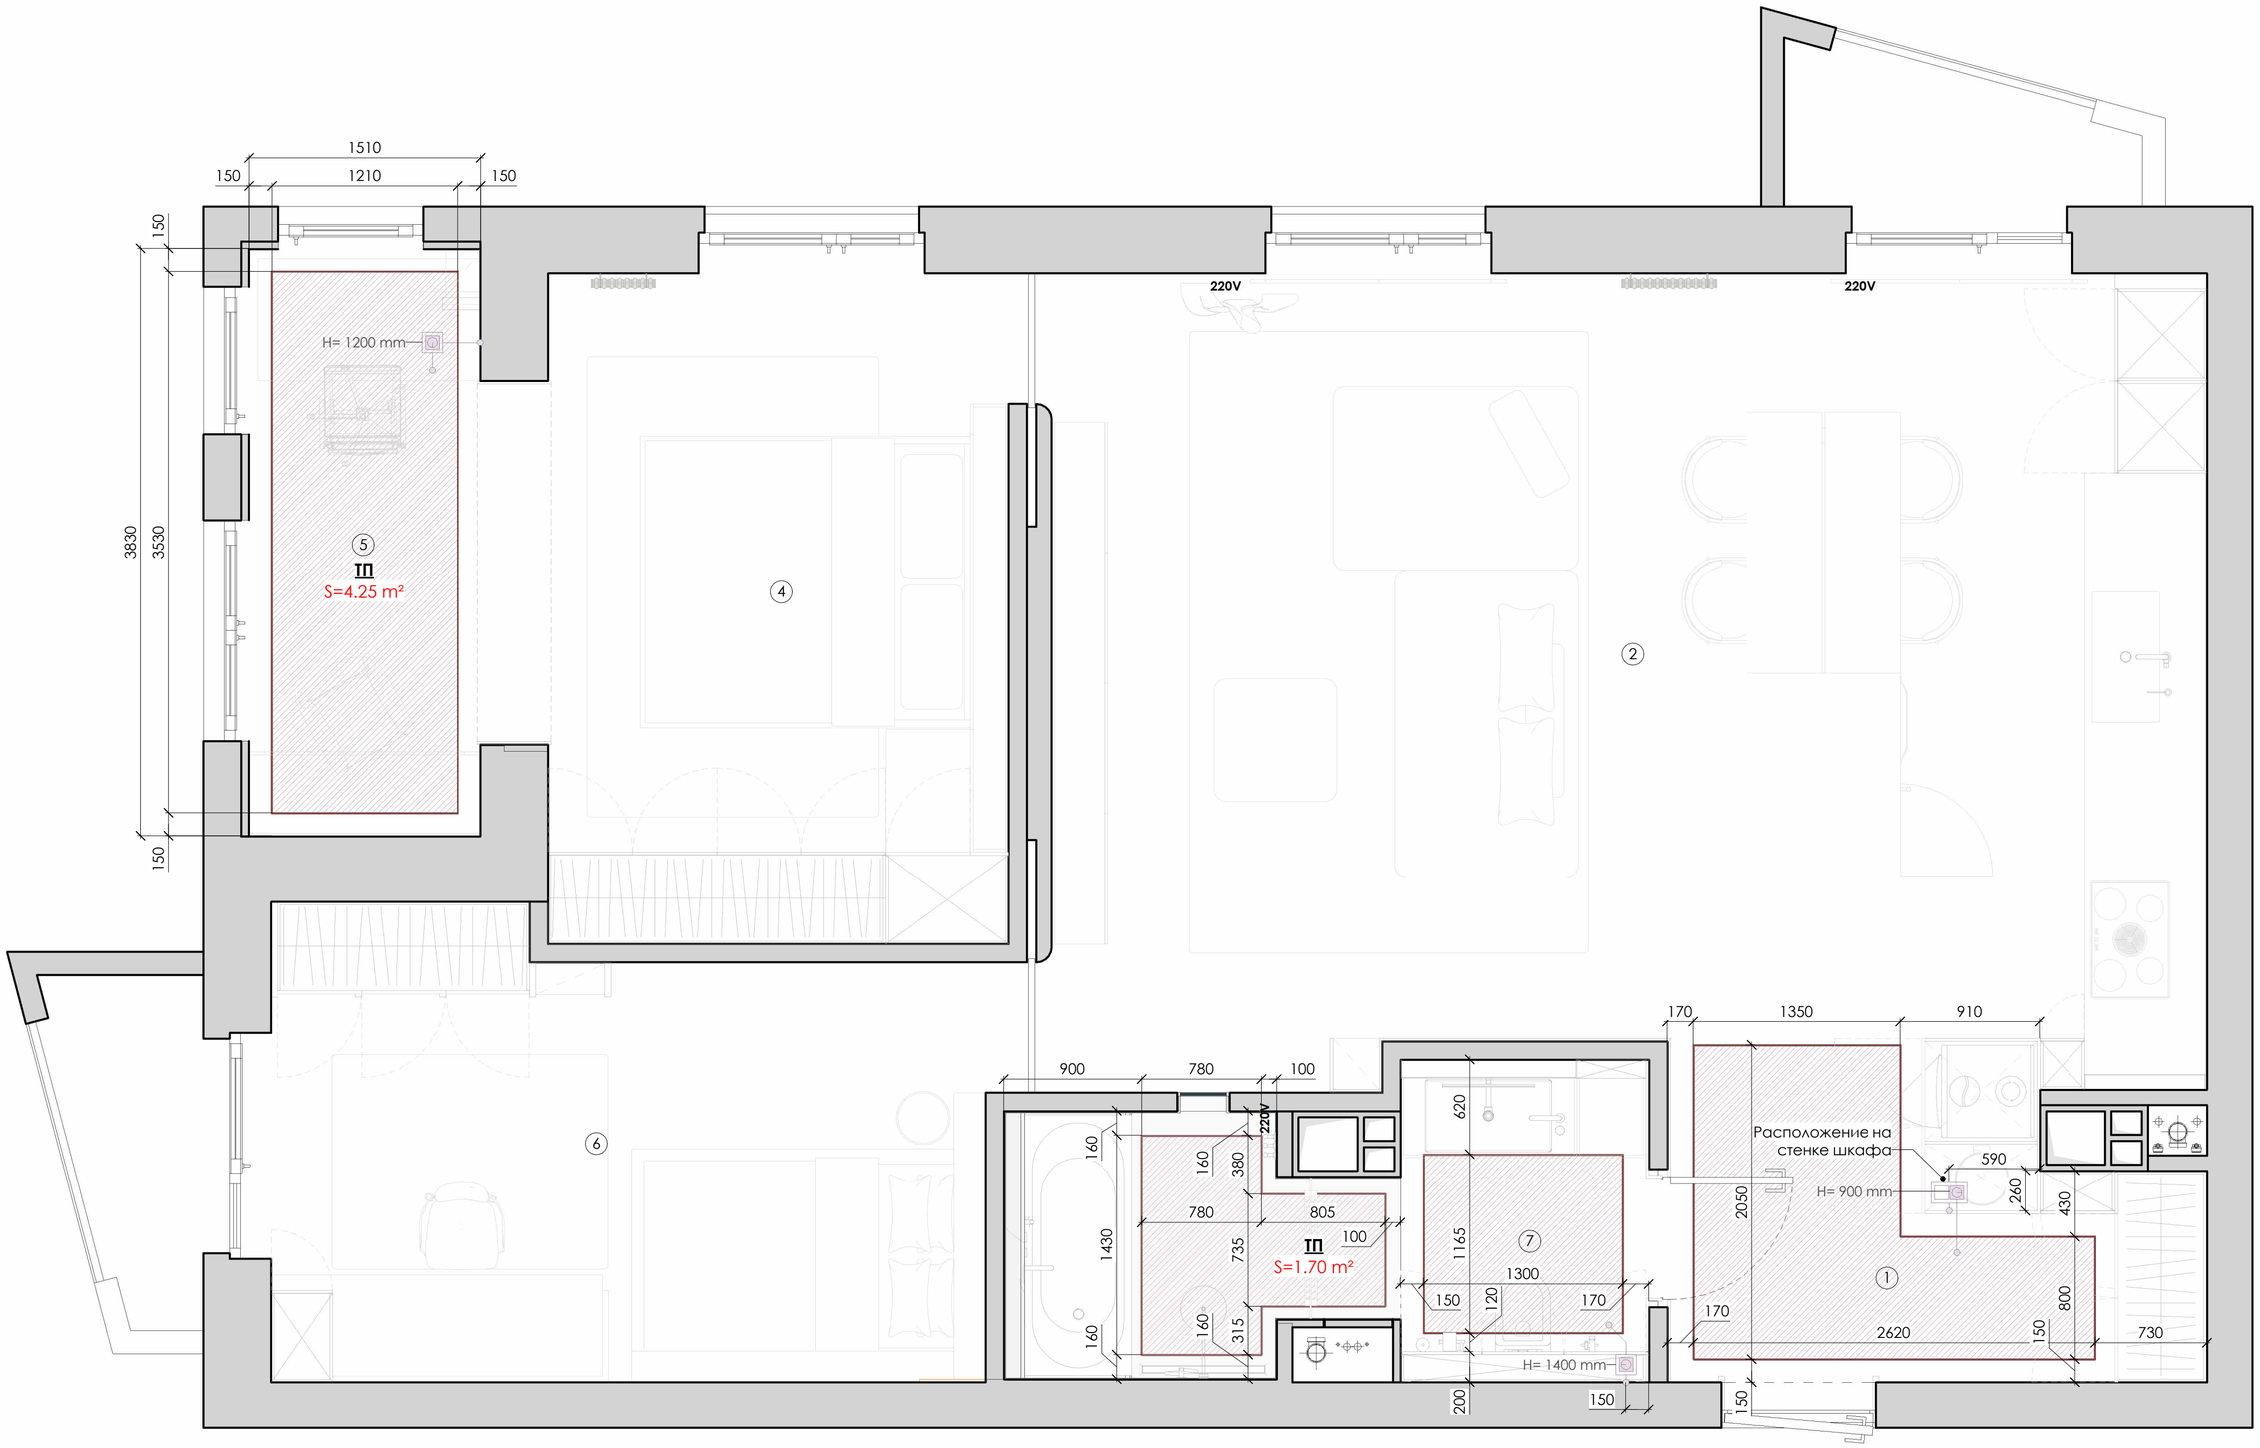

Условные обозначения:

- (1) - марка обозначения помещений
- - существующие стены
- - радиатор отопления
- - шахта
- - канализация, хол. , гор. водоснабжение

Примечания:

- Все размеры уточнить по месту;
- Устройство теплого пола в клею плитки;
- Теплые полы укладываются на расстоянии 100-150 мм от стен (если не указана другая) и на расстоянии 50-60 мм (0,5 шага укладки нагревательного кабеля) от часто используемой мебели.

Спецификация теплого пола

Тип	УГО	Описание	S, кв.м
ТП		Теплый пол	11.30 m²

Спецификация терморегуляторов

УГО	Описание	Кол-во, шт
	Терморегулятор теплого пола	3

Экспликация помещений

№	Наименование	S, кв.м.
1	Прихожая	6.90
2	Кухня-гостиная	39.75
4	Спальня	14.10
5	Лоджия	6.70
6	Детская	14.00
7	Ванная	7.25
		88.70

IVANCHUKINTERIOR

НАИМЕНОВАНИЕ ЧЕРТЕЖА / DRAWING TITLE

ПЛАН ТЕПЛОГО ПОЛА

№ ЛИСТА/ DRAWING NO	12	ВЫПОЛНИЛ/ DRAWN BY	ИВАНЧУК А.Ю.
		ДАТА/ DATE	13.02.2026
		ГОРОД/ CITY	МИНСК

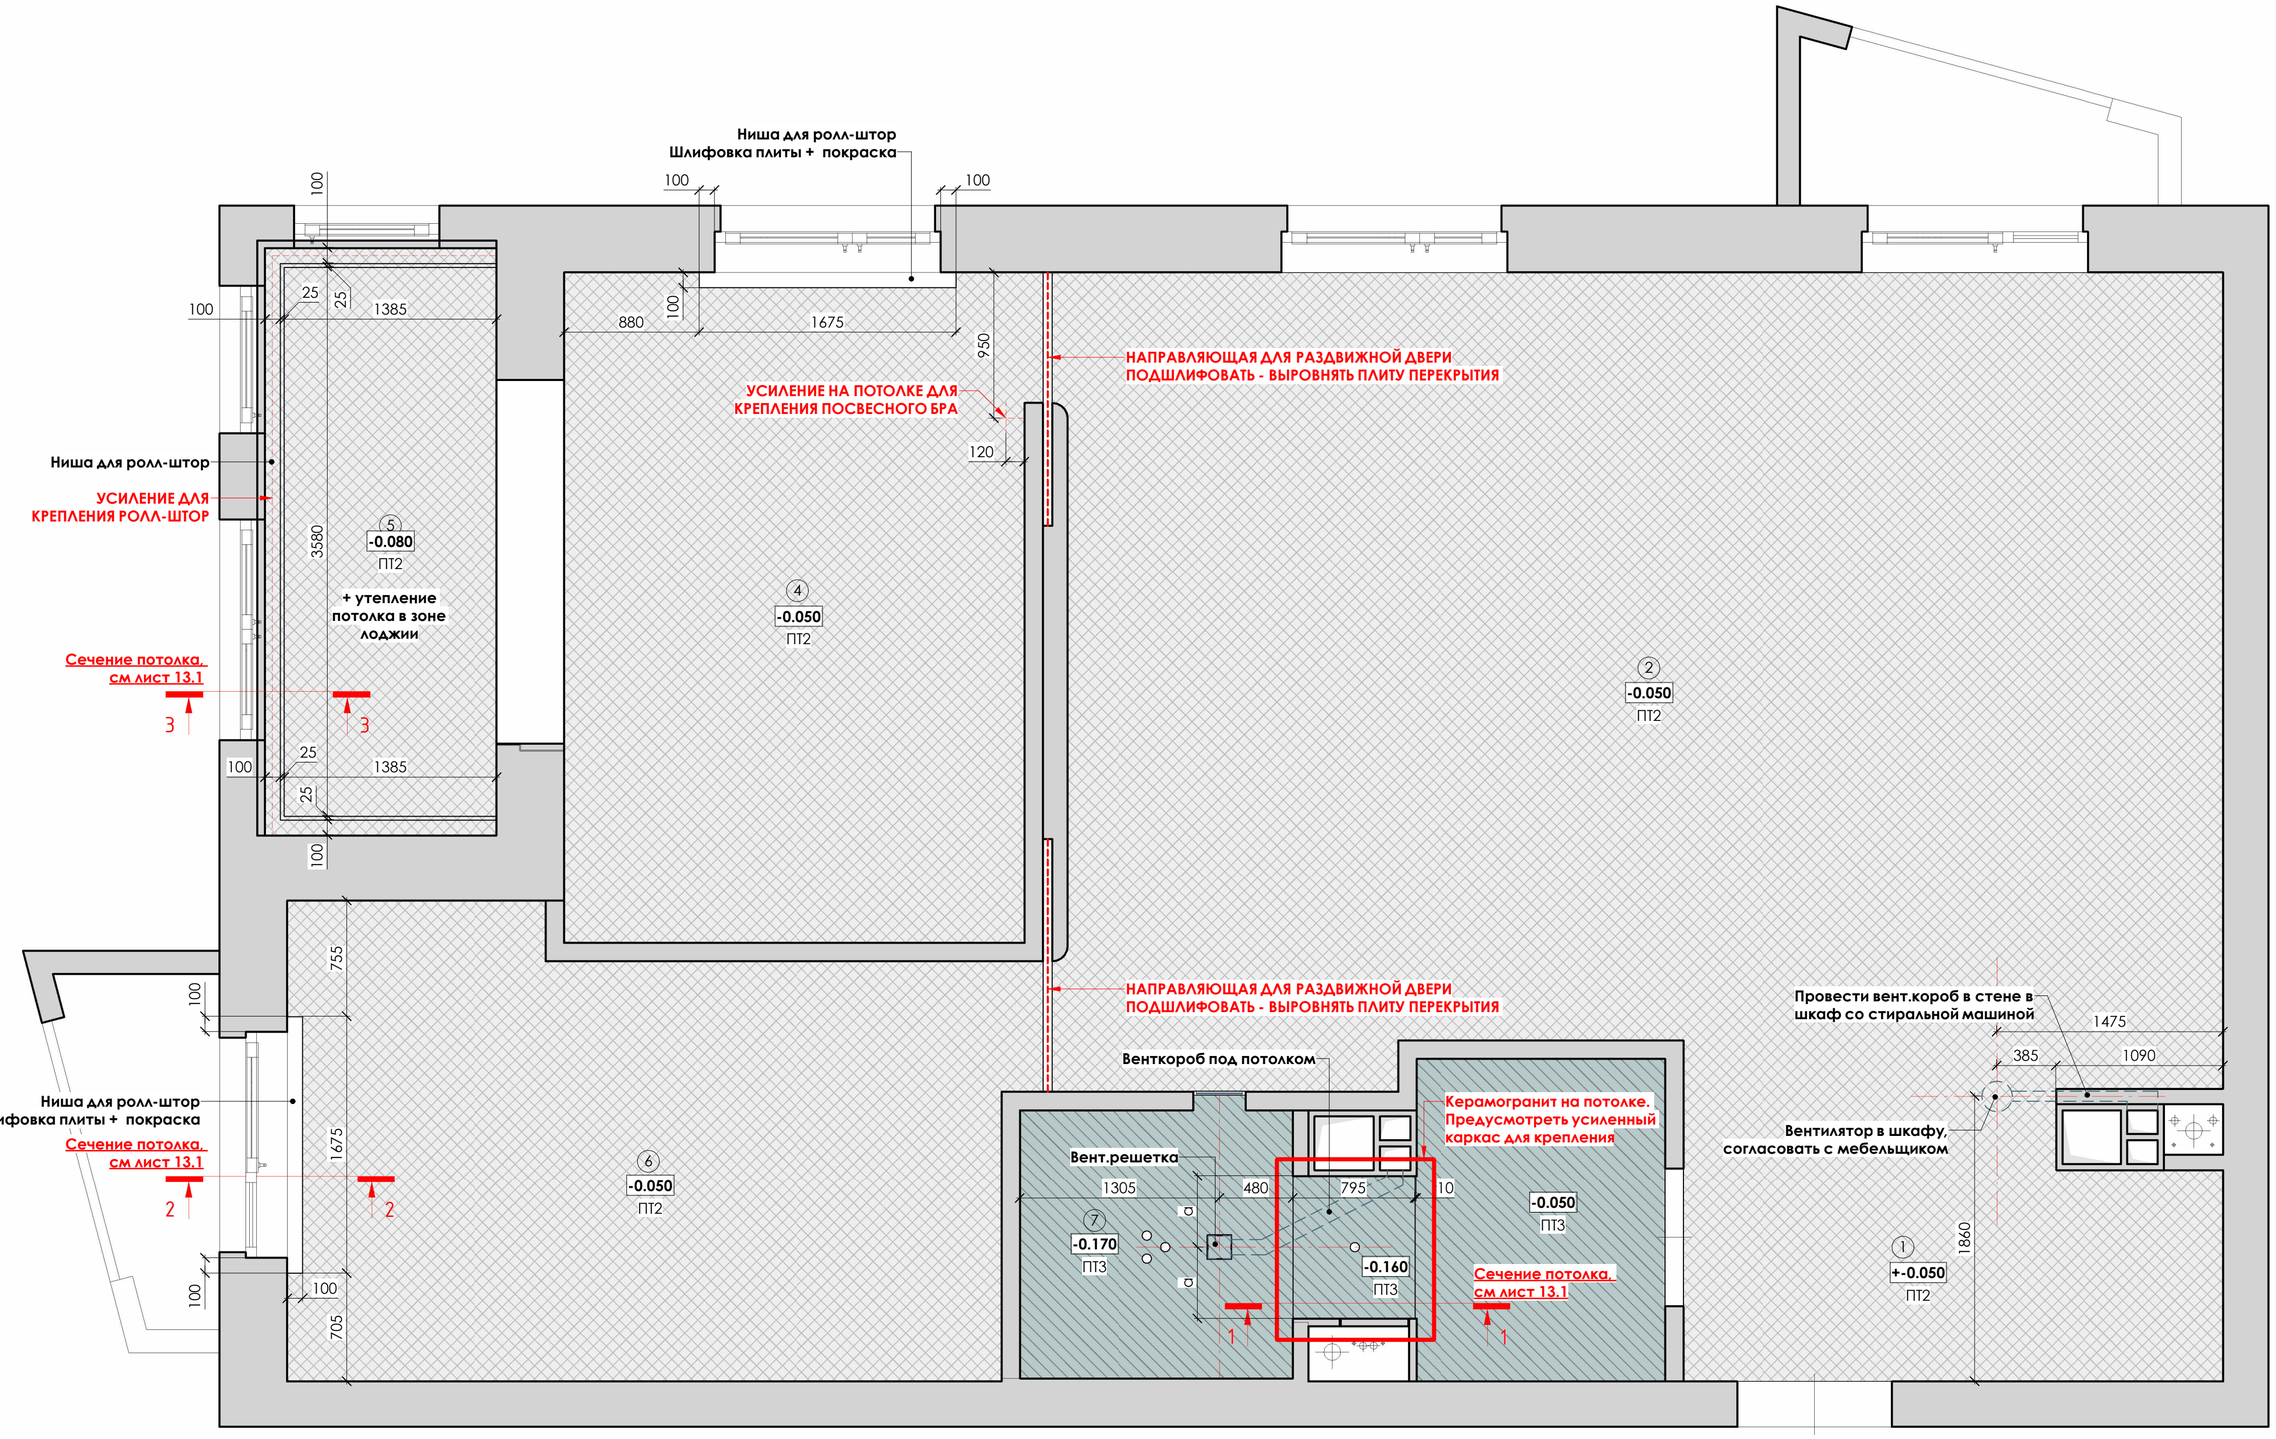

Примечания:

- Отметка 0,000 соответствует отметке верхнего перекрытия;
- Точный цвет краски указан в комплектации;
- Кол-во материалов в спецификации посчитано БЕЗ ЗАПАСА;
- Все отверстия в потолке под осветительные приборы выполнять после покупки освещения;
- Учесть высоту встраиваемых светильников и других приборов;

Спецификация потолков

Тип	УГО	Описание	S, кв.м
ПТ2		Подвесной потолок, ГКЛ	78.17 m²
ПТ3		Подвесной потолок, ГКЛВ	7.31 m²

Экспликация помещений

№	Наименование	S, кв.м.
1	Прихожая	6.90
2	Кухня-гостиная	39.75
4	Спальня	14.10
5	Лоджия	6.70
6	Детская	14.00
7	Ванная	7.25
		88.70

IVANCHUKINTERIOR

НАИМЕНОВАНИЕ ЧЕРТЕЖА / DRAWING TITLE

ПЛАН ПОТОЛКА

№ ЛИСТА/ DRAWING NO: 13

ВЫПОЛНИЛ/ DRAWN BY	ИВАНЧУК А.Ю.
ДАТА/ DATE	13.02.2026
ГОРОД/ CITY	МИНСК

Сечение 1-1

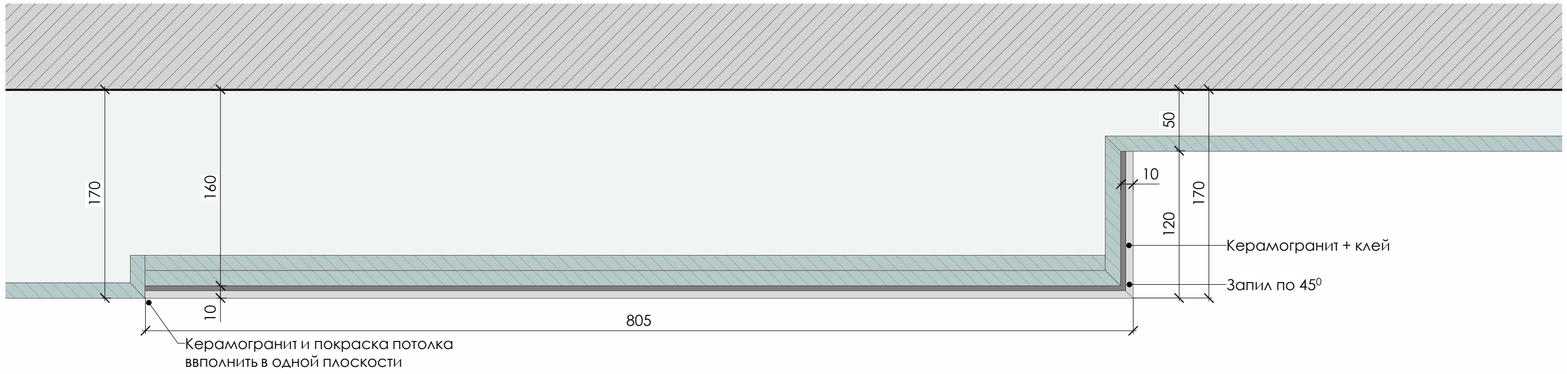

Сечение 2-2

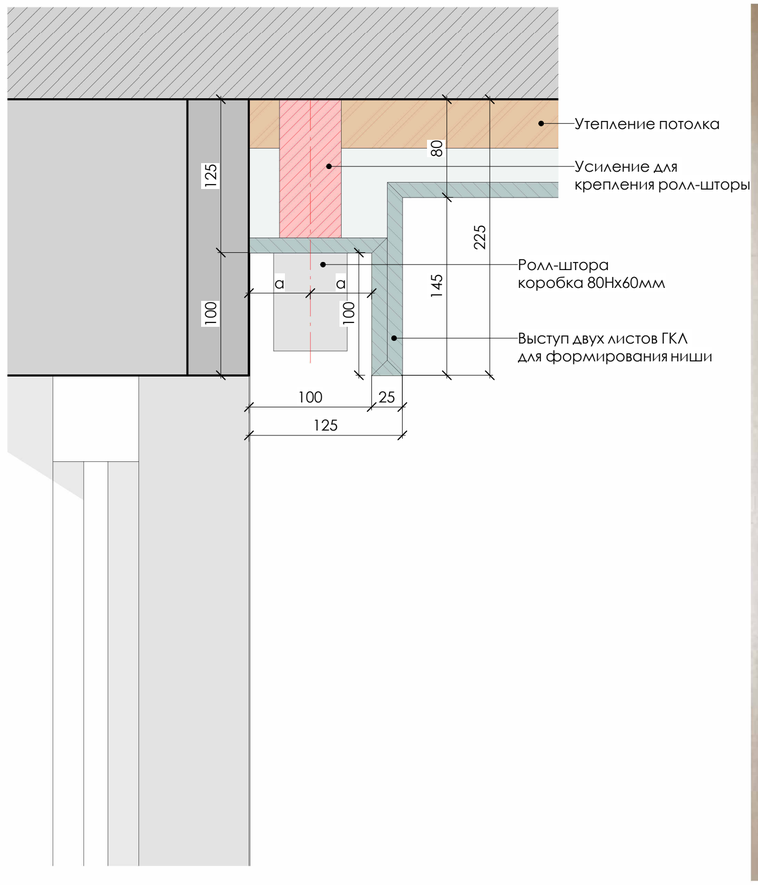

Сечение 3-3

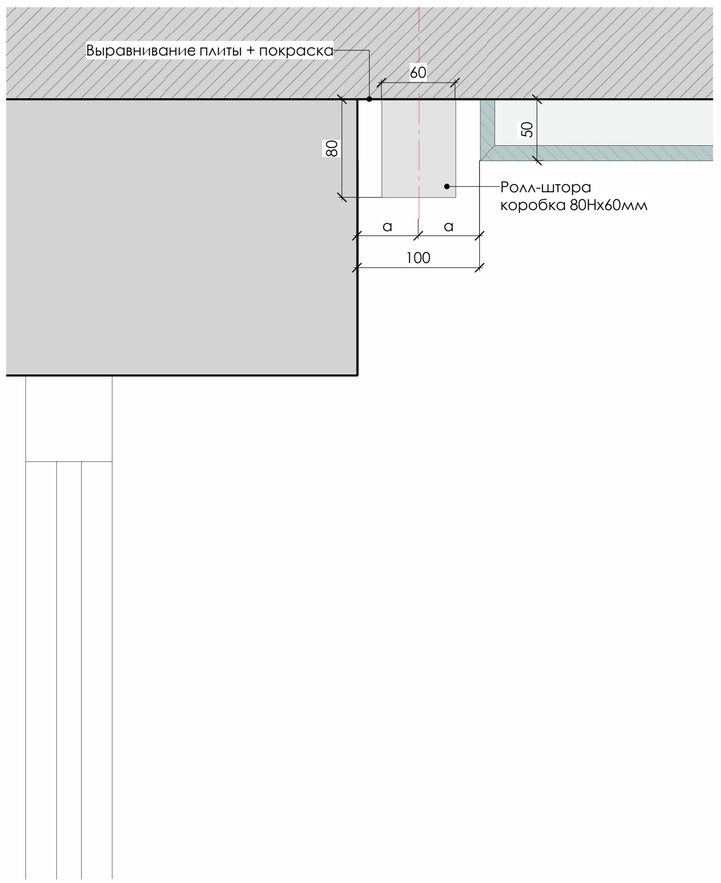

IVANCHUKINTERIOR

НАИМЕНОВАНИЕ ЧЕРТЕЖА / DRAWING TITLE

СЕЧЕНИЯ ПОТОЛКА.

№ ЛИСТА/ DRAWING NO	13.1	ВЫПОЛНИЛ/ DRAWN BY	ИВАНЧУК А.Ю.
		ДАТА/ DATE	13.02.2026
		ГОРОД/ CITY	МИНСК

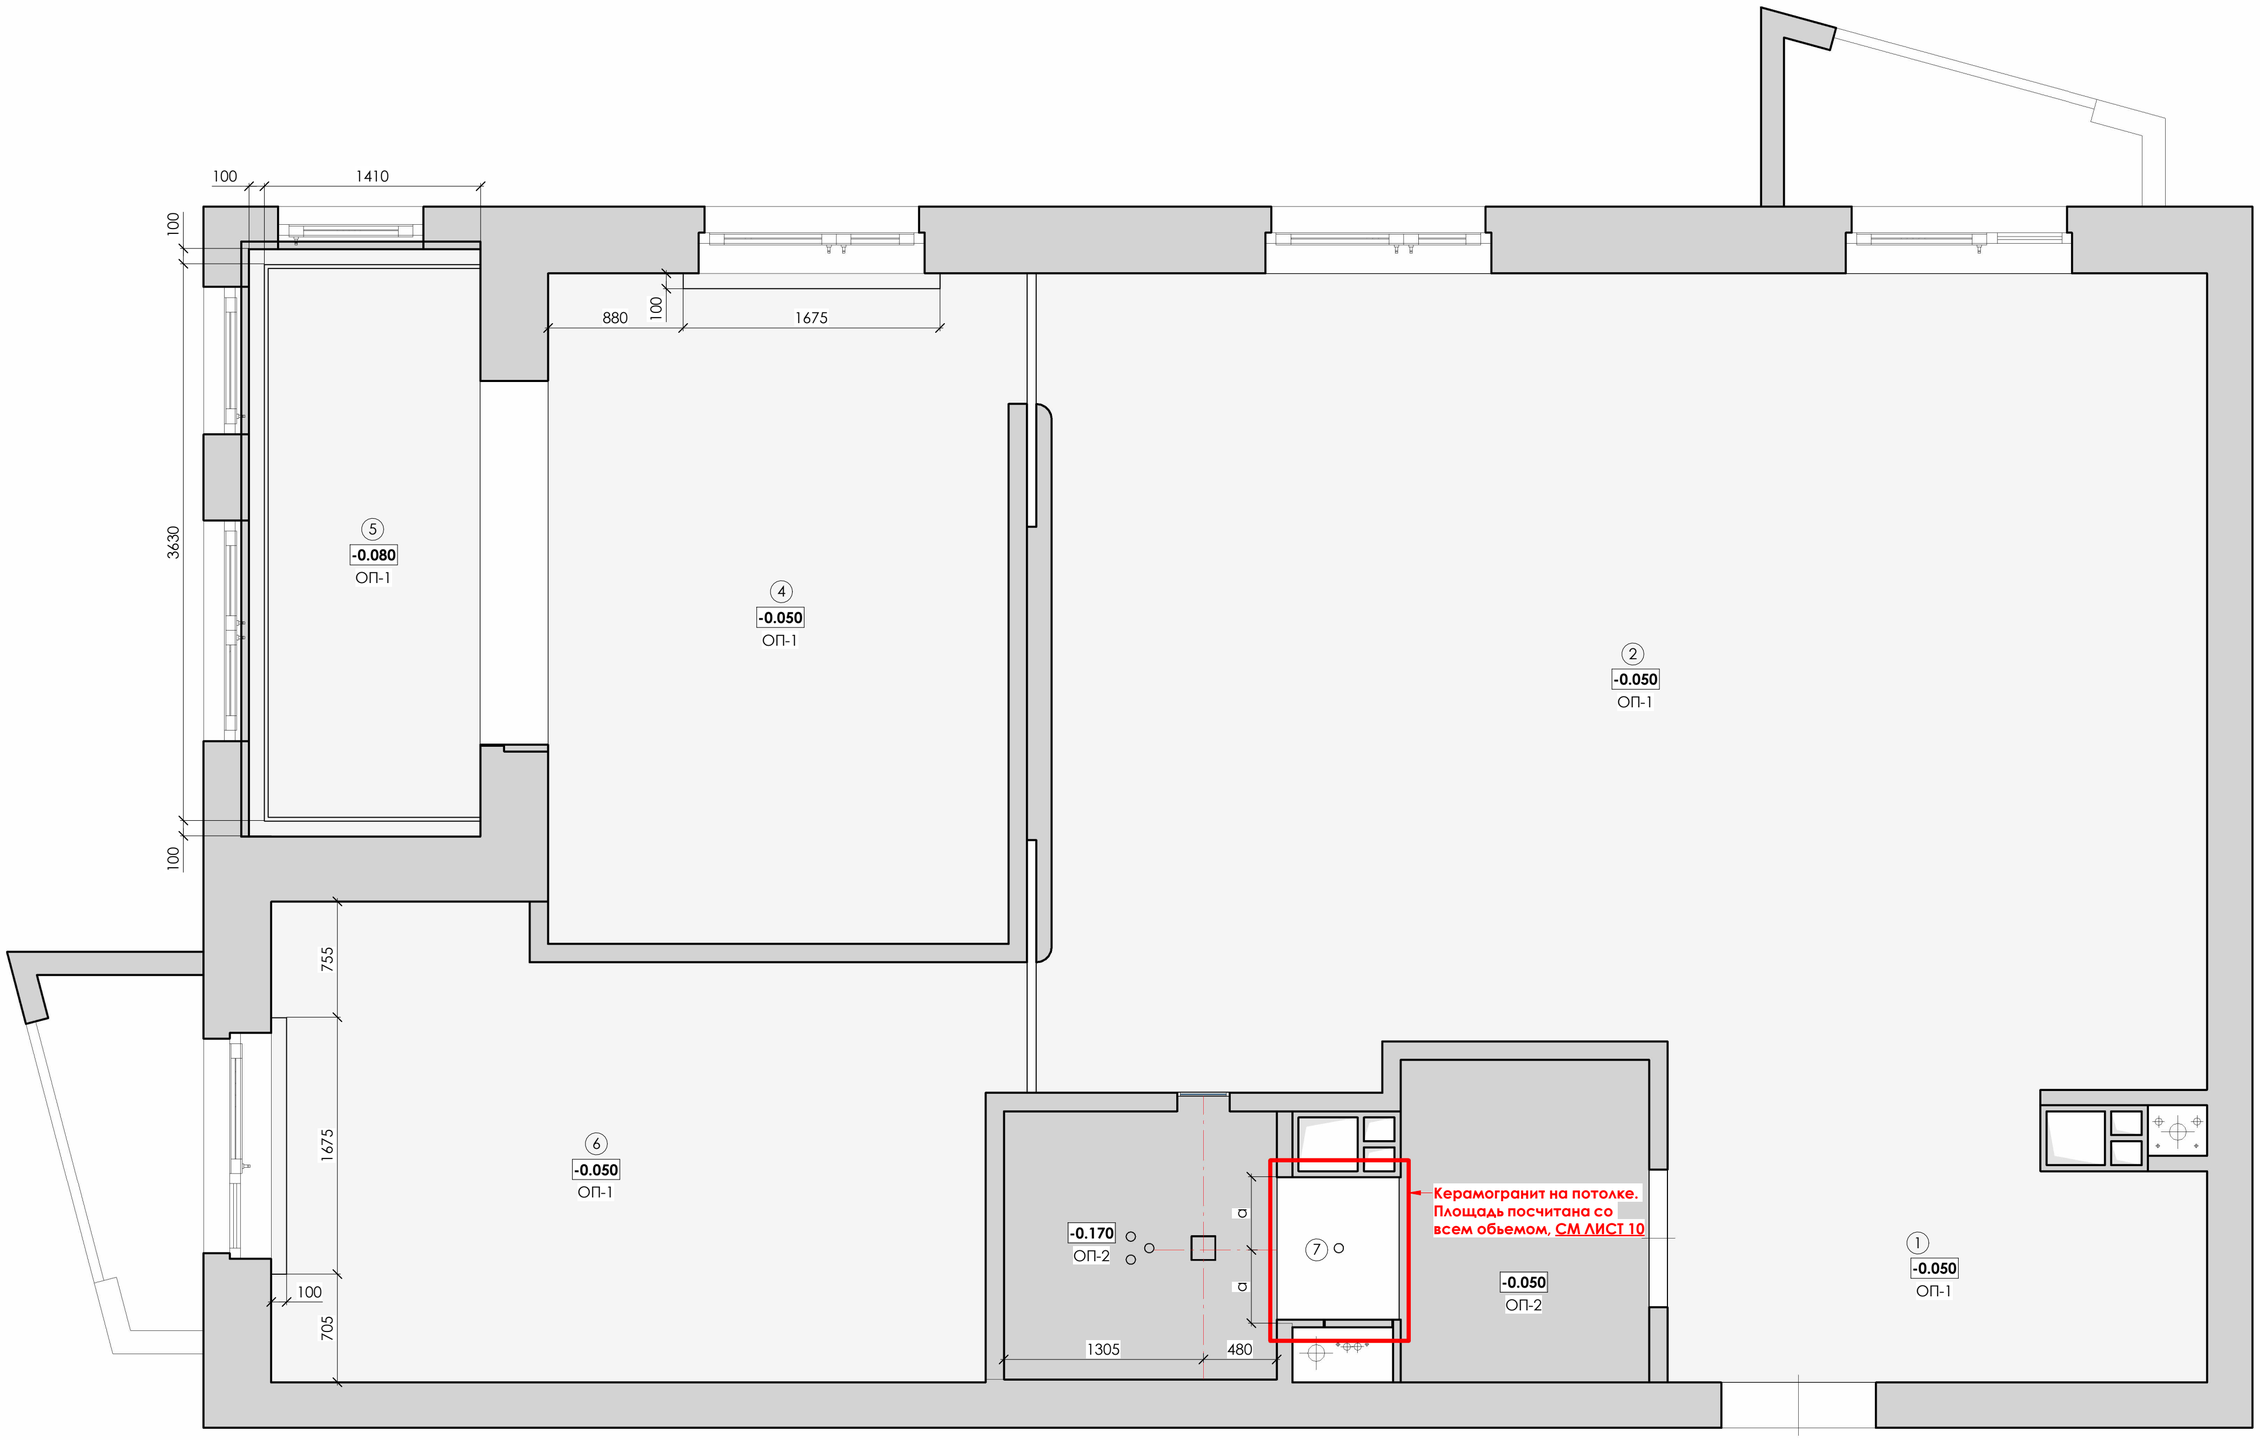

Примечания:

- Отметка 0,000 соответствует отметке верхнего перекрытия;
- Точный цвет краски указан в комплектации;
- Кол-во материалов в спецификации посчитано БЕЗ ЗАПАСА;
- Все отверстия в потолке под осветительные приборы выполнять после покупки освещения;
- Учесть высоту встраиваемых светильников и других приборов;

Спецификация отделки потолка

Тип	УГО	Описание	S, кв.м
ОП-1		Покраска в цвет стен	78.51 m²
ОП-2		Покраска влагостойкой краской	6.57 m²

Экспликация помещений

№	Наименование	S, кв.м.
1	Прихожая	6.90
2	Кухня-гостиная	39.75
4	Спальня	14.10
5	Лоджия	6.70
6	Детская	14.00
7	Ванная	7.25
		88.70

IVANCHUKINTERIOR

НАИМЕНОВАНИЕ ЧЕРТЕЖА / DRAWING TITLE

ПЛАН ПОТОЛКА С ОТДЕЛКОЙ

№ ЛИСТА/ DRAWING NO: 13.2

ВЫПОЛНИЛ/ DRAWN BY	ИВАНЧУК А.Ю.
ДАТА/ DATE	13.02.2026
ГОРОД/ CITY	МИНСК

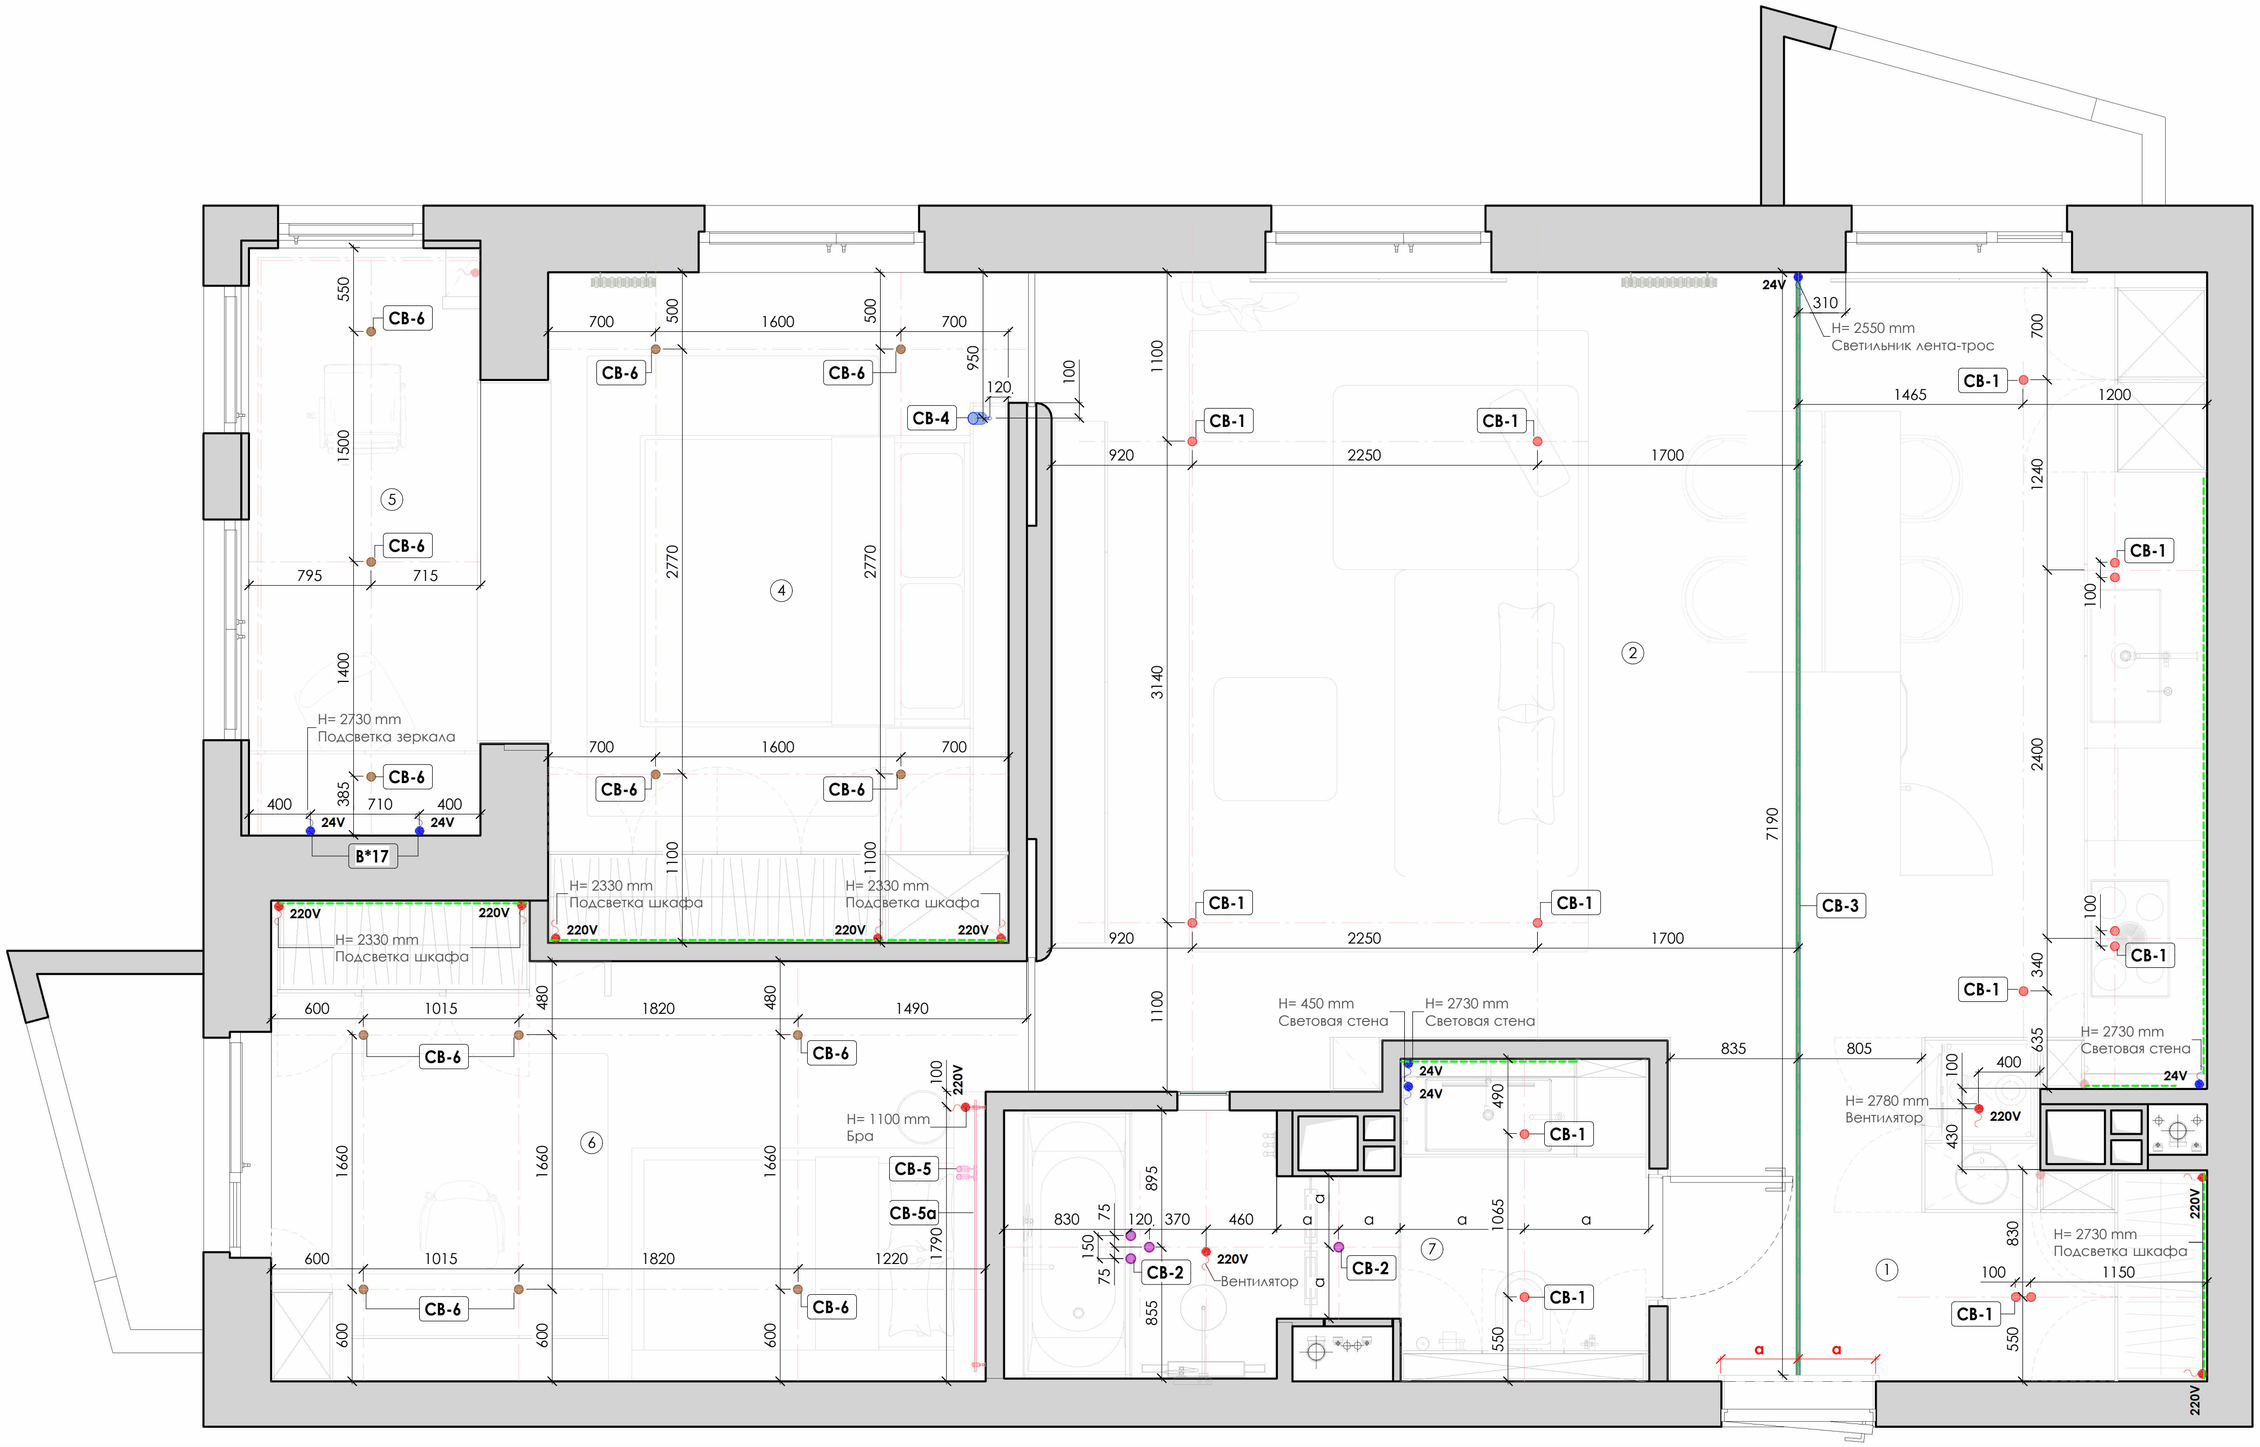

Условные обозначения:

- 1 - марка обозначения помещений
- - существующие стены
- - радиатор отопления
- - шахта
- - канализация, хол. , гор. водоснабжение
- Накладной светильник
- Встраиваемый светильник
- Лента-тросс
- Напольно-подвесной светильник
- Бра
- Накладной светильник
- LED подсветка
- Вывод кабеля 24V
- Вывод кабеля 220V

Примечания:

- Все высоты указаны от чистового пола;
- Вопросы согласовать с заказчиком или представителем авторского надзора.

Экспликация помещений

№	Наименование	S, кв.м.
1	Прихожая	6.90
2	Кухня-гостиная	39.75
4	Спальня	14.10
5	Лоджия	6.70
6	Детская	14.00
7	Ванная	7.25
		88.70

IVANCHUKINTERIOR

НАИМЕНОВАНИЕ ЧЕРТЕЖА / DRAWING TITLE

ПЛАН ОСВЕЩЕНИЯ С ПРИВЯЗКАМИ

№ ЛИСТА/ DRAWING NO	14	ВЫПОЛНИЛ/ DRAWN BY	ИВАНЧУК А.Ю.
		ДАТА/ DATE	13.02.2026
		ГОРОД/ CITY	МИНСК

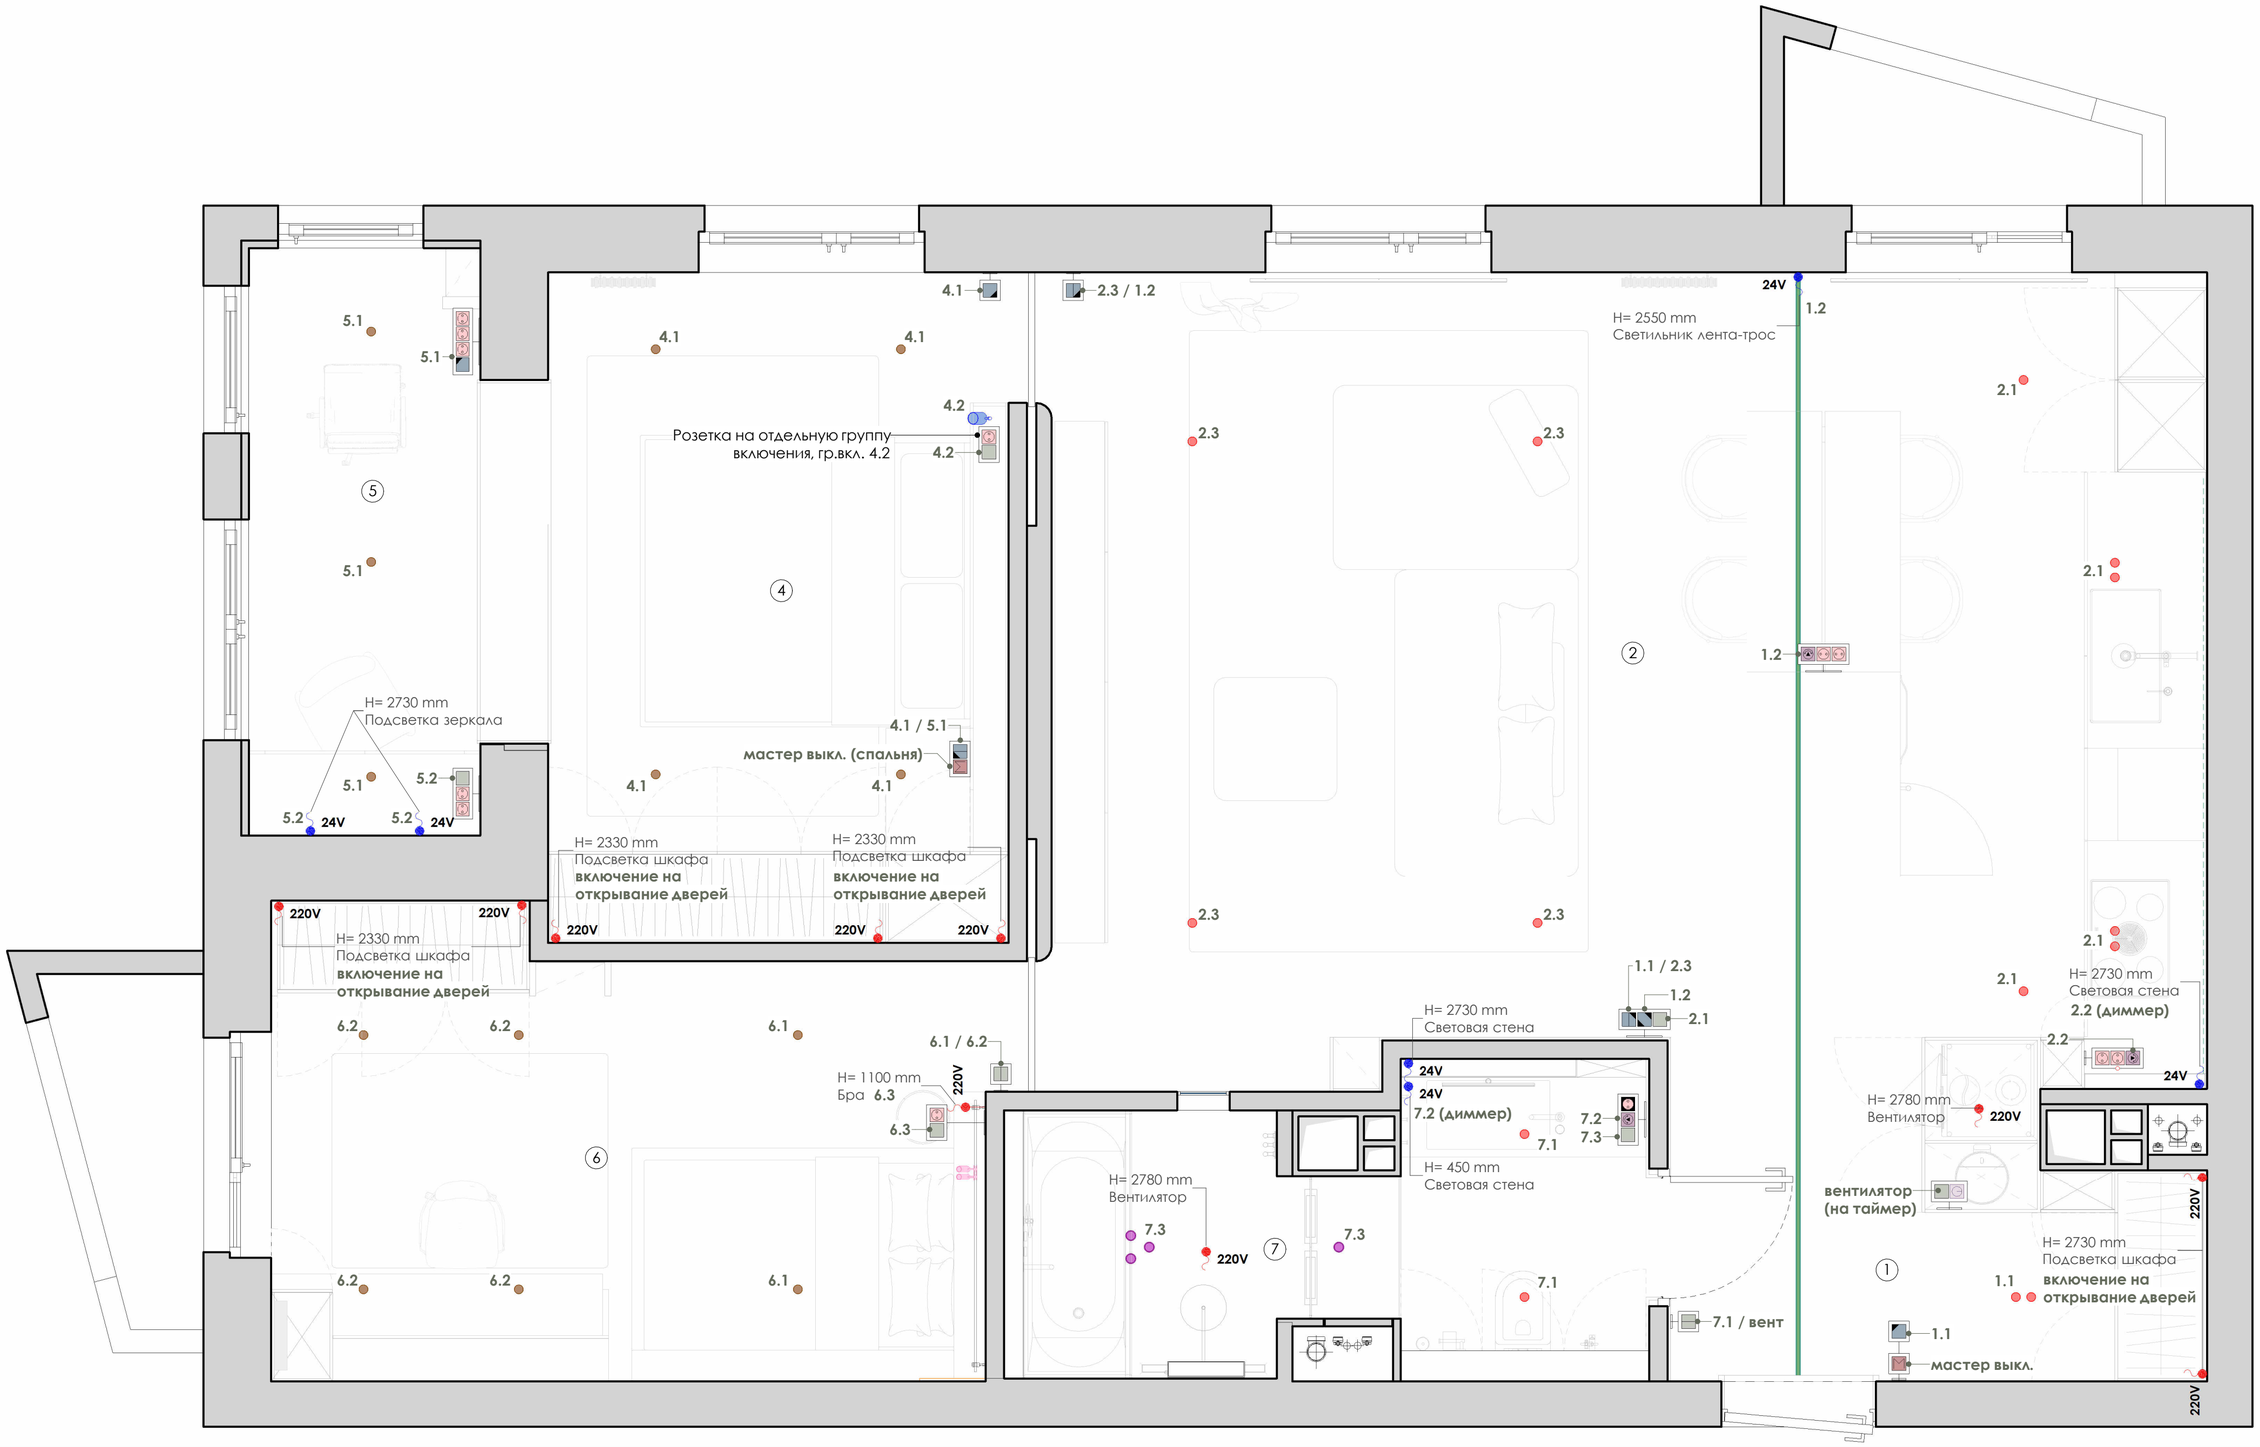

Условные обозначения:

- 1 - марка обозначения помещений
- - существующие стены
- - радиатор отопления
- - шахта
- - канализация, хол. , гор. водоснабжение

- Накладной светильник
- Встраиваемый светильник
- Лента-тросс
- Напольно-подвесной светильник
- Бра
- Накладной светильник
- LED подсветка
- Вывод кабеля 24V
- Вывод кабеля 220V

- Выключатель одноклавишный
- Выключатель двухклавишный
- Переключатель одноклавишный
- Переключатель двухклавишный
- Перекрестный одноклавишный выключатель
- Диммер
- Мастер выключатель

Экспликация помещений

№	Наименование	S, кв.м.
1	Прихожая	6.90
2	Кухня-гостиная	39.75
4	Спальня	14.10
5	Лоджия	6.70
6	Детская	14.00
7	Ванная	7.25
		88.70

IVANCHUKINTERIOR

НАИМЕНОВАНИЕ ЧЕРТЕЖА / DRAWING TITLE

СХЕМА ВЫКЛЮЧЕНИЯ СВЕТИЛЬНИКОВ

№ ЛИСТА/ DRAWING NO: 15

ВЫПОЛНИЛ/ DRAWN BY	ИВАНЧУК А.Ю.
ДАТА/ DATE	13.02.2026
ГОРОД/ CITY	МИНСК

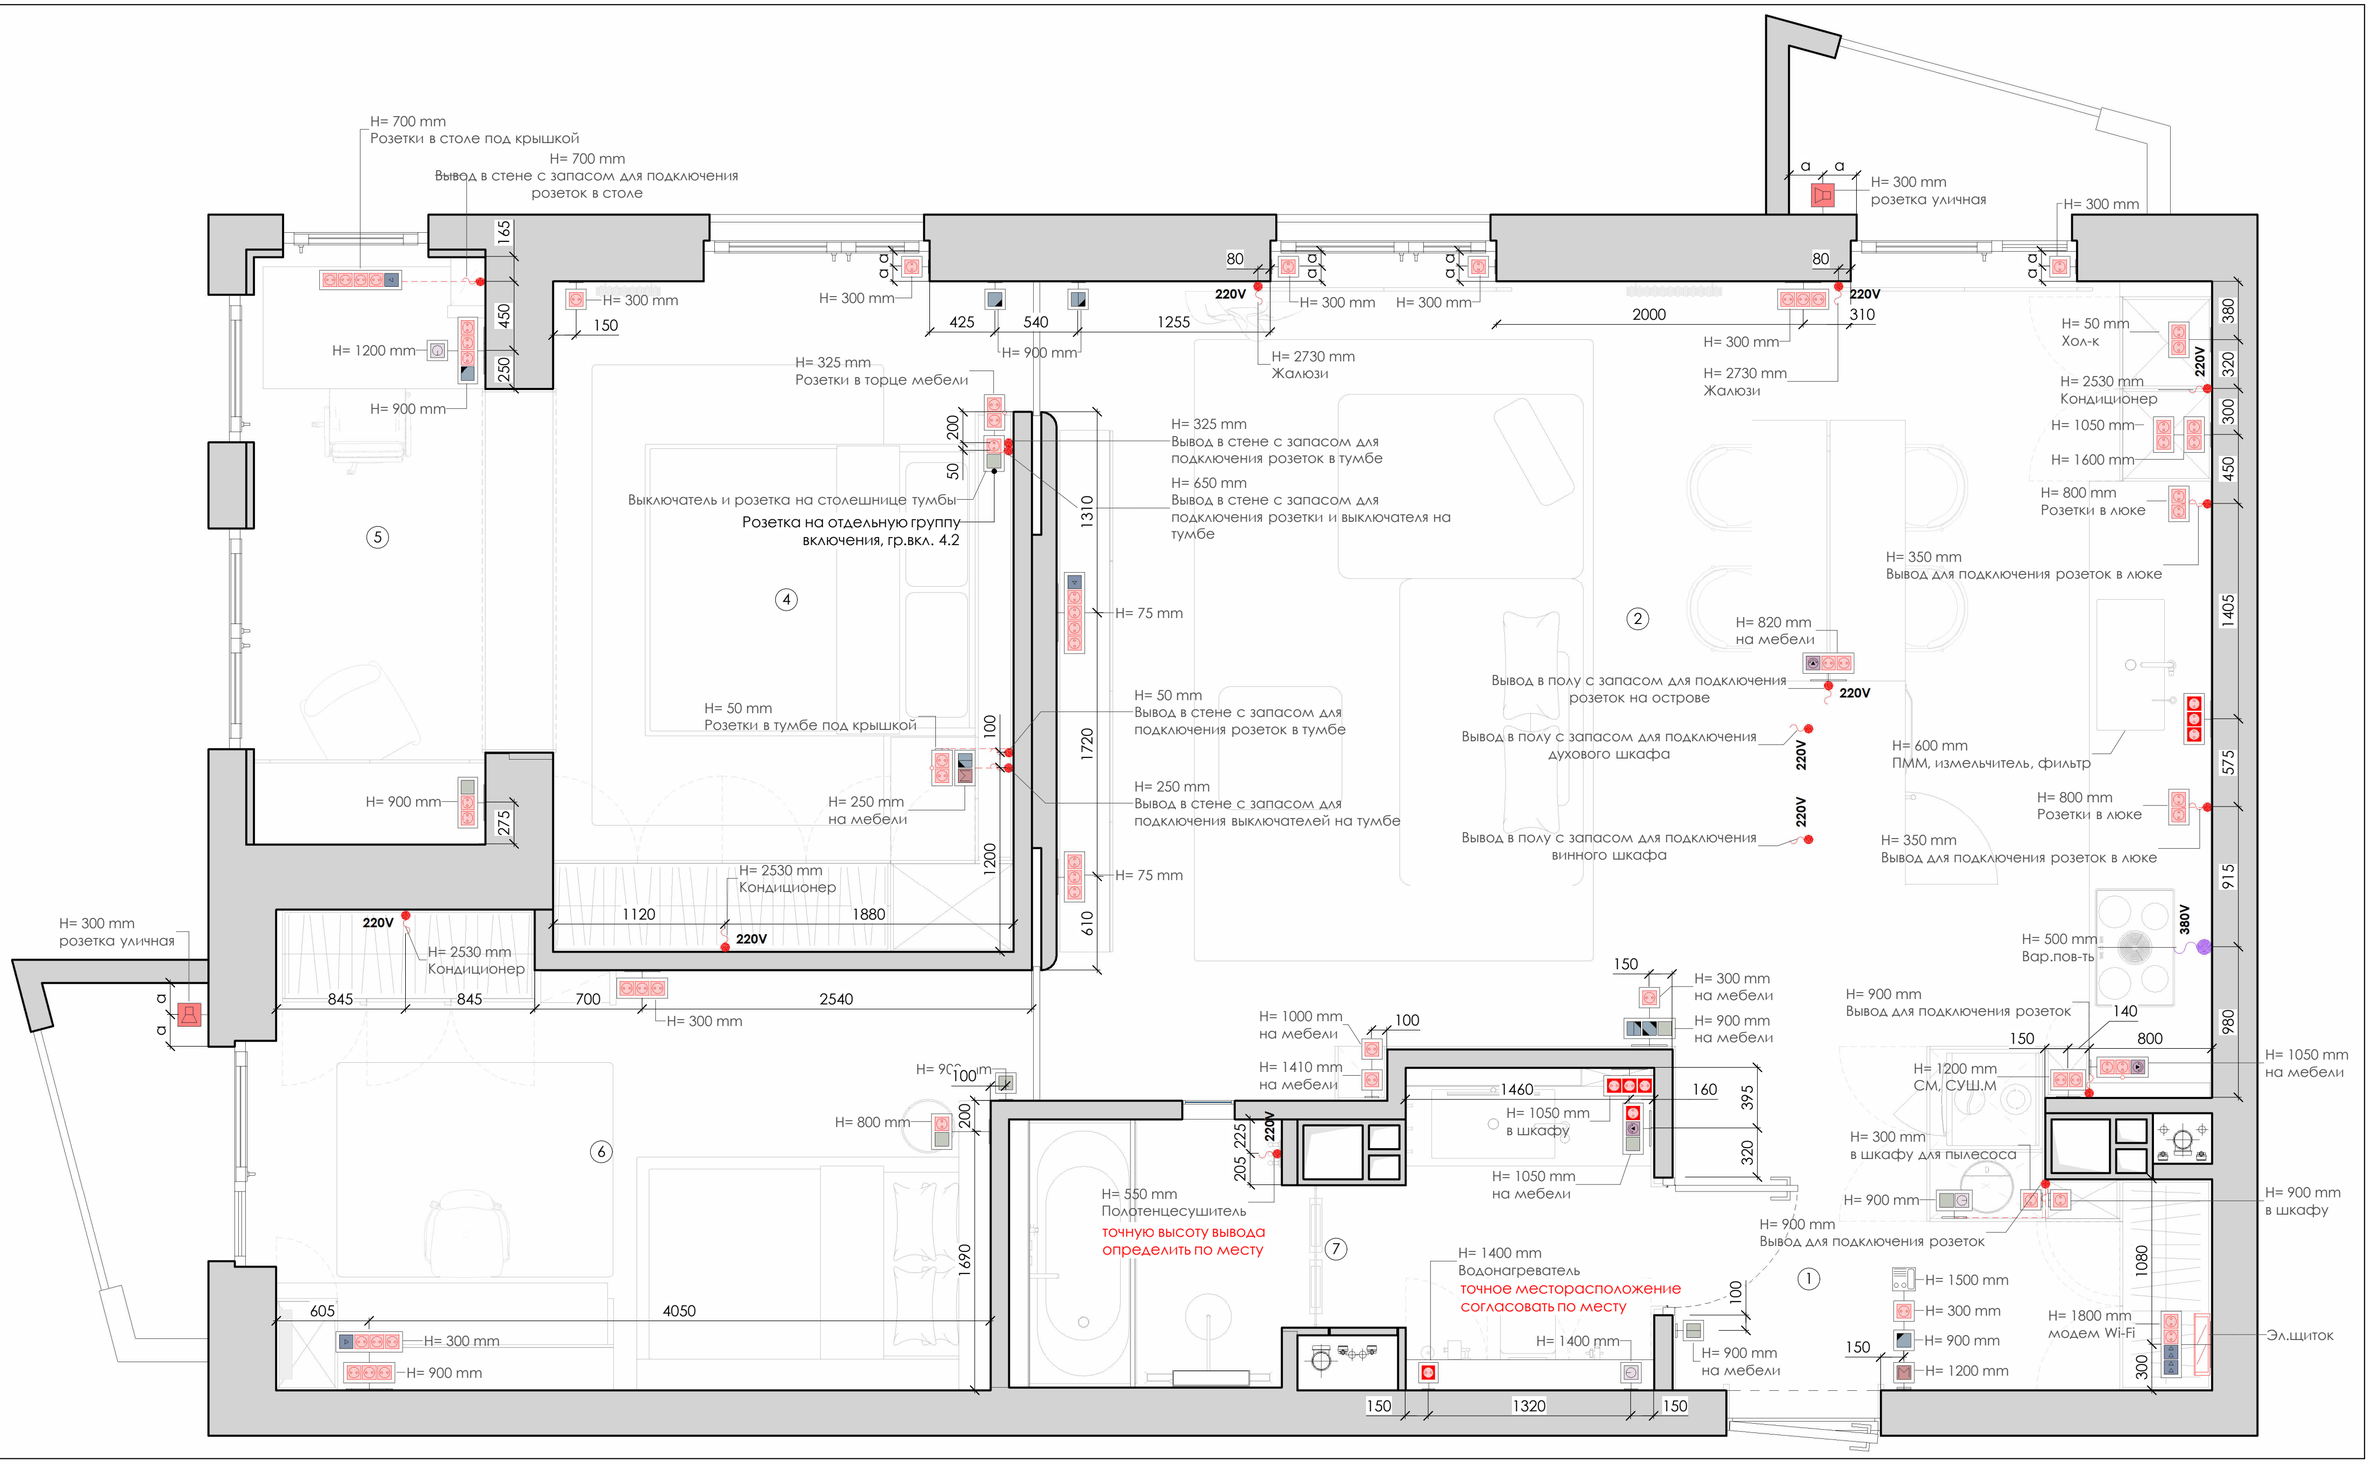

Примечания:

- Высота розеток - 300мм от ур.ч.п. (если не указана другая).
- Высота выключателей - 900мм от ур.ч.п. (если не указана другая).
- Привязки указаны по оси выключателей или их блоков.
- Расчет энергопотребления дает специалист-электрик с лицензией на эти виды работ
- Окончательные выводы для кухонной техники определяются после заказа кухни (проект кухни должен быть утвержден до начала строительства)
- Все высоты указаны от чистового пола.
- Разметку розеток провести совместно с заказчиком или представителем авторского надзора.
- Перед проведением работ согласовать тип, марку и цвет розеток с заказчиком или представителем авторского надзора.
- ПЕРЕПРОВЕРИТЬ кол-во рамок и розеток по факту.
- Вопросы согласовать с заказчиком или представителем авторского надзора.

Условные обозначения

- Домофон
- Вывод кабеля 220V
- Вывод кабеля 380V
- Выключатель одноклавишный
- Выключатель двухклавишный
- Переключатель одноклавишный
- Переключатель двухклавишный
- Перекрестный одноклавишный выключатель
- Электрощиток, слаботочный щиток
- Мастер выключатель
- Диммер
- Интернет розетка RJ45 1x
- Интернет розетка RJ45 2x
- Розетка 220V
- Розетка 220V IP44 влагозащищенная
- Терморегулятор
- Розетка уличная

Экспликация помещений

№	Наименование	S, кв.м.
1	Прихожая	6.90
2	Кухня-гостиная	39.75
4	Спальня	14.10
5	Лоджия	6.70
6	Детская	14.00
7	Ванная	7.25
		88.70

IVANCHUKINTERIOR

НАИМЕНОВАНИЕ ЧЕРТЕЖА / DRAWING TITLE

ПЛАН РАССТАНОВКИ РОЗЕТОК И ВЫКЛЮЧАТЕЛЕЙ

№ ЛИСТА/ DRAWING NO: 16

ВЫПОЛНИЛ/ DRAWN BY	ИВАНЧУК А.Ю.
ДАТА/ DATE	13.02.2026
ГОРОД/ CITY	МИНСК

Спецификация осветительных приборов (шт.)

Тип		Тип светильника	Комментарии к типоразмеру	Кол-во, шт
СВ-1		Накладной светильник	Фабрика: Denkirs Название: Shine Tube DK2615-DN Размеры: Ø 45 × H 115 мм Мощность: 7 Вт Цветовая температура: 3000 K Степень защиты: IP20	14
СВ-2		Встраиваемый светильник	Фабрика: Maytoni Название: DL034-2-L12W (Zoom downlight) Размеры: Ø 85 × H 85 мм; монтажное отверстие Ø 75 мм Мощность: 12 Вт Цветовая температура: 3000 K Степень защиты: IP65	4
СВ-3		Лента-трос	Фабрика: ST Luce Название: Ray ST961.437.09 (тросовая световая система) Размеры: длина системы 12000 мм Мощность: 8,7 Вт LED Цветовая температура: 3000 K Степень защиты: IP20	1
СВ-4		Напольно-подвесной светильник	Фабрика: Lodes Название: Cima Pendant / Floor Lamp Размеры: Ø 60 × H 140 мм (корпус); максимальная высота системы до 4300 мм Мощность: 1×10 Вт (GU10 LED) Цветовая температура: определяется лампой Степень защиты: IP20	1
СВ-5		Бра	Фабрика: Maytoni Название: TR144-1-12W3K-W-PT (Focus LED Flarity) Размеры: Ø 55 × H 203 мм Мощность: 12 Вт Цветовая температура: 3000 K Степень защиты: IP20	2
СВ-5а			Фабрика: Maytoni Название: TRX154-112PT (шинопровод Flarity, магнитная система) Размеры: L 2000 × Ш 8,5 × В 15 мм Мощность: — Цветовая температура: — Степень защиты: IP20	1
СВ-6		Накладной светильник	Фабрика: Maytoni Название: C052CL-01W (Focus S) Размеры: Ø 52 × H 100 мм Мощность: 1×10 Вт (GU10) Цветовая температура: определяется лампой Степень защиты: IP20	13

Спецификация розеток и выключателей

УГО	Описание	Кол-во, шт
	Аудиодомофон	1
	Вывод кабеля 24V	6
	Вывод кабеля 220V	28
	Вывод кабеля 380V	1
	Выключатель двухклавишный	2
	Выключатель одноклавишный	6
	Выключатель одноклавишный (мастер)	2
	Диммер	3
	Интернет розетка RJ45 1x	3
	Интернет розетка RJ45 2x	2
	Переключатель двухклавишный	3
	Переключатель одноклавишный	3
	Перекрестный переключатель одноклавишный	1
	Розетка 220V	63
	Розетка 220V IP44 влагозащищенная	8
	Терморегулятор теплого пола	3
	Уличная розетка 220V	2
	Электрощиток. слаботочный щиток	1

Спецификация рамок44

УГО	Описание	Кол-во, шт
	Рамка на 1 пост	20
	Рамка на 2 поста	12
	Рамка на 3 поста	11
	Рамка на 4 поста	3
	Рамка на 5 постов	2

Спецификация осветительных приборов (пог.м.)

Тип	УГО	Описание	Кол-во, пог.м.
B*17		PR-SF-SL-1612 Светодиодный профиль Byled накладной. 2000*17*12мм.	3.8

IVANCHUKINTERIOR

НАИМЕНОВАНИЕ ЧЕРТЕЖА / DRAWING TITLE

СПЕЦИФИКАЦИИ ЭЛЕКТОРООБОРУДОВАНИЯ

№ ЛИСТА/ DRAWING NO: 16.1

ВЫПОЛНИЛ/ DRAWN BY	ИВАНЧУК А.Ю.
ДАТА/ DATE	13.02.2026
ГОРОД/ CITY	МИНСК

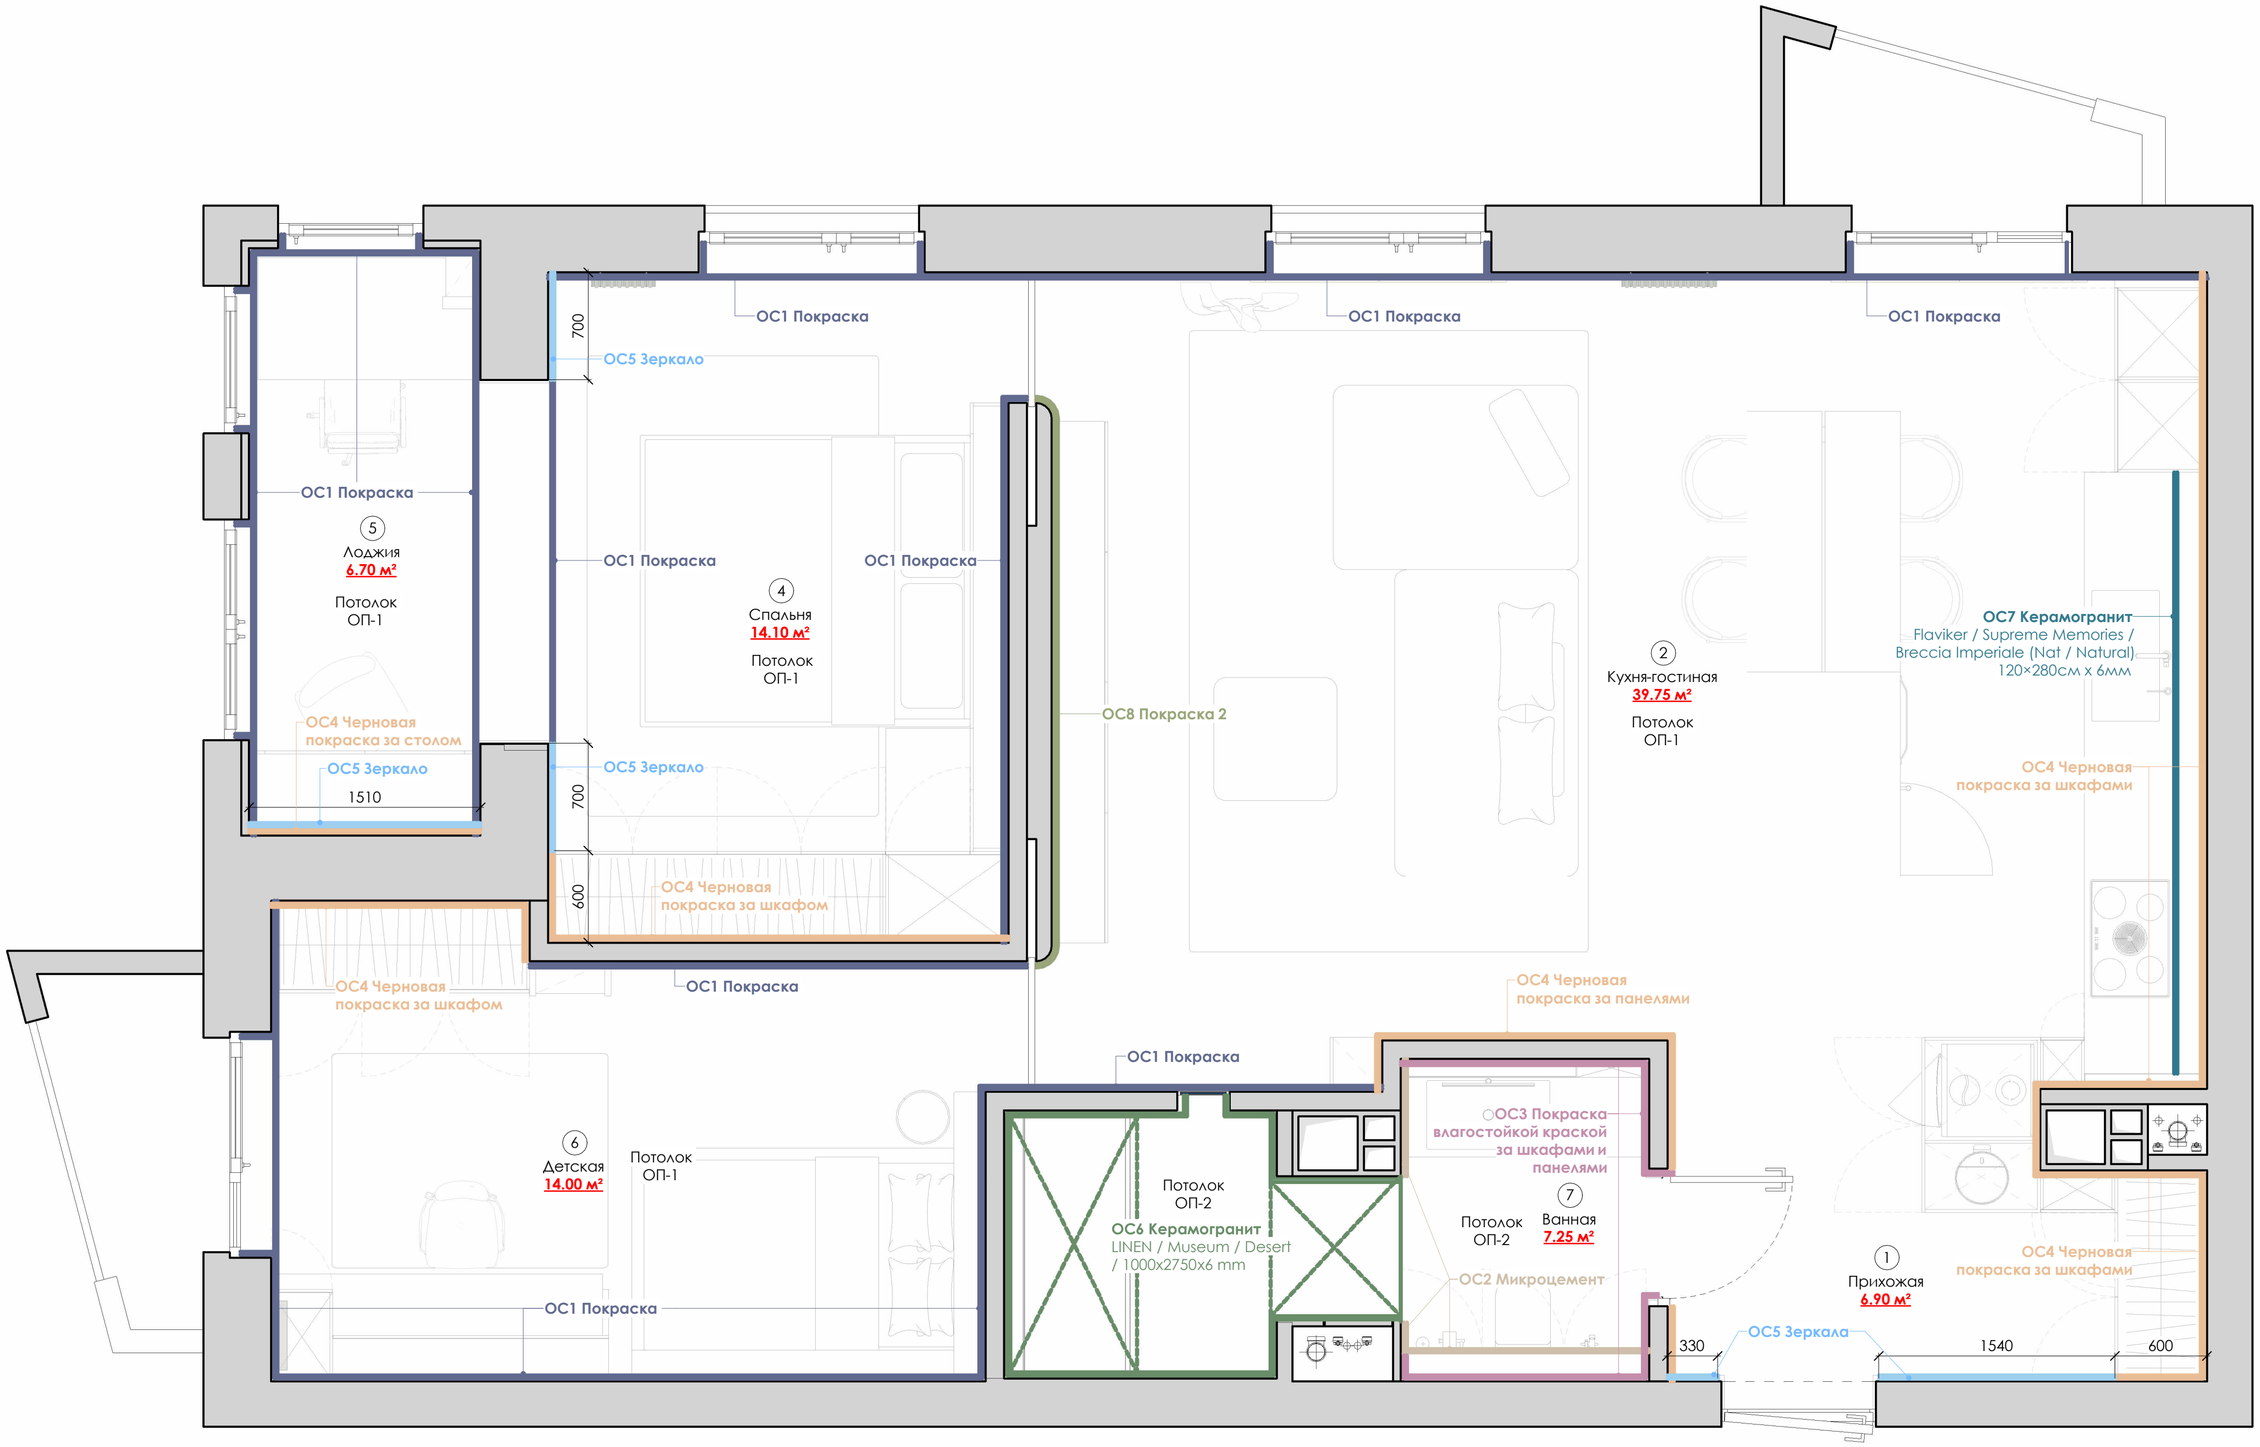

Условные обозначения:

- 1 - марка обозначения помещений
- - существующие стены
- - радиатор отопления
- - шахта
- - канализация, хол. , гор. водоснабжение

Примечания:

- За отметку 0.000 принята отметка чистого пола квартиры;
- Все размеры уточняются по месту;
- Перед окраской стен, сделать выкрасы, цвет согласовать с заказчиком и автором проекта;
- Образец затирки для керамогранита согласовать в режиме авторского надзора;
- Смотреть совместно с развертками помещений / визуализациями помещений.

Спецификация отделки потолка .

Тип	Описание	S, кв.м
ОП-1	Покраска в цвет стен	78.51 m²
ОП-2	Покраска влагостойкой краской	6.57 m²

Спецификация отделочных материалов

Тип	УГО	Описание	S, кв.м.
ОС1		Покраска	80.3
ОС2		Микроцемент	7.3
ОС3		Покраска влагостойкой краской	13.1
ОС4		Черновая покраска	54.5
ОС5		Зеркало, 4мм	11.7
ОС8		Покраска 2	10.2
ОС6		Керамогранит LINEN / Museum / Desert / 1000x2750x6 mm	28.0
ОС7		Керамогранит Flaviker / Supreme Memories / Breccia Imperiale (Nat / Natural) / 120×280см x 6мм	24.5

Экспликация помещений

№	Наименование	S, кв.м.
1	Прихожая	6.90
2	Кухня-гостиная	39.75
4	Спальня	14.10
5	Лоджия	6.70
6	Детская	14.00
7	Ванная	7.25
		88.70

IVANCHUKINTERIOR

НАИМЕНОВАНИЕ ЧЕРТЕЖА / DRAWING TITLE

ПЛАН ОТДЕЛКИ СТЕН

№ ЛИСТА/ DRAWING NO	17	ВЫПОЛНИЛ/ DRAWN BY	ИВАНЧУК А.Ю.
		ДАТА/ DATE	13.02.2026
		ГОРОД/ CITY	МИНСК

ВИД 1.1

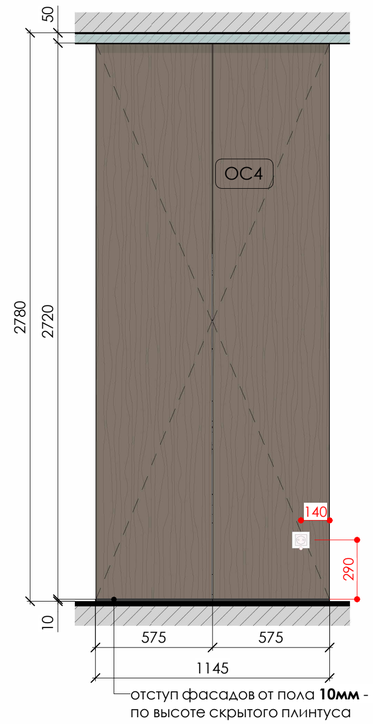

ВИД 1.2

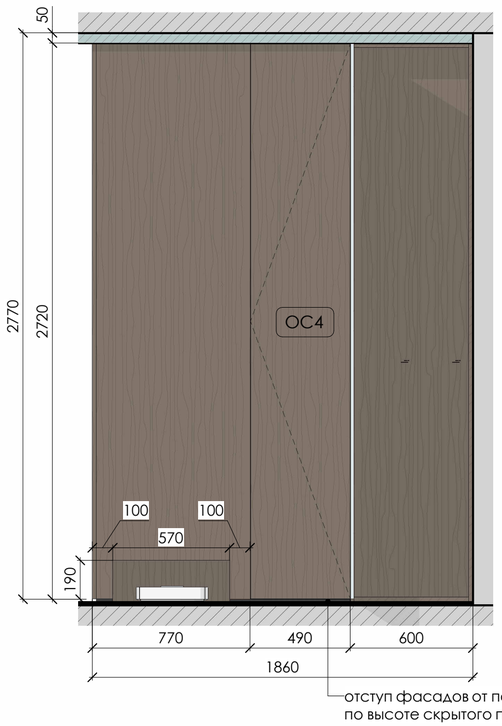

ВИД 1.3

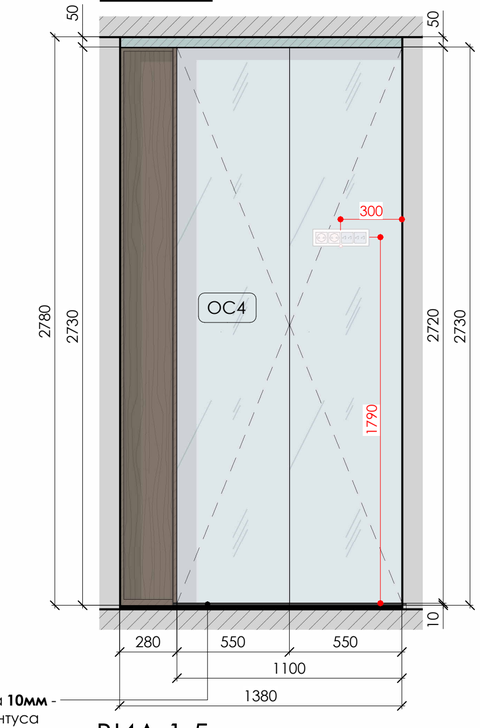

ВИД 1.4

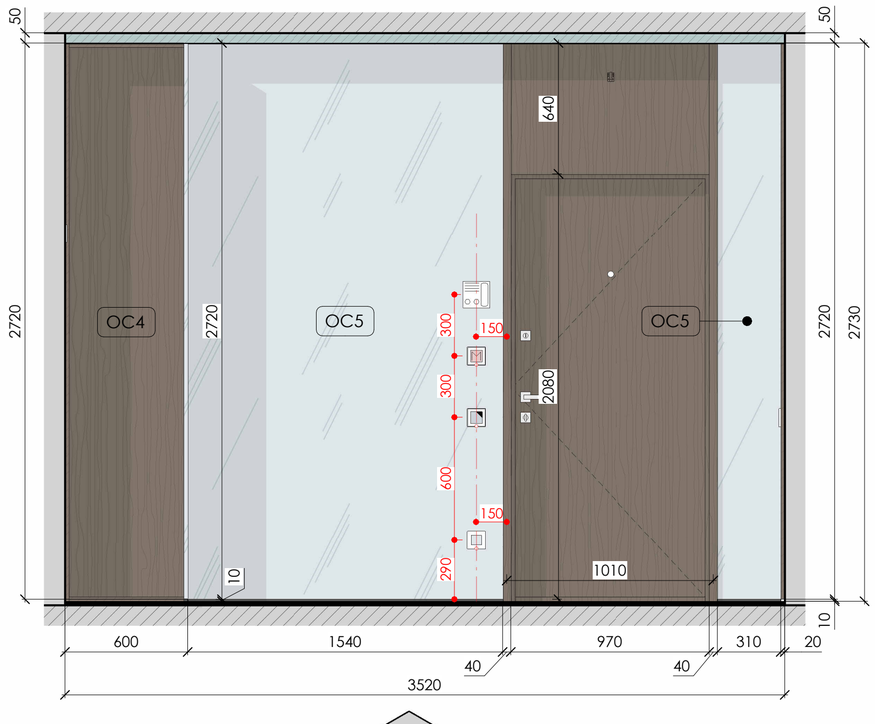

ВИД 1.5

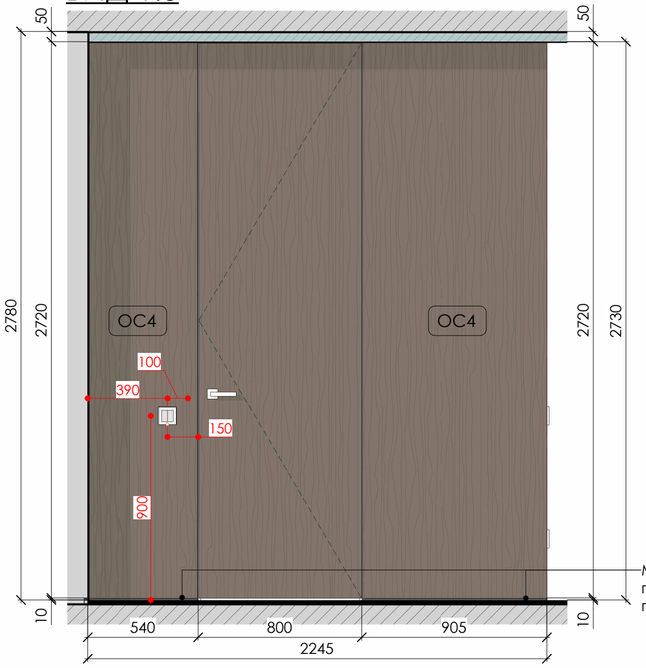

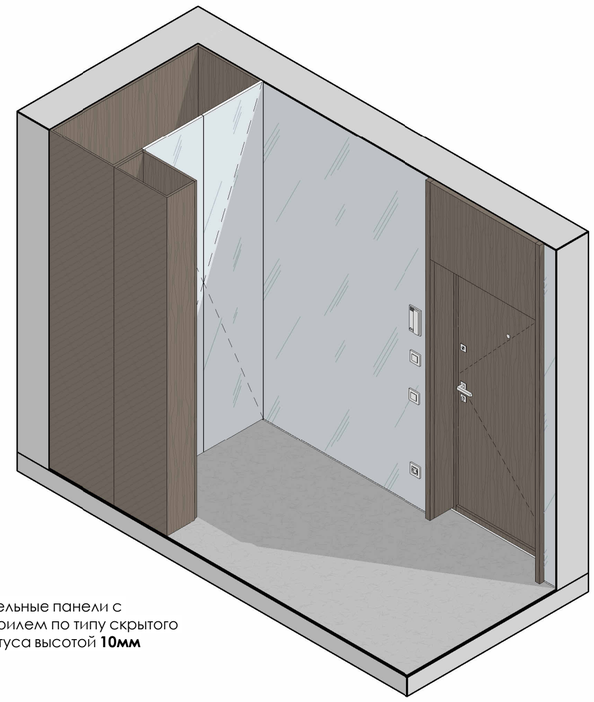

ПОМ. 1, ПРИХОЖАЯ

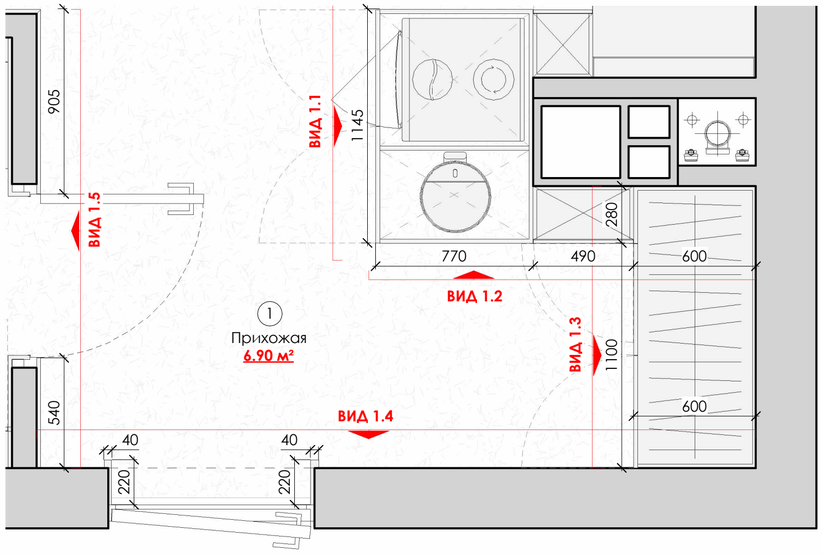

Примечания:

- Все отделочные материалы должны быть выполнены в единой плоскости. При установке материалов учесть их толщину и соблюдение допусков для предотвращения неровностей и зазоров.
- Мебель и встроенные элементы должны быть установлены в соответствии с проектом. Все размеры и положения, указанные в проекте, подлежат перепроверке на этапе монтажа.
- Расположение осветительных приборов, выключателей и розеток соответствует проекту. Необходимо обеспечить правильную высоту установки и проверить расположение электрических точек в реальных условиях.
- До покупки полного объема краски выполнить предварительные выкрасы на небольших участках для проверки цвета и покрытия.

Зеркало

Шпон

IVANCHUKINTERIOR

НАИМЕНОВАНИЕ ЧЕРТЕЖА / DRAWING TITLE

РАЗВЕРТКА ПРИХОЖЕЙ

№ ЛИСТА/ DRAWING NO	18	ВЫПОЛНИЛ/ DRAWN BY	ИВАНЧУК А.Ю.
		ДАТА/ DATE	13.02.2026
		ГОРОД/ CITY	МИНСК

ВИД 2.1

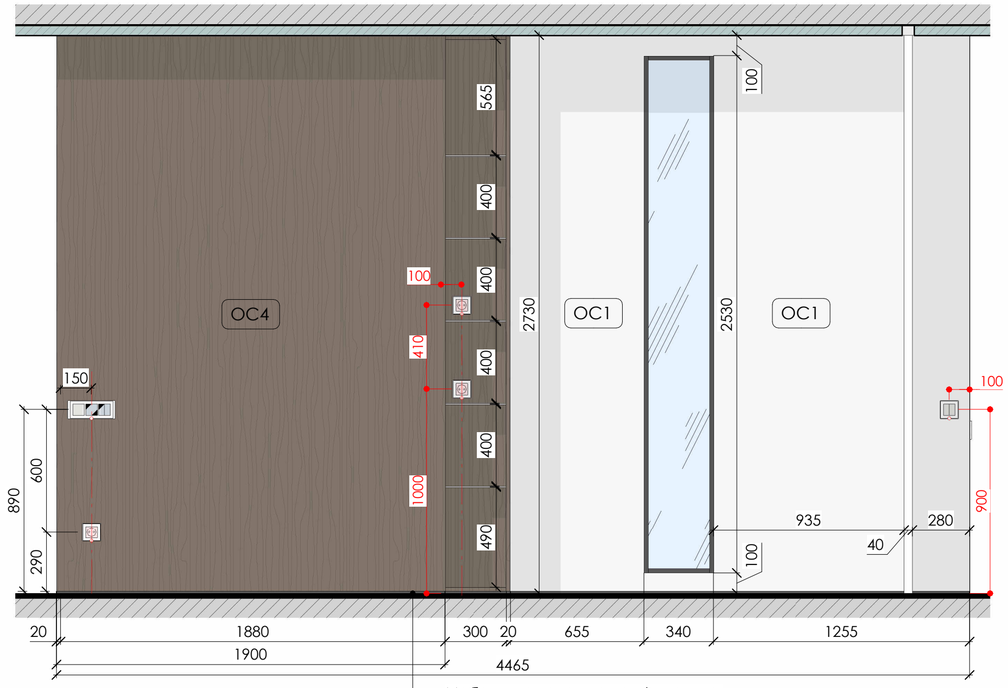

Мебельные панели с прифилем по типу скрытого плинтуса высотой **10мм**

ВИД 2.2

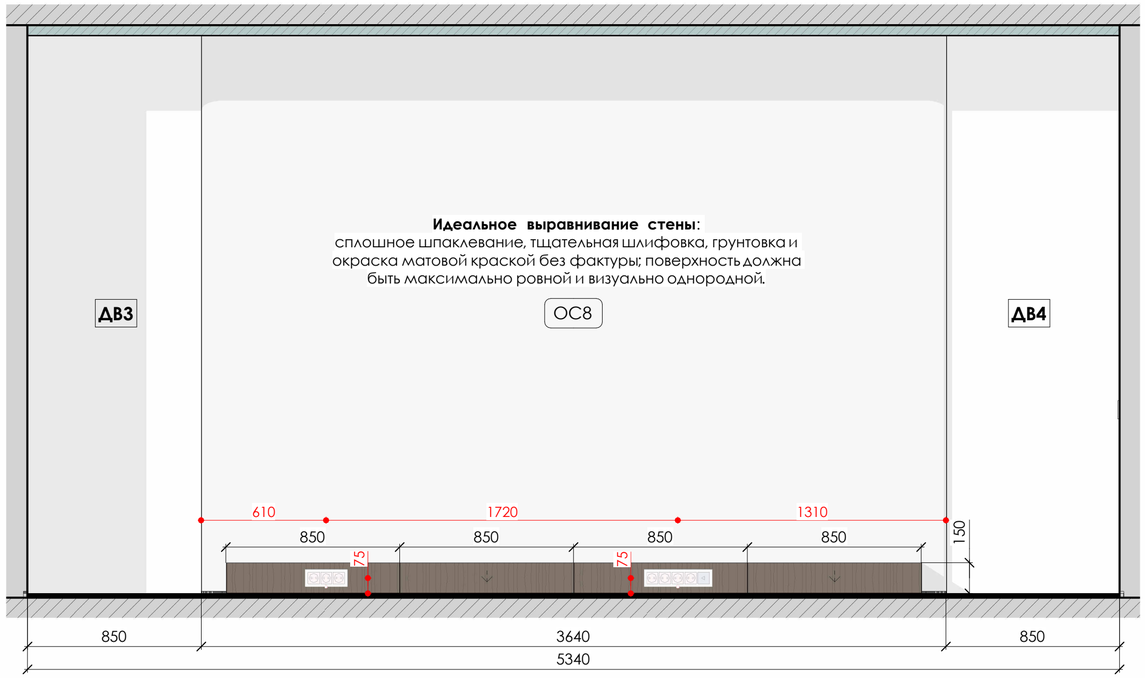

ПОМ. 2, КУХНЯ ГОСТИНАЯ

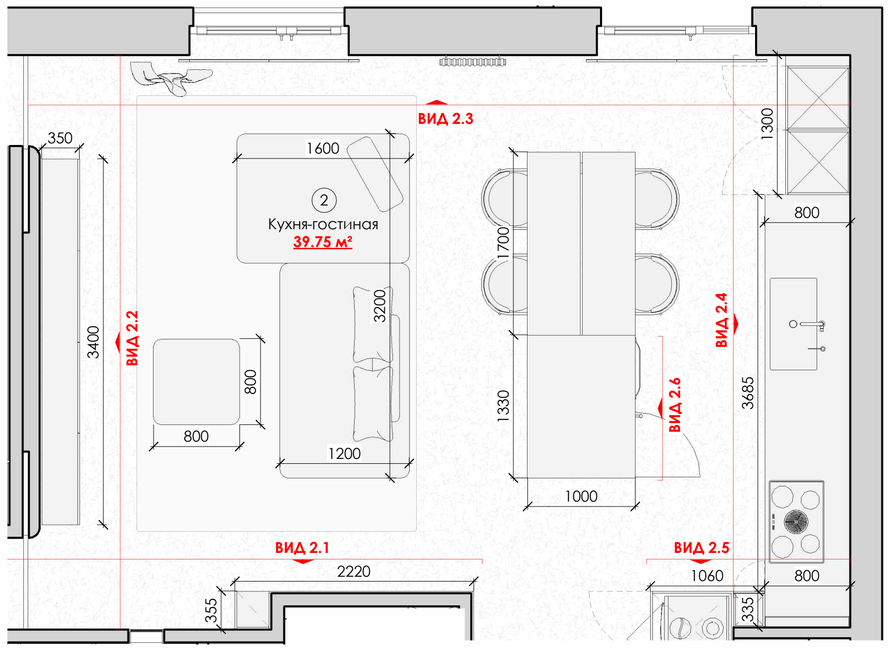

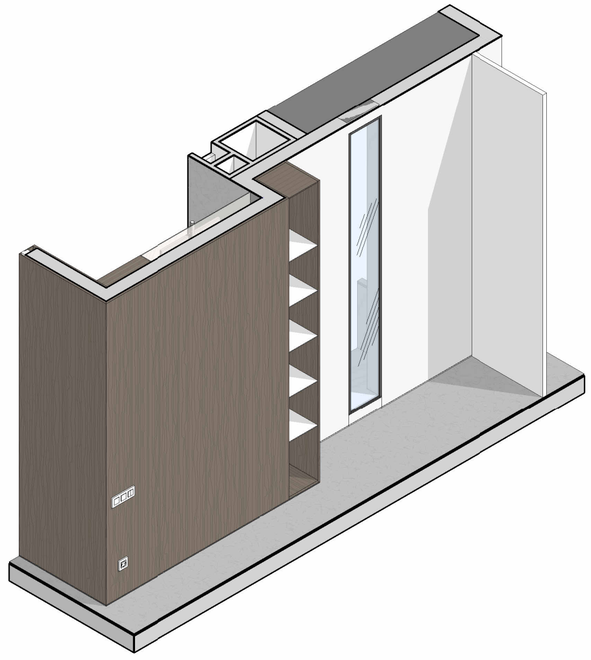

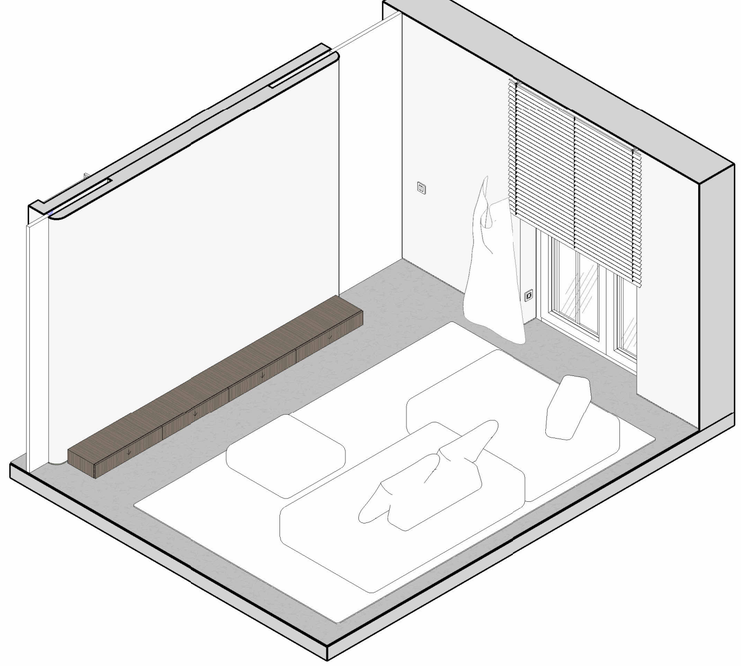

Примечания:

- Все отделочные материалы должны быть выполнены в единой плоскости. При установке материалов учесть их толщину и соблюдение допусков для предотвращения неровностей и зазоров.
- Мебель и встроенные элементы должны быть установлены в соответствии с проектом. Все размеры и положения, указанные в проекте, подлежат перепроверке на этапе монтажа.
- Расположение осветительных приборов, выключателей и розеток соответствует проекту. Необходимо обеспечить правильную высоту установки и проверить расположение электрических точек в реальных условиях.
- До покупки полного объема краски выполнить предварительные выкрасы на небольших участках для проверки цвета и покрытия.

Зеркало

Шпон

Покраска

IVANCHUKINTERIOR

НАИМЕНОВАНИЕ ЧЕРТЕЖА / DRAWING TITLE

РАЗВЕРТКА КУХНИ ГОСТИНОЙ

№ ЛИСТА/ DRAWING NO	19	ВЫПОЛНИЛ/ DRAWN BY	ИВАНЧУК А.Ю.
		ДАТА/ DATE	13.02.2026
		ГОРОД/ CITY	МИНСК

ВИД 2.3

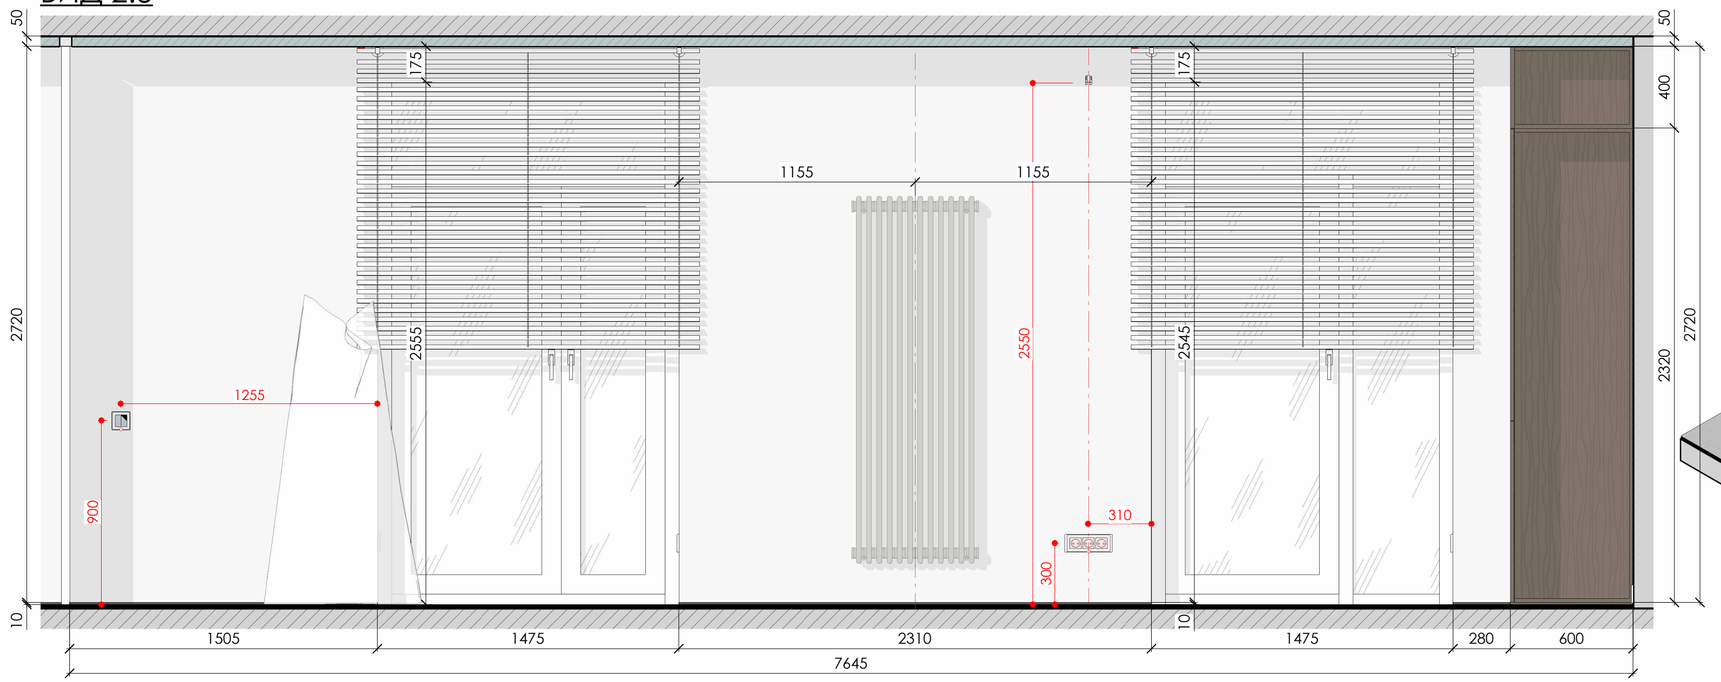

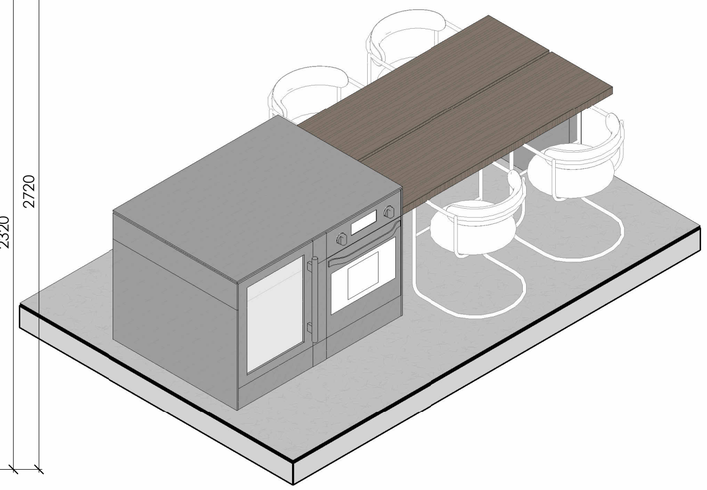

ВИД 2.4

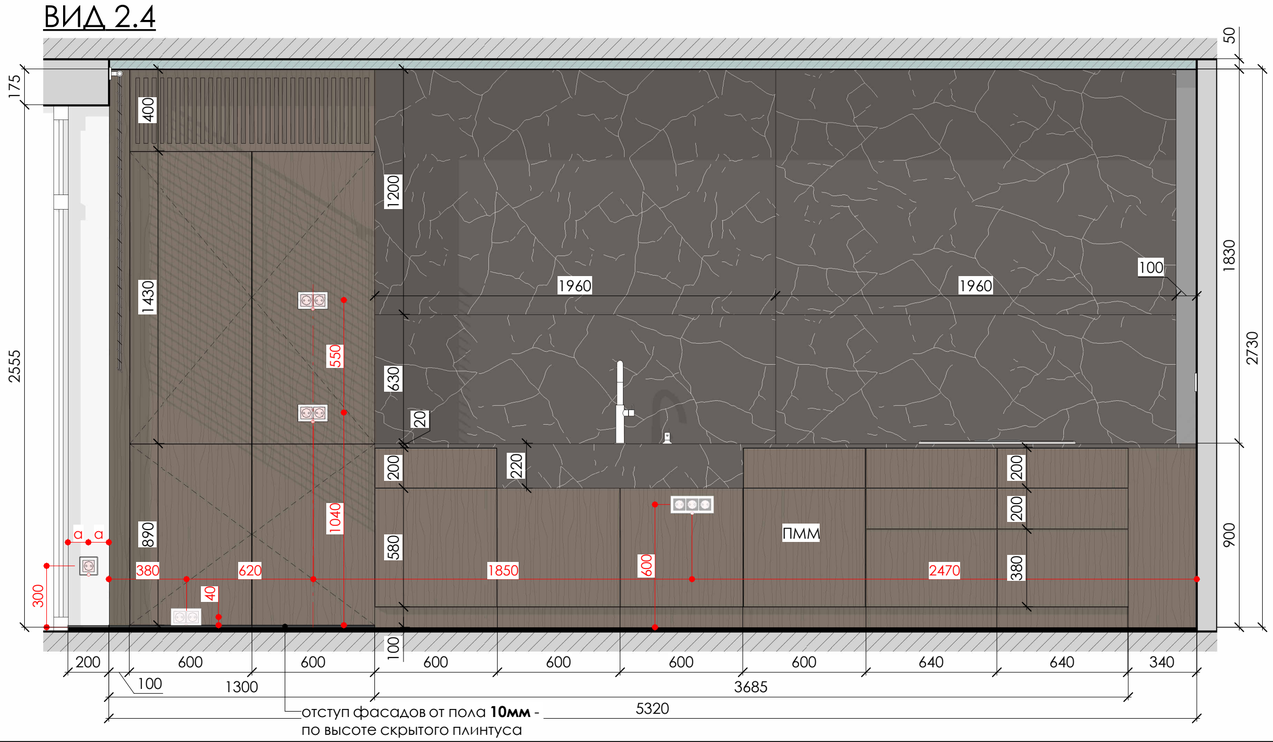

ВИД 2.5

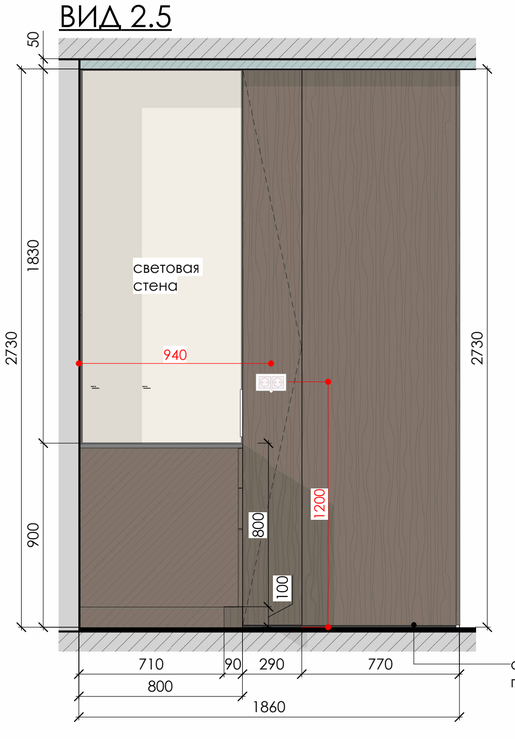

ВИД 2.6

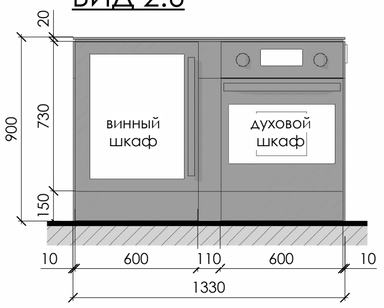

Примечания:

- Все отделочные материалы должны быть выполнены в единой плоскости. При установке материалов учесть их толщину и соблюдение допусков для предотвращения неровностей и зазоров.
- Мебель и встроенные элементы должны быть установлены в соответствии с проектом. Все размеры и положения, указанные в проекте, подлежат перепроверке на этапе монтажа.
- Расположение осветительных приборов, выключателей и розеток соответствует проекту. Необходимо обеспечить правильную высоту установки и проверить расположение электрических точек в реальных условиях.
- До покупки полного объема краски выполнить предварительные выкрасы на небольших участках для проверки цвета и покрытия.

Зеркало

Шпон

Покраска

Керамогранит
Flaviker / Supreme Memories / Breccia Imperiale (Nat / Natural)
120×280см x 6мм

IVANCHUKINTERIOR

НАИМЕНОВАНИЕ ЧЕРТЕЖА / DRAWING TITLE

РАЗВЕРТКА КУХНИ ГОСТИНОЙ

№ ЛИСТА/ DRAWING NO	19.1	ВЫПОЛНИЛ/ DRAWN BY	ИВАНЧУК А.Ю.
		ДАТА/ DATE	13.02.2026
		ГОРОД/ CITY	МИНСК

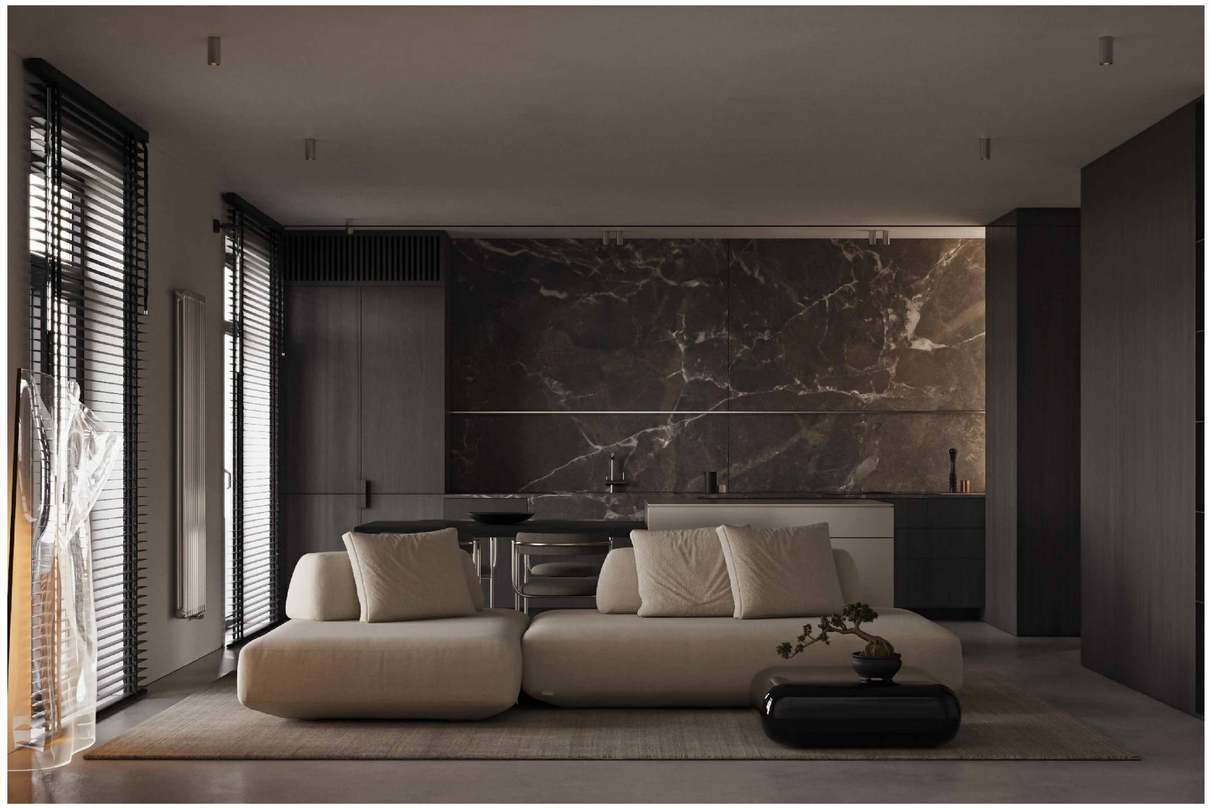

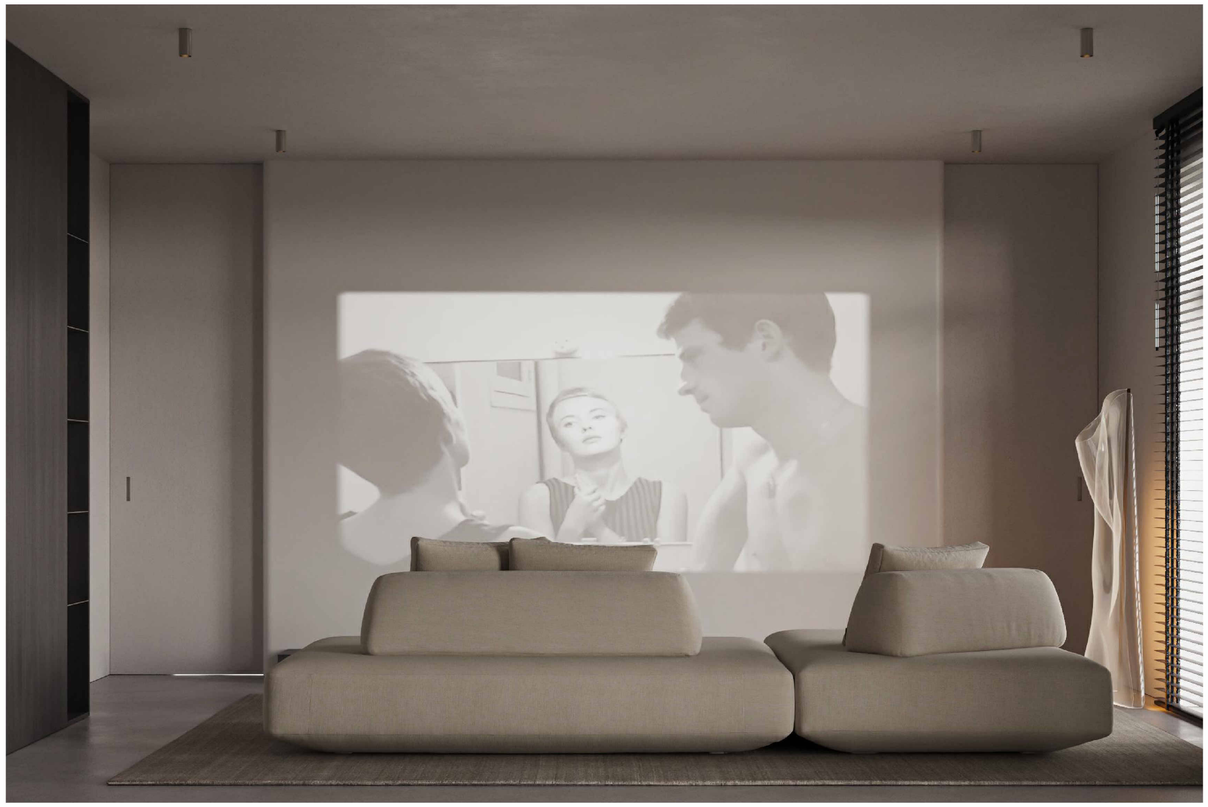

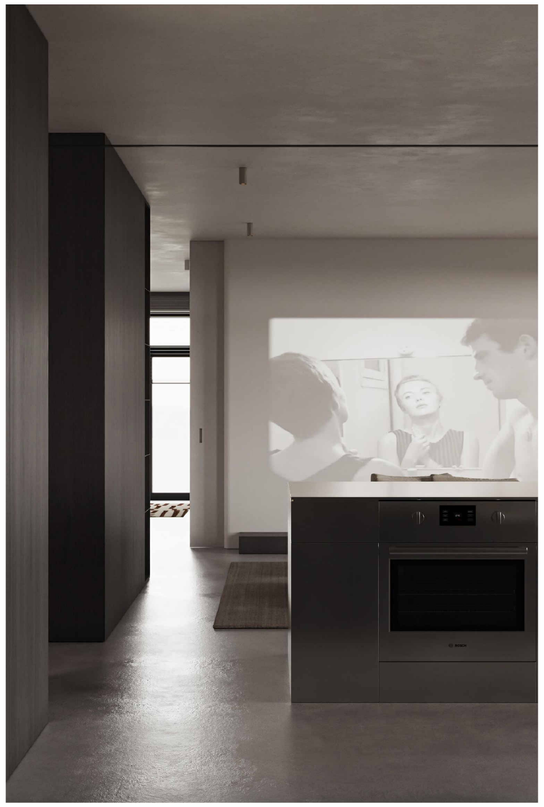

ВИД 4.1

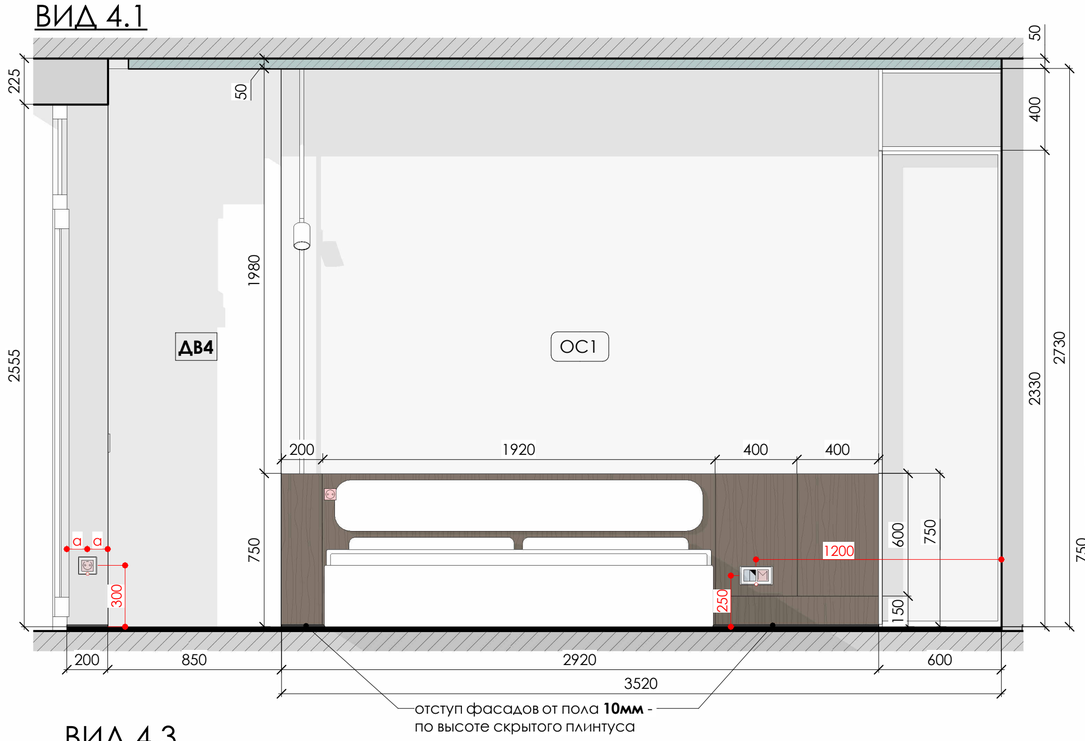

ВИД 4.2

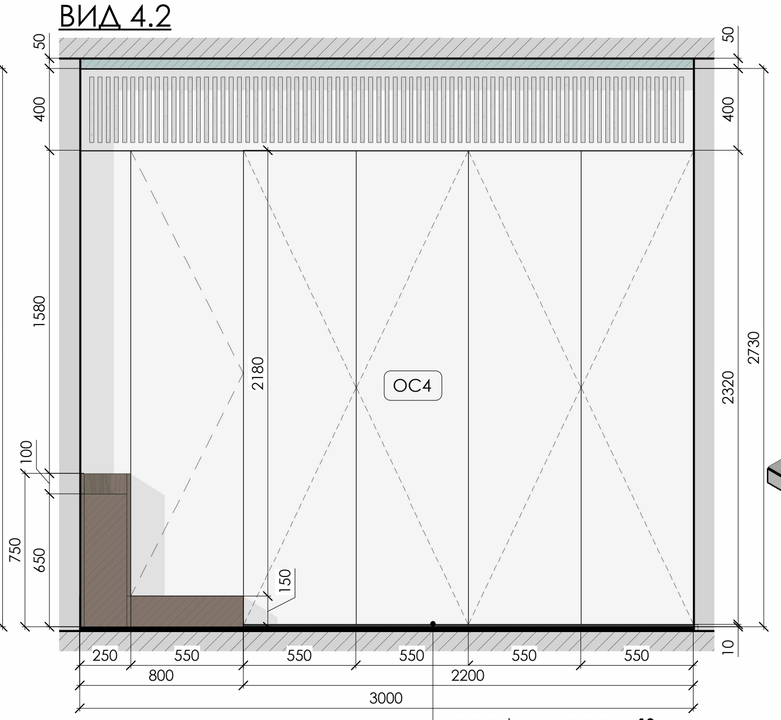

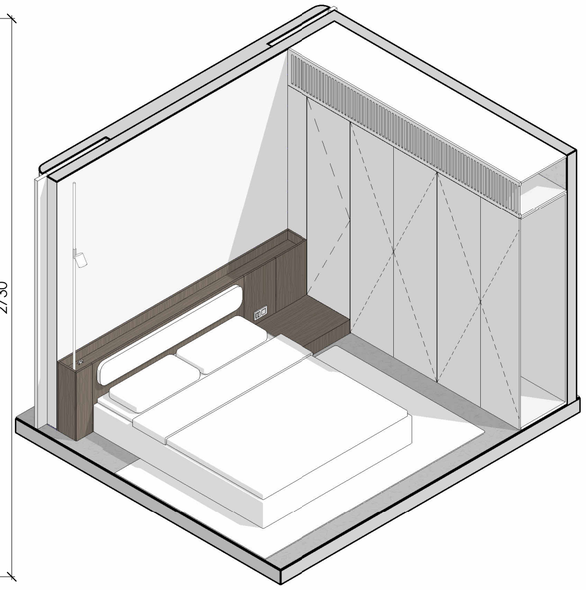

ВИД 4.3

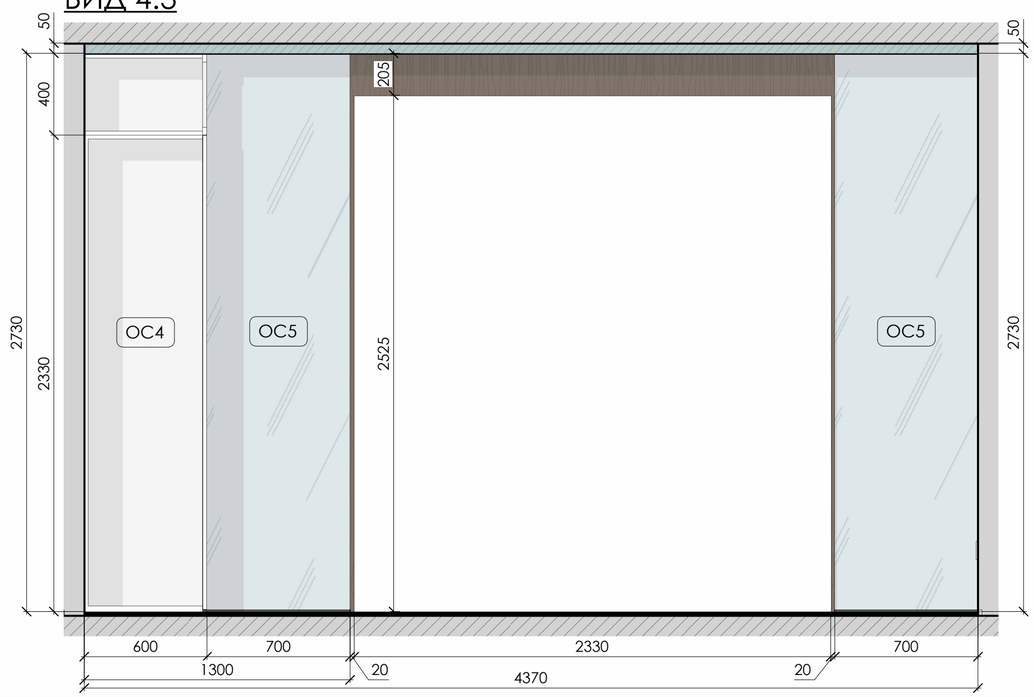

ВИД 4.4

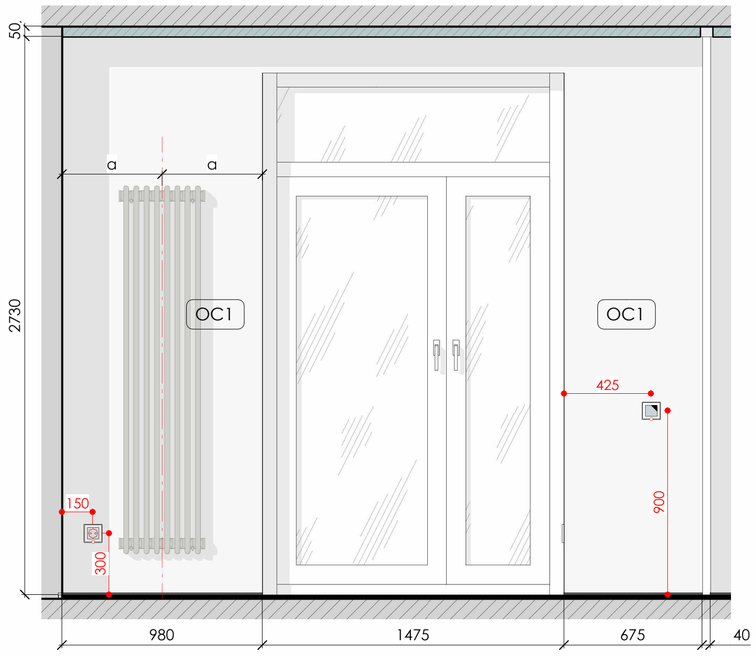

ПОМ. 4, СПАЛЬНЯ.

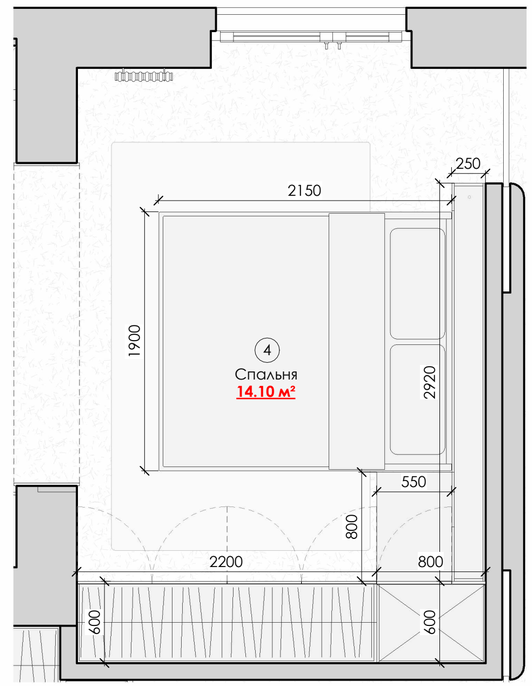

Примечания:

- Все отделочные материалы должны быть выполнены в единой плоскости. При установке материалов учесть их толщину и соблюдение допусков для предотвращения неровностей и зазоров.
- Мебель и встроенные элементы должны быть установлены в соответствии с проектом. Все размеры и положения, указанные в проекте, подлежат перепроверке на этапе монтажа.
- Расположение осветительных приборов, выключателей и розеток соответствует проекту. Необходимо обеспечить правильную высоту установки и проверить расположение электрических точек в реальных условиях.
- До покупки полного объема краски выполнить предварительные выкрасы на небольших участках для проверки цвета и покрытия.

Зеркало

Шпон

Покраска

IVANCHUKINTERIOR

НАИМЕНОВАНИЕ ЧЕРТЕЖА / DRAWING TITLE

РАЗВЕРТКА СПАЛЬНИ

№ ЛИСТА/ DRAWING NO	20	ВЫПОЛНИЛ/ DRAWN BY	ИВАНЧУК А.Ю.
		ДАТА/ DATE	13.02.2026
		ГОРОД/ CITY	МИНСК

ВИД 5.1

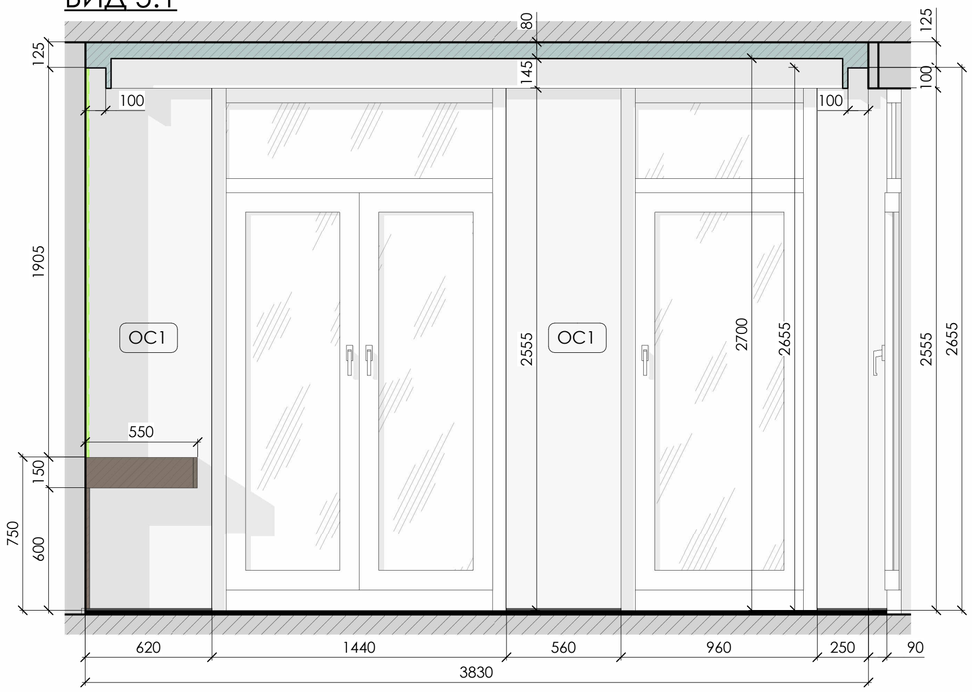

ВИД 5.2

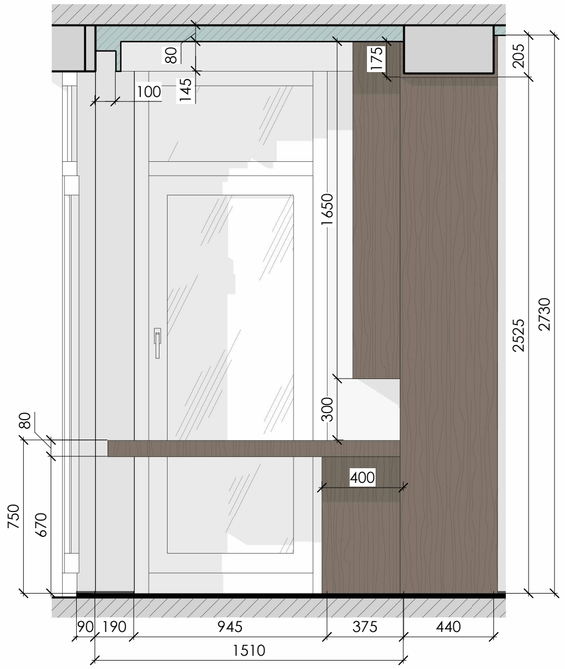

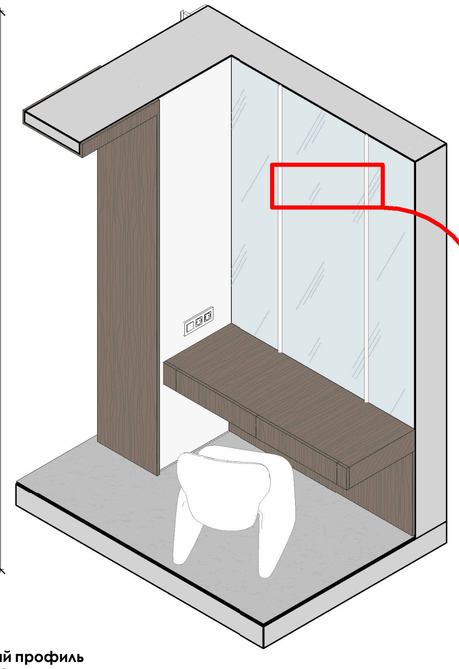

ВИД 5.3

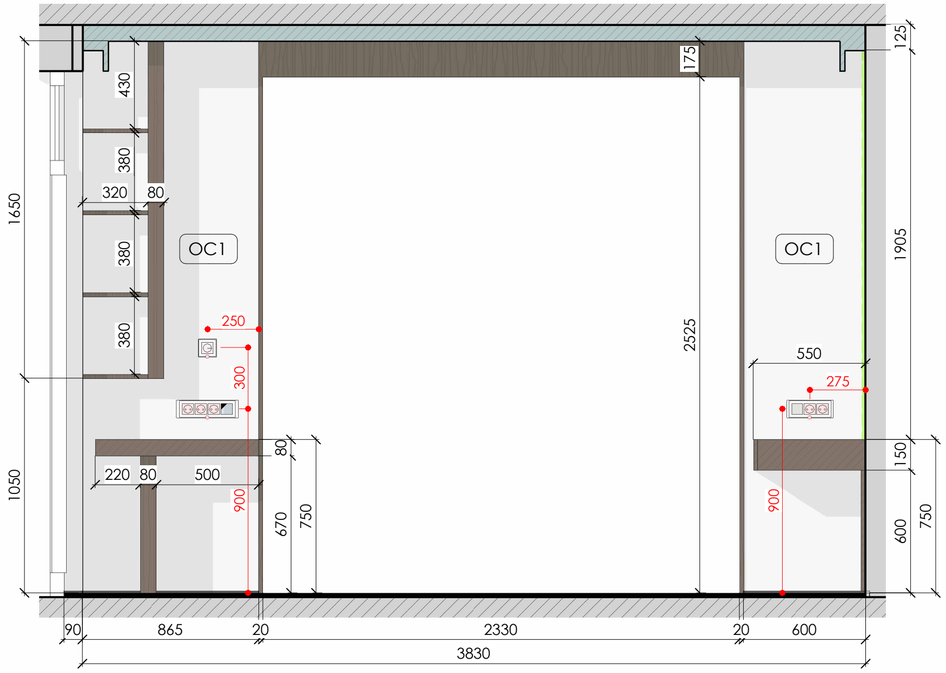

ВИД 5.4

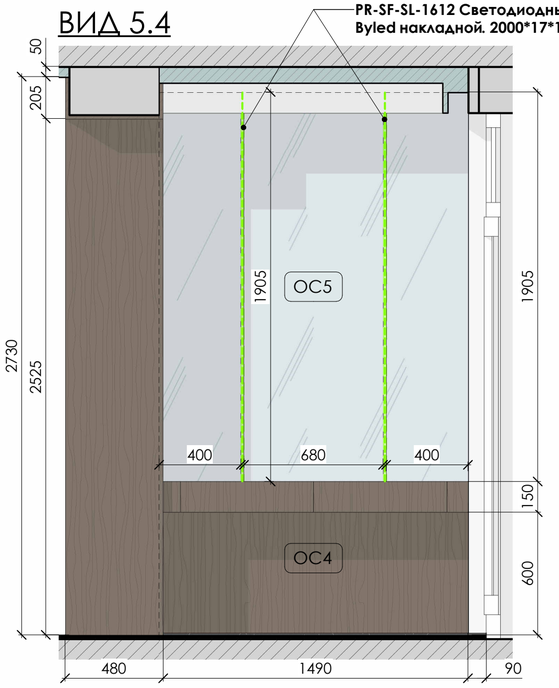

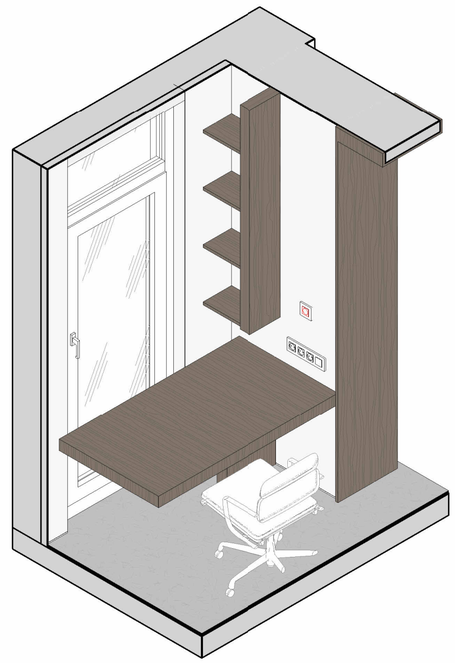

ПОМ. 5, ЛОДЖИЯ.

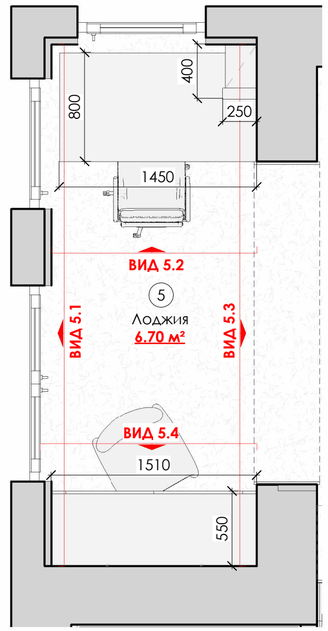

Примечания:

- Все отделочные материалы должны быть выполнены в единой плоскости. При установке материалов учесть их толщину и соблюдение допусков для предотвращения неровностей и зазоров.
- Мебель и встроенные элементы должны быть установлены в соответствии с проектом. Все размеры и положения, указанные в проекте, подлежат перепроверке на этапе монтажа.
- Расположение осветительных приборов, выключателей и розеток соответствует проекту. Необходимо обеспечить правильную высоту установки и проверить расположение электрических точек в реальных условиях.
- До покупки полного объема краски выполнить предварительные выкрасы на небольших участках для проверки цвета и покрытия.

Зеркало

Шпон

Покраска

IVANCHUKINTERIOR

НАИМЕНОВАНИЕ ЧЕРТЕЖА / DRAWING TITLE

РАЗВЕРТКА ЛОДЖИИ

№ ЛИСТА/ DRAWING NO	20.1	ВЫПОЛНИЛ/ DRAWN BY	ИВАНЧУК А.Ю.
		ДАТА/ DATE	13.02.2026
		ГОРОД/ CITY	МИНСК

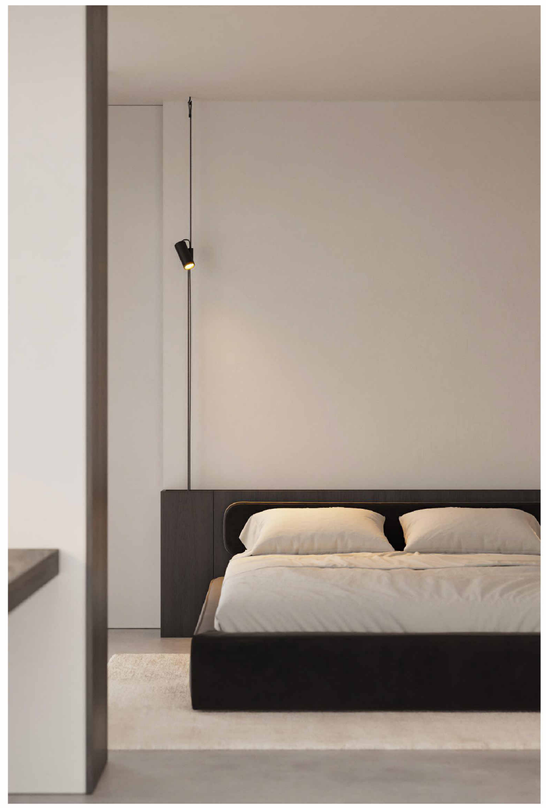

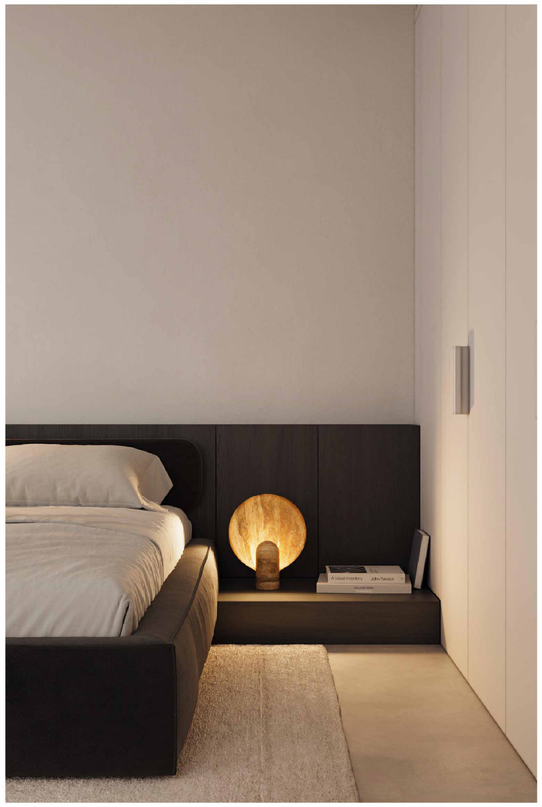

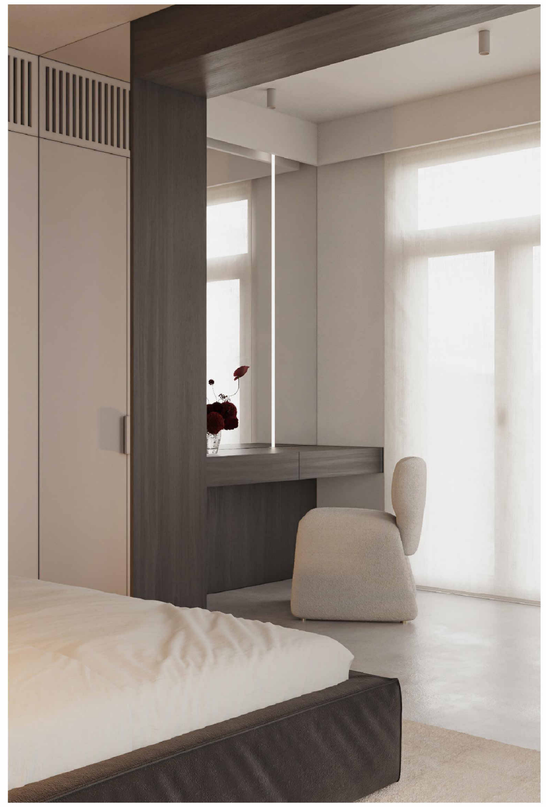

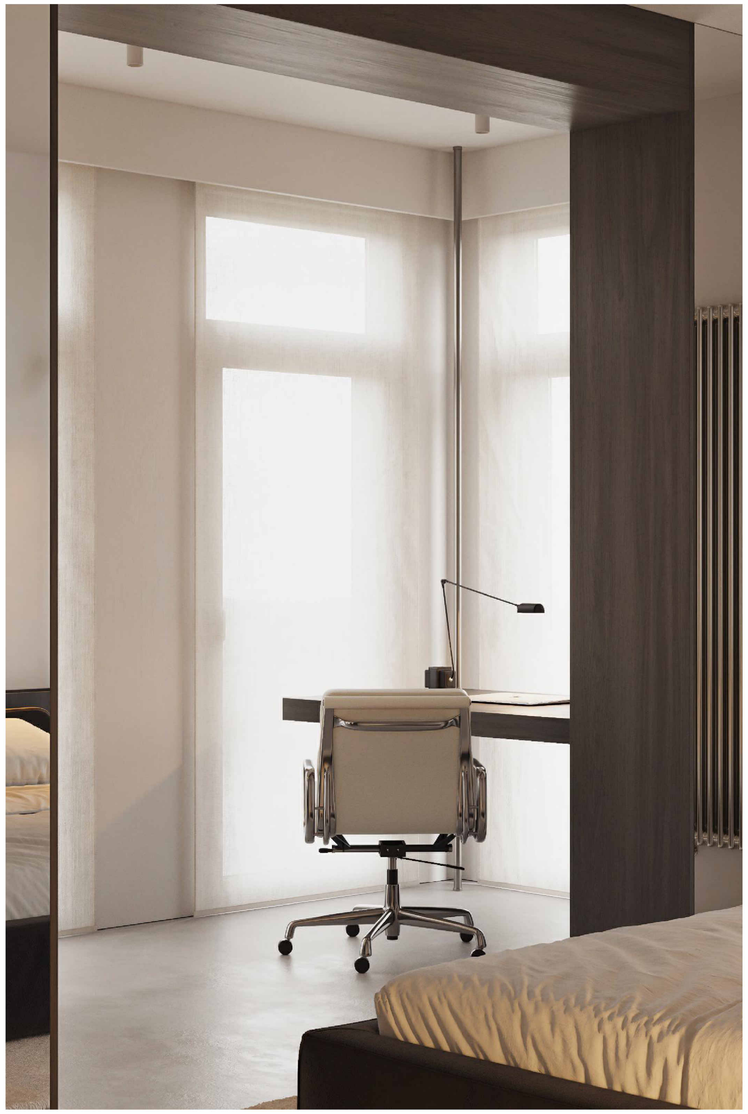

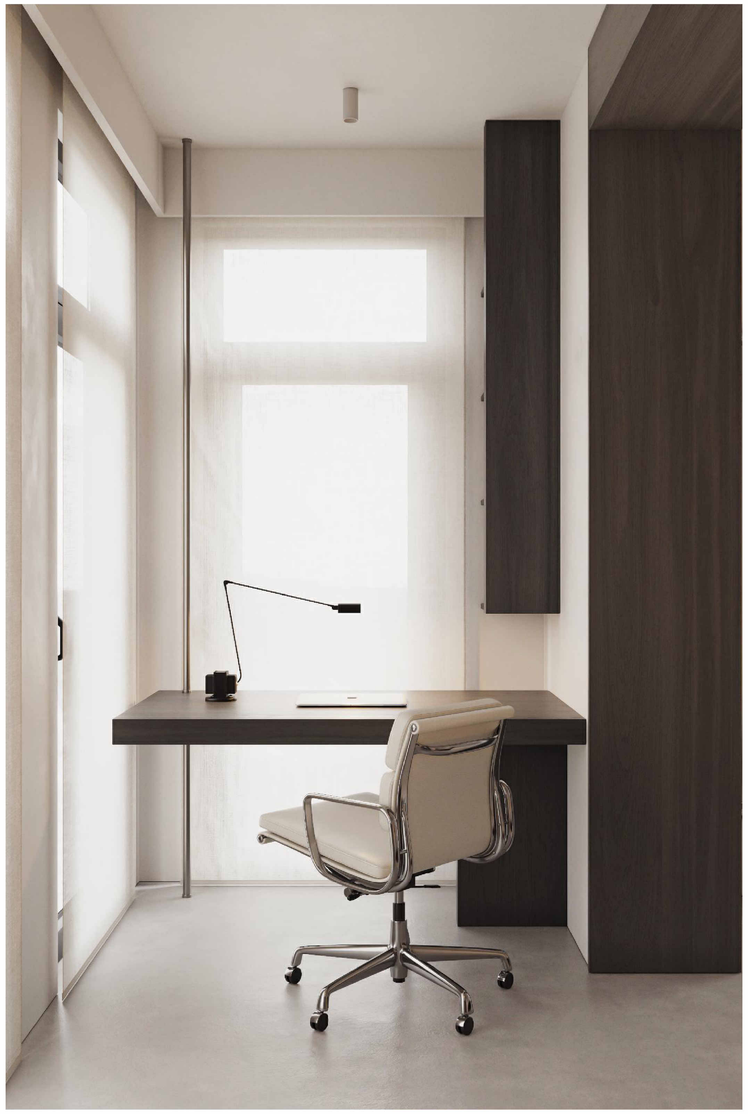

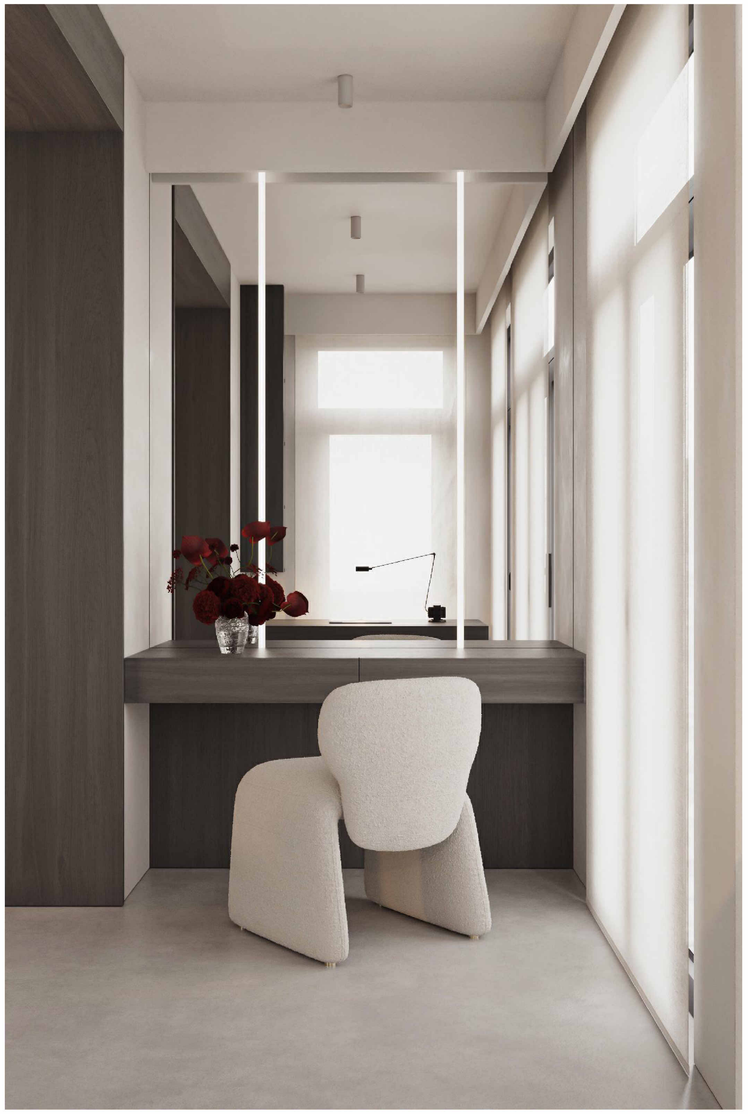

ВИД 6.1

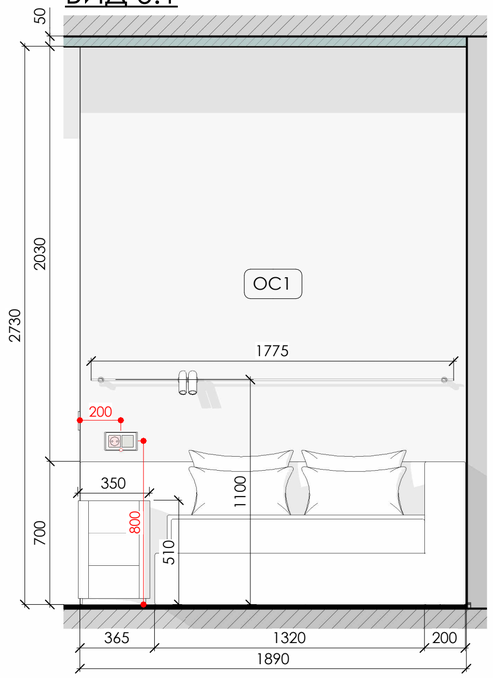

ВИД 6.2

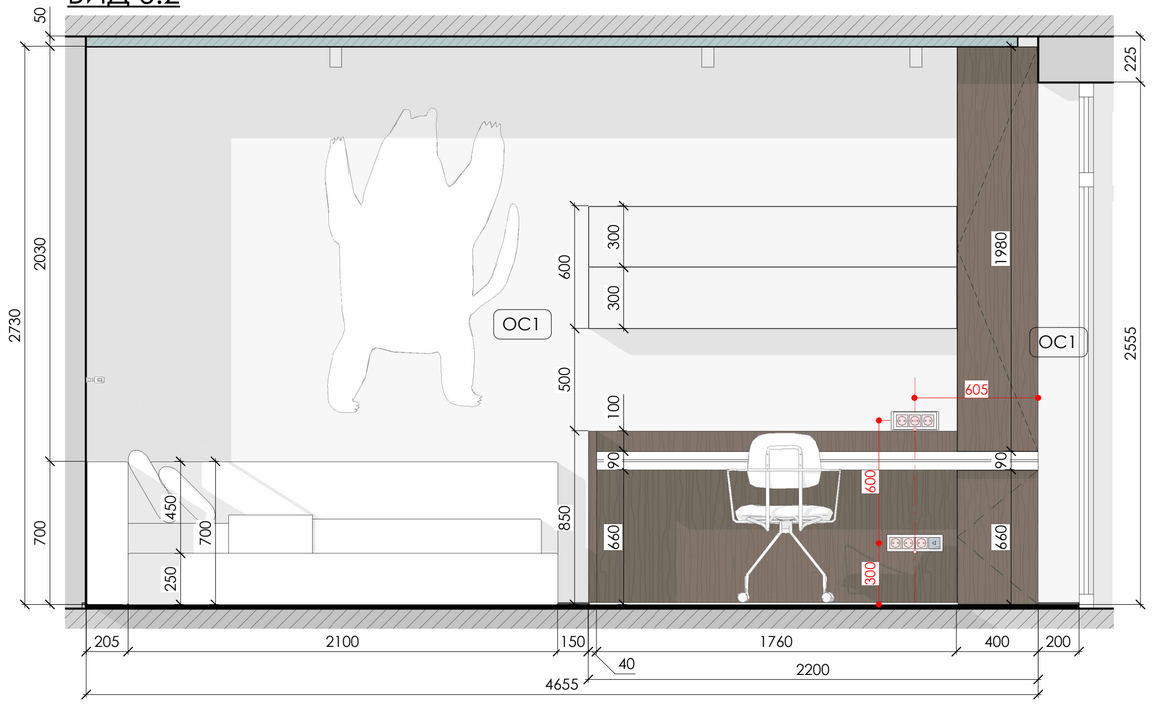

ВИД 6.3

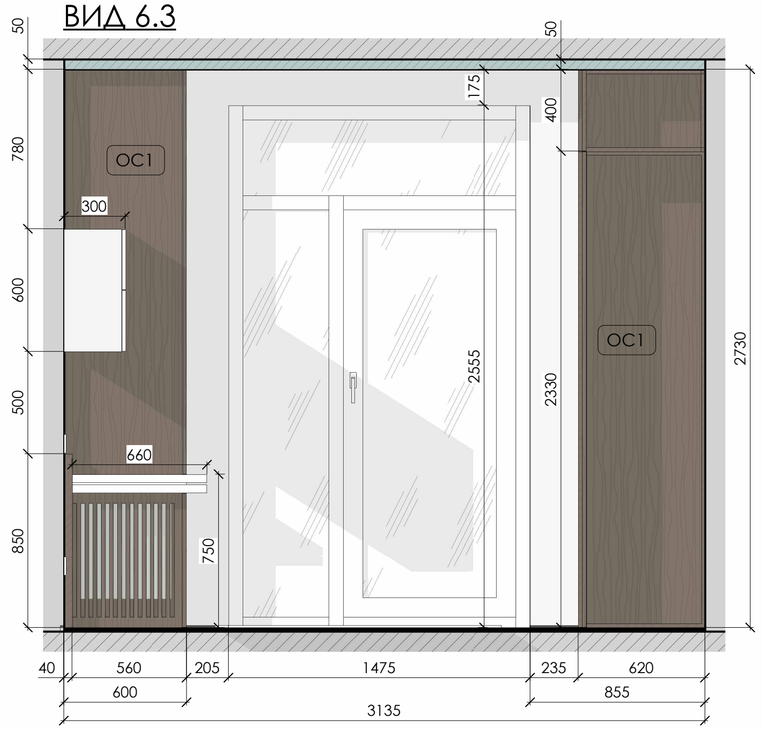

ВИД 6.4

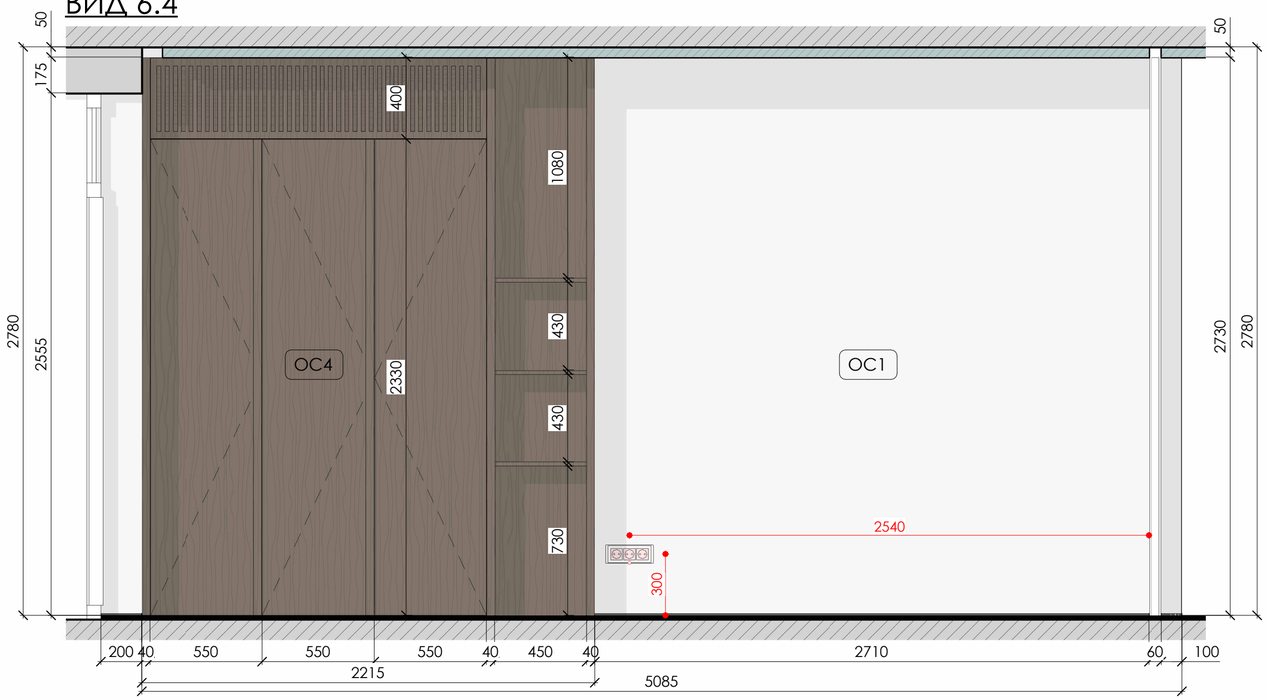

ПОМ. 6, ДЕТСКАЯ

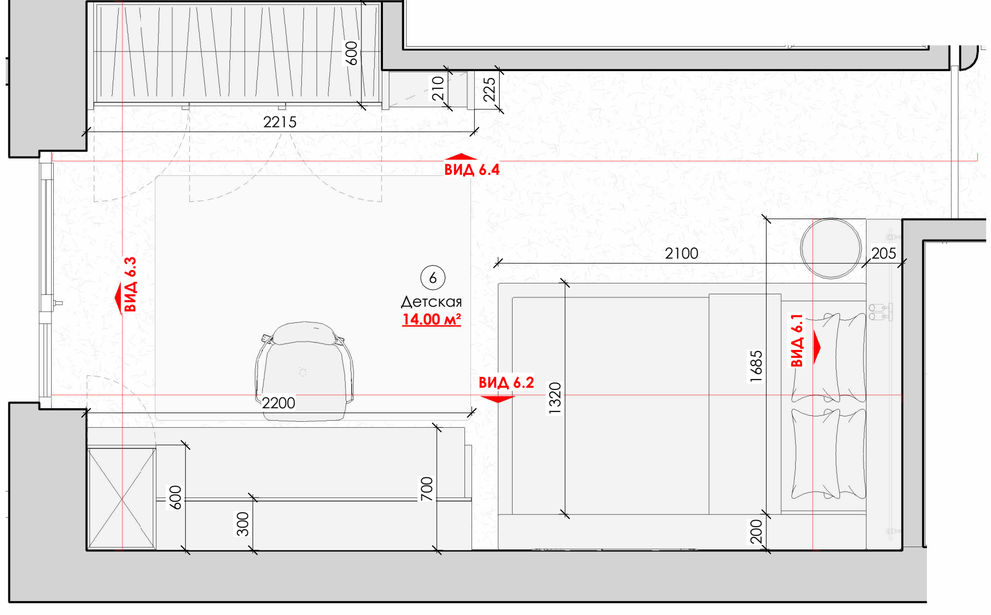

Примечания:

- Все отделочные материалы должны быть выполнены в единой плоскости. При установке материалов учесть их толщину и соблюдение допусков для предотвращения неровностей и зазоров.
- Мебель и встроенные элементы должны быть установлены в соответствии с проектом. Все размеры и положения, указанные в проекте, подлежат перепроверке на этапе монтажа.
- Расположение осветительных приборов, выключателей и розеток соответствует проекту. Необходимо обеспечить правильную высоту установки и проверить расположение электрических точек в реальных условиях.
- До покупки полного объема краски выполнить предварительные выкрасы на небольших участках для проверки цвета и покрытия.

Шпон

Покраска

IVANCHUKINTERIOR

НАИМЕНОВАНИЕ ЧЕРТЕЖА / DRAWING TITLE

РАЗВЕРТКА ДЕТСКОЙ

№ ЛИСТА/ DRAWING NO	21	ВЫПОЛНИЛ/ DRAWN BY	ИВАНЧУК А.Ю.
		ДАТА/ DATE	13.02.2026
		ГОРОД/ CITY	МИНСК

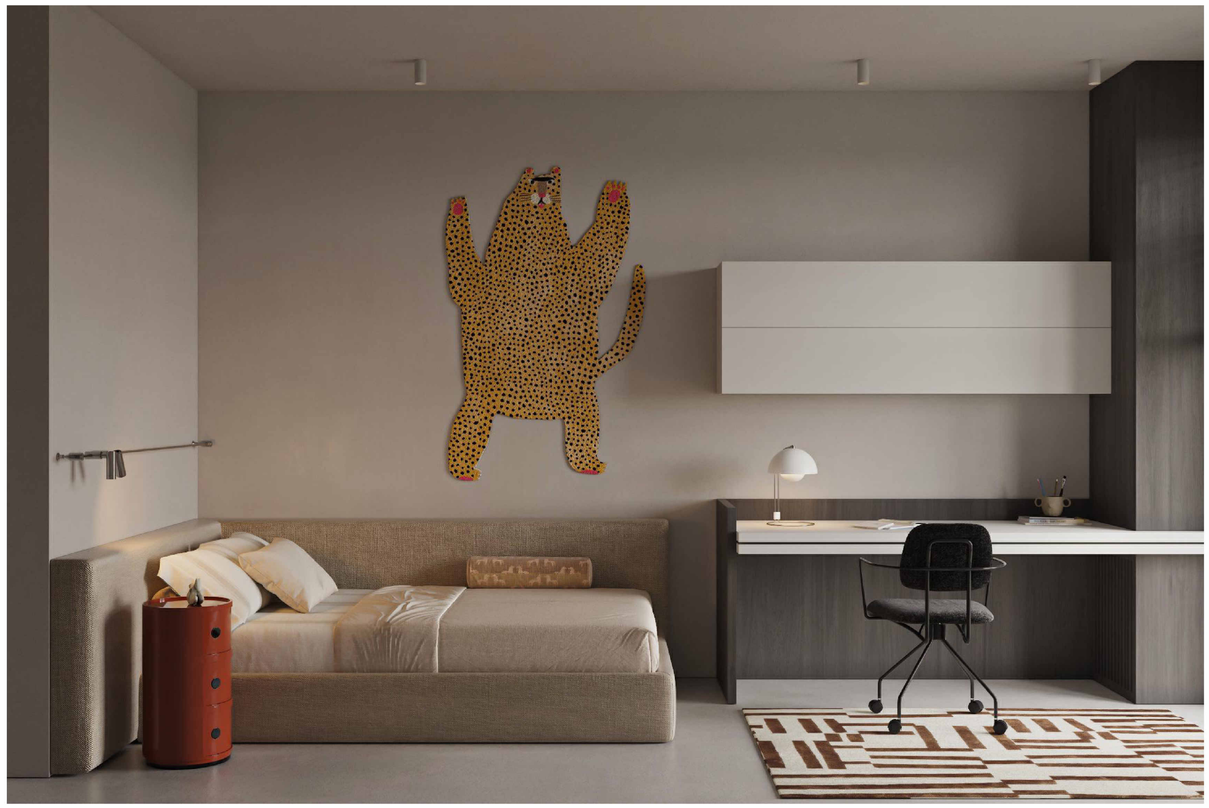

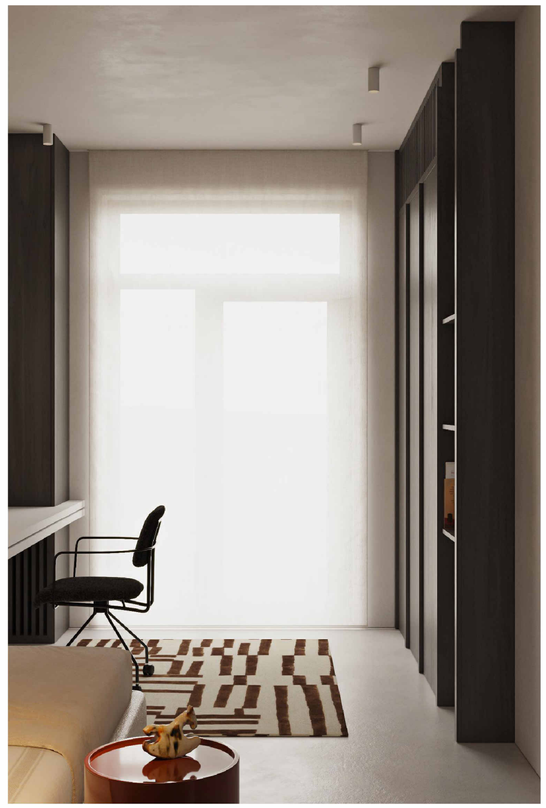

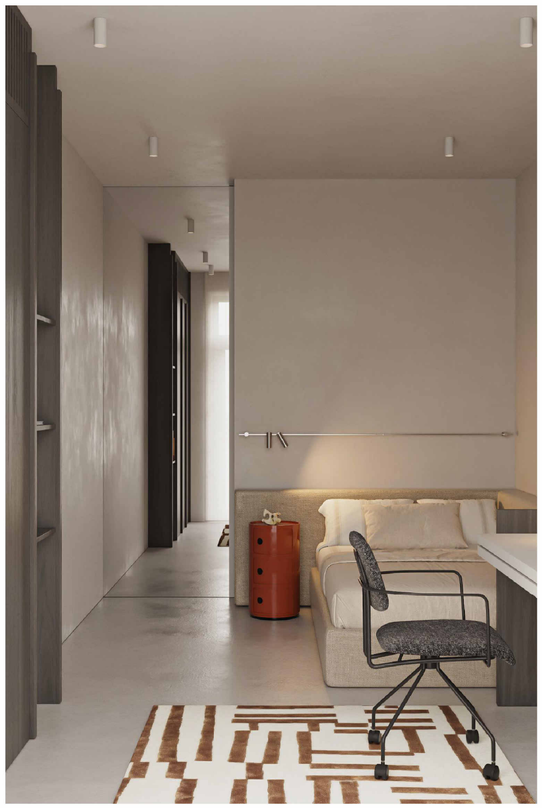

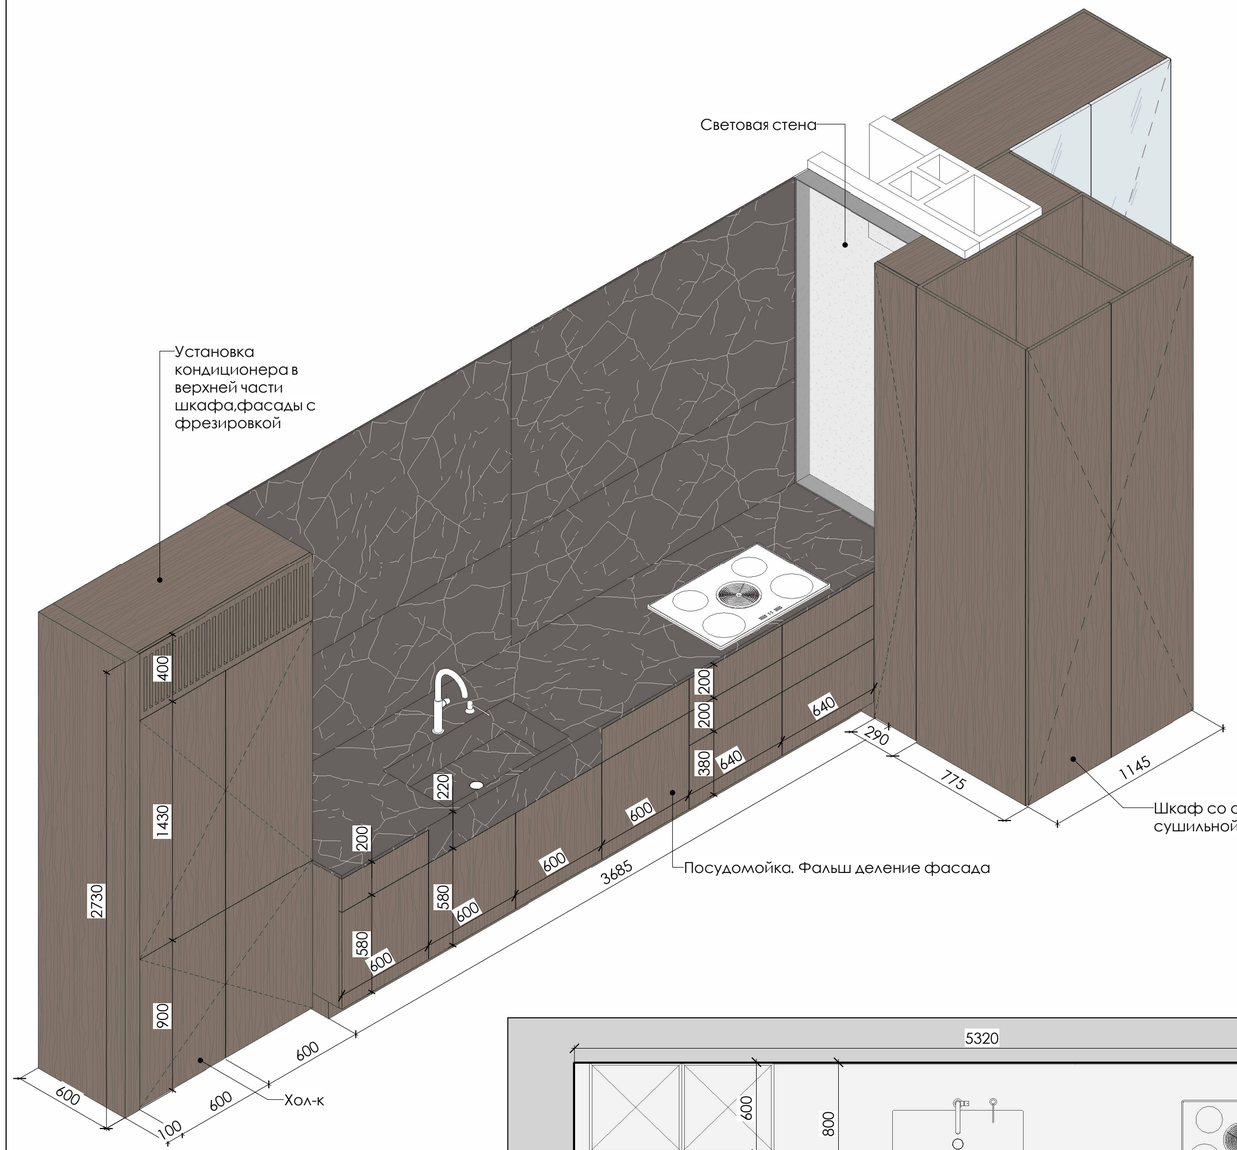

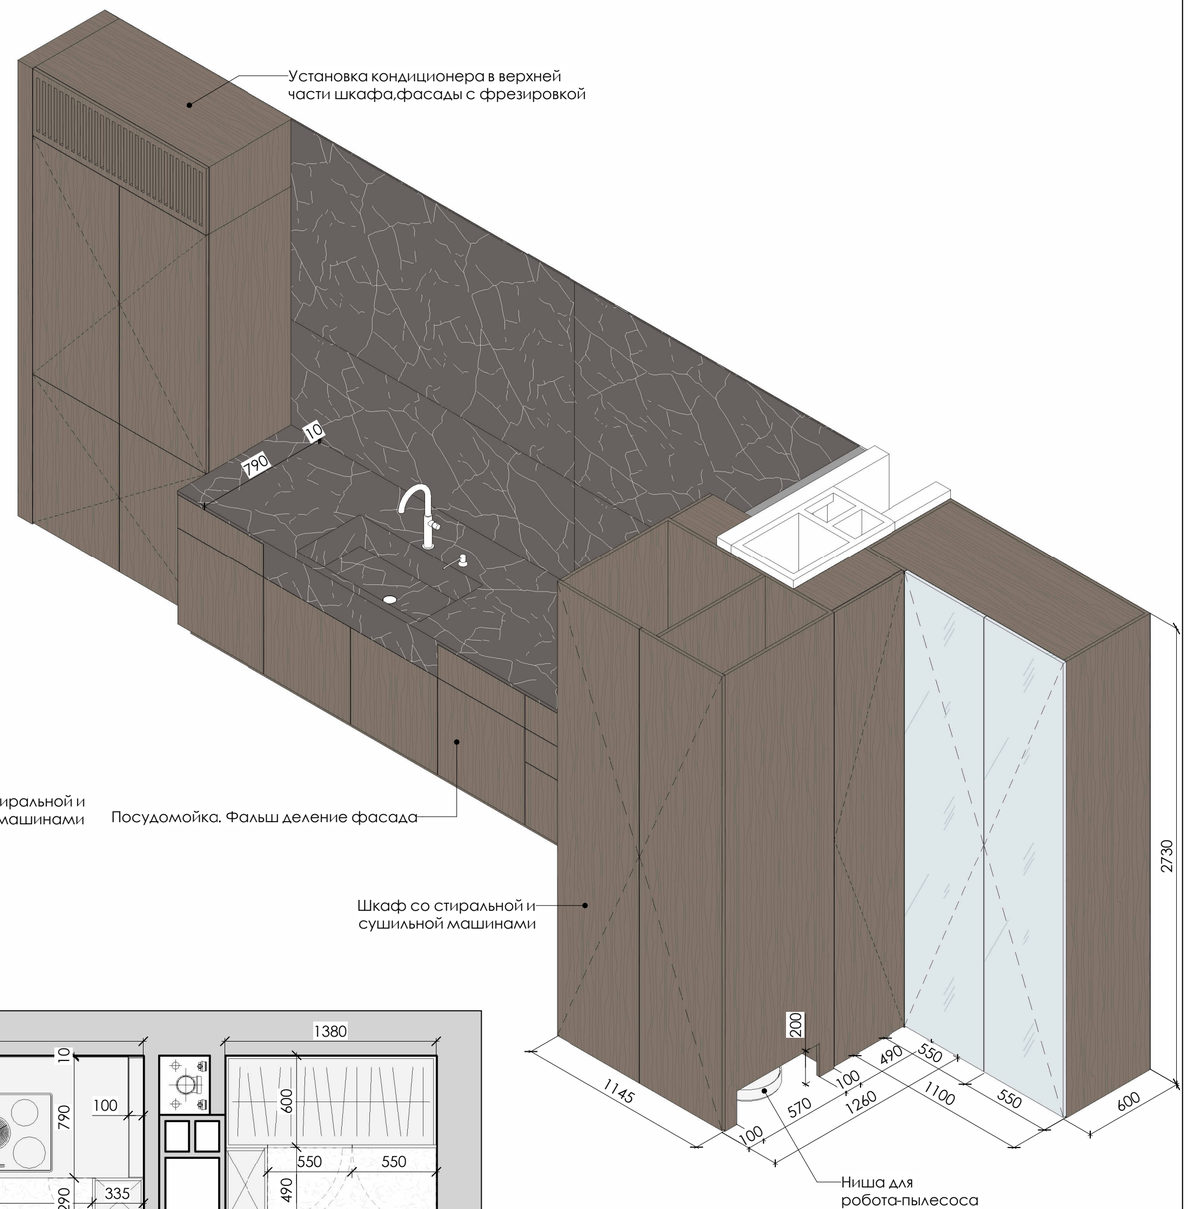

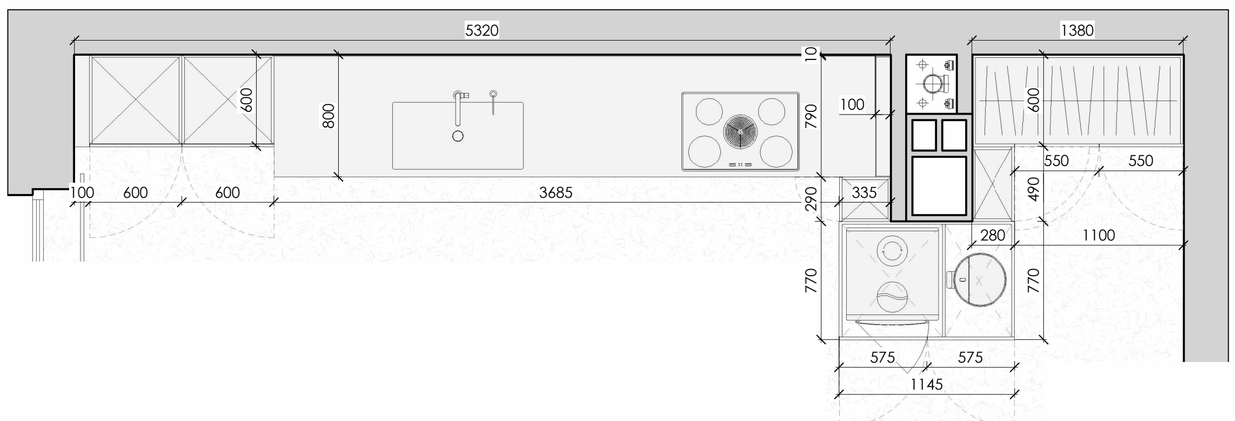

Ниша для робота-пылесоса

IVANCHUKINTERIOR

НАИМЕНОВАНИЕ ЧЕРТЕЖА / DRAWING TITLE

3Д схема шкафов в прихожей + кухня

№ ЛИСТА/ DRAWING NO	22	ВЫПОЛНИЛ/ DRAWN BY	ИВАНЧУК А.Ю.
		ДАТА/ DATE	13.02.2026
		ГОРОД/ CITY	МИНСК